


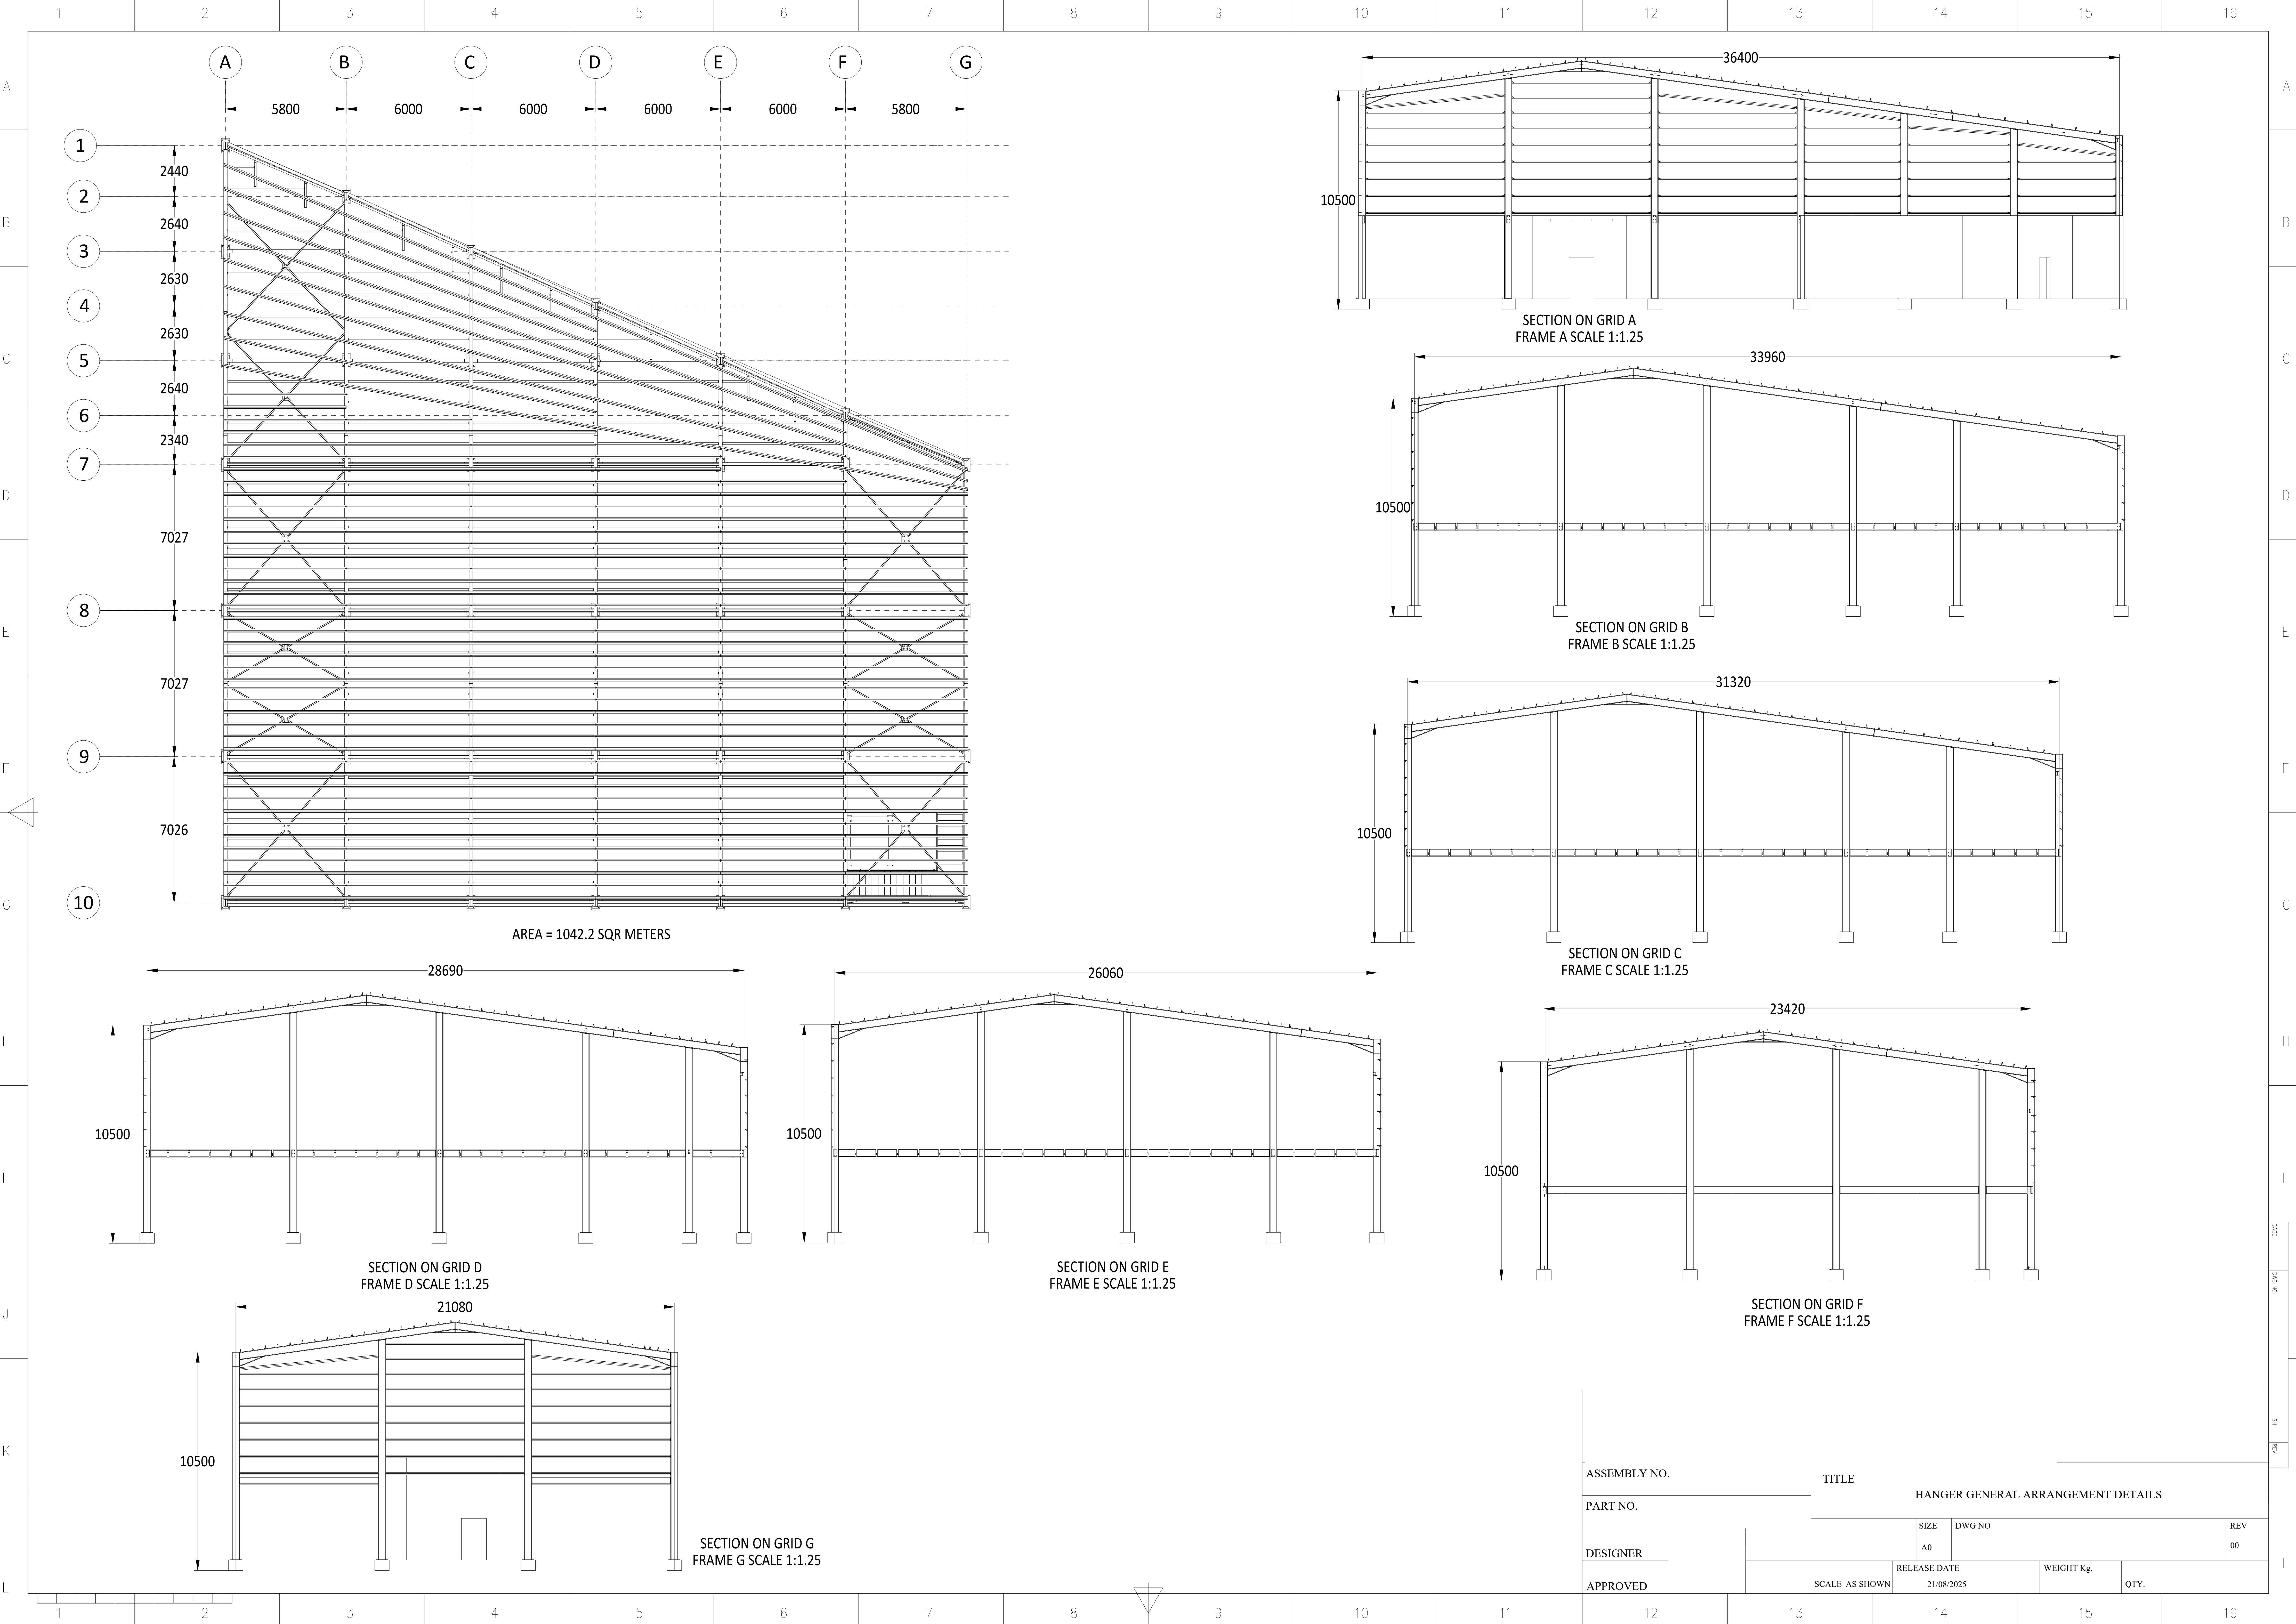

ASSEMBLY NO.

PART NO.

DESIGNER

APPROVED

TITLE

HANGER GENERAL ARRANGEMENT DETAILS

SIZE

A0

DWG NO

RELEASE DATE


21/08/2025


WEIGHT Kg.

QTY.


REV

00

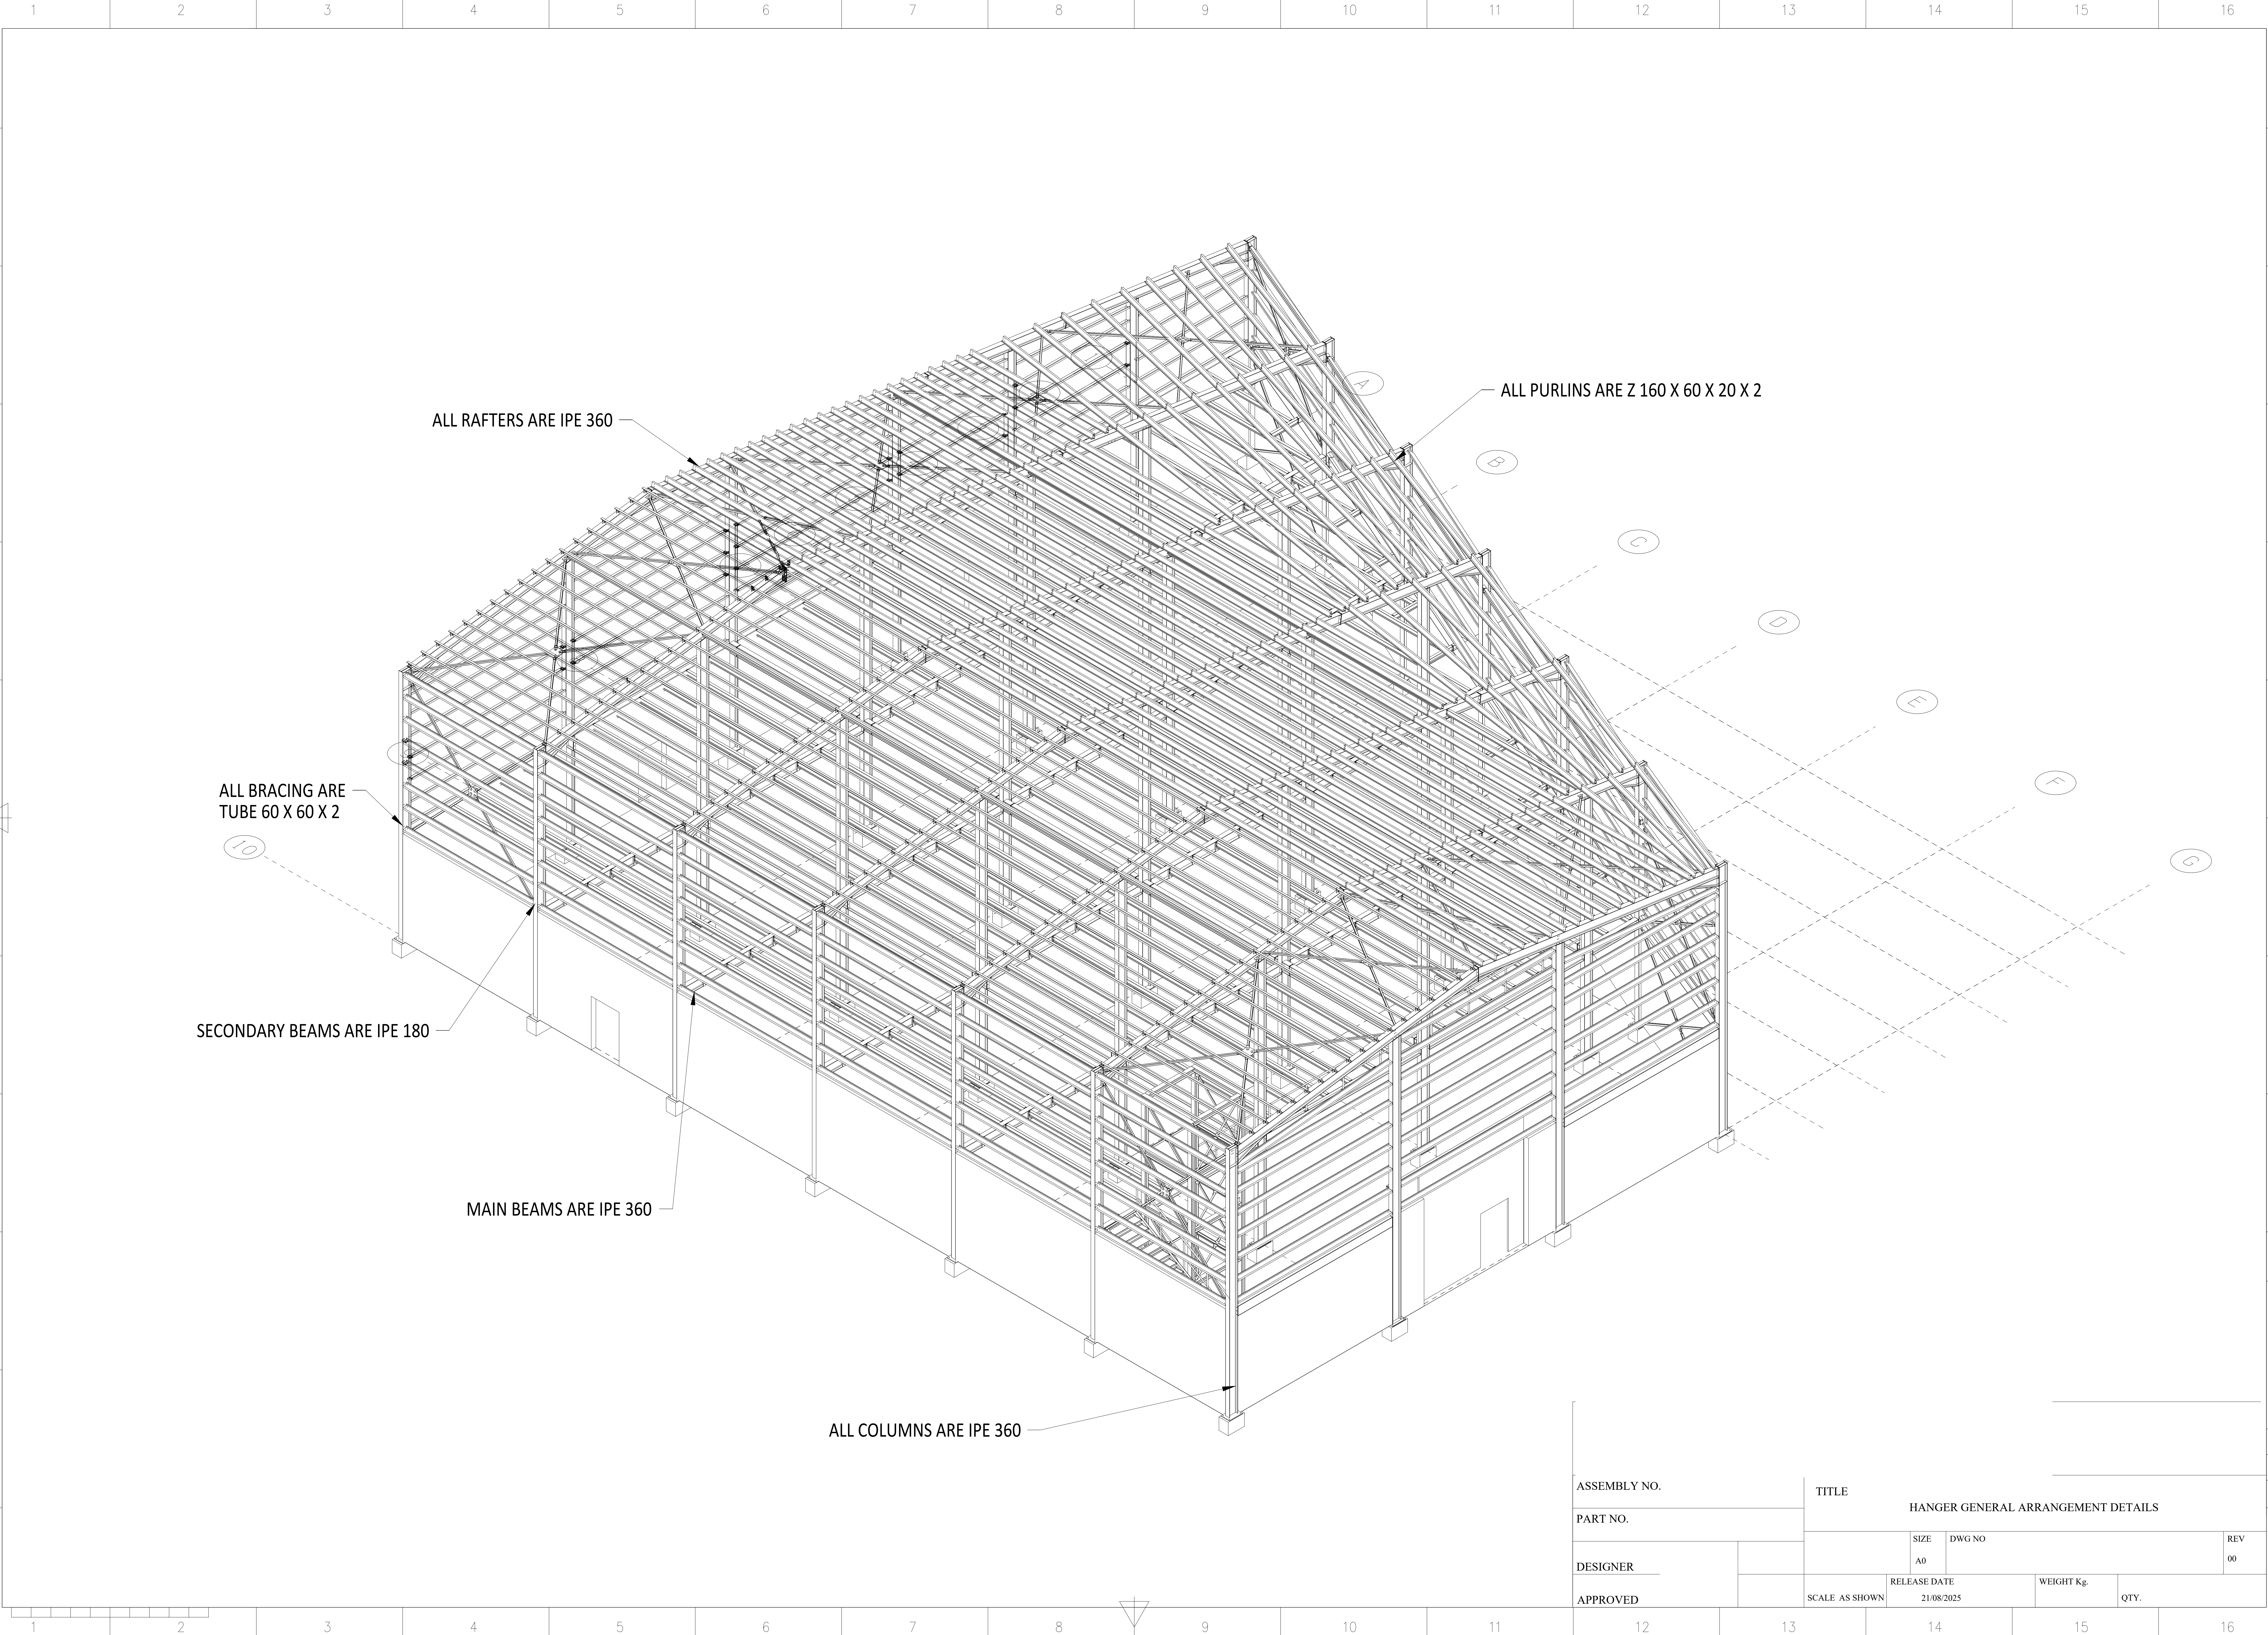


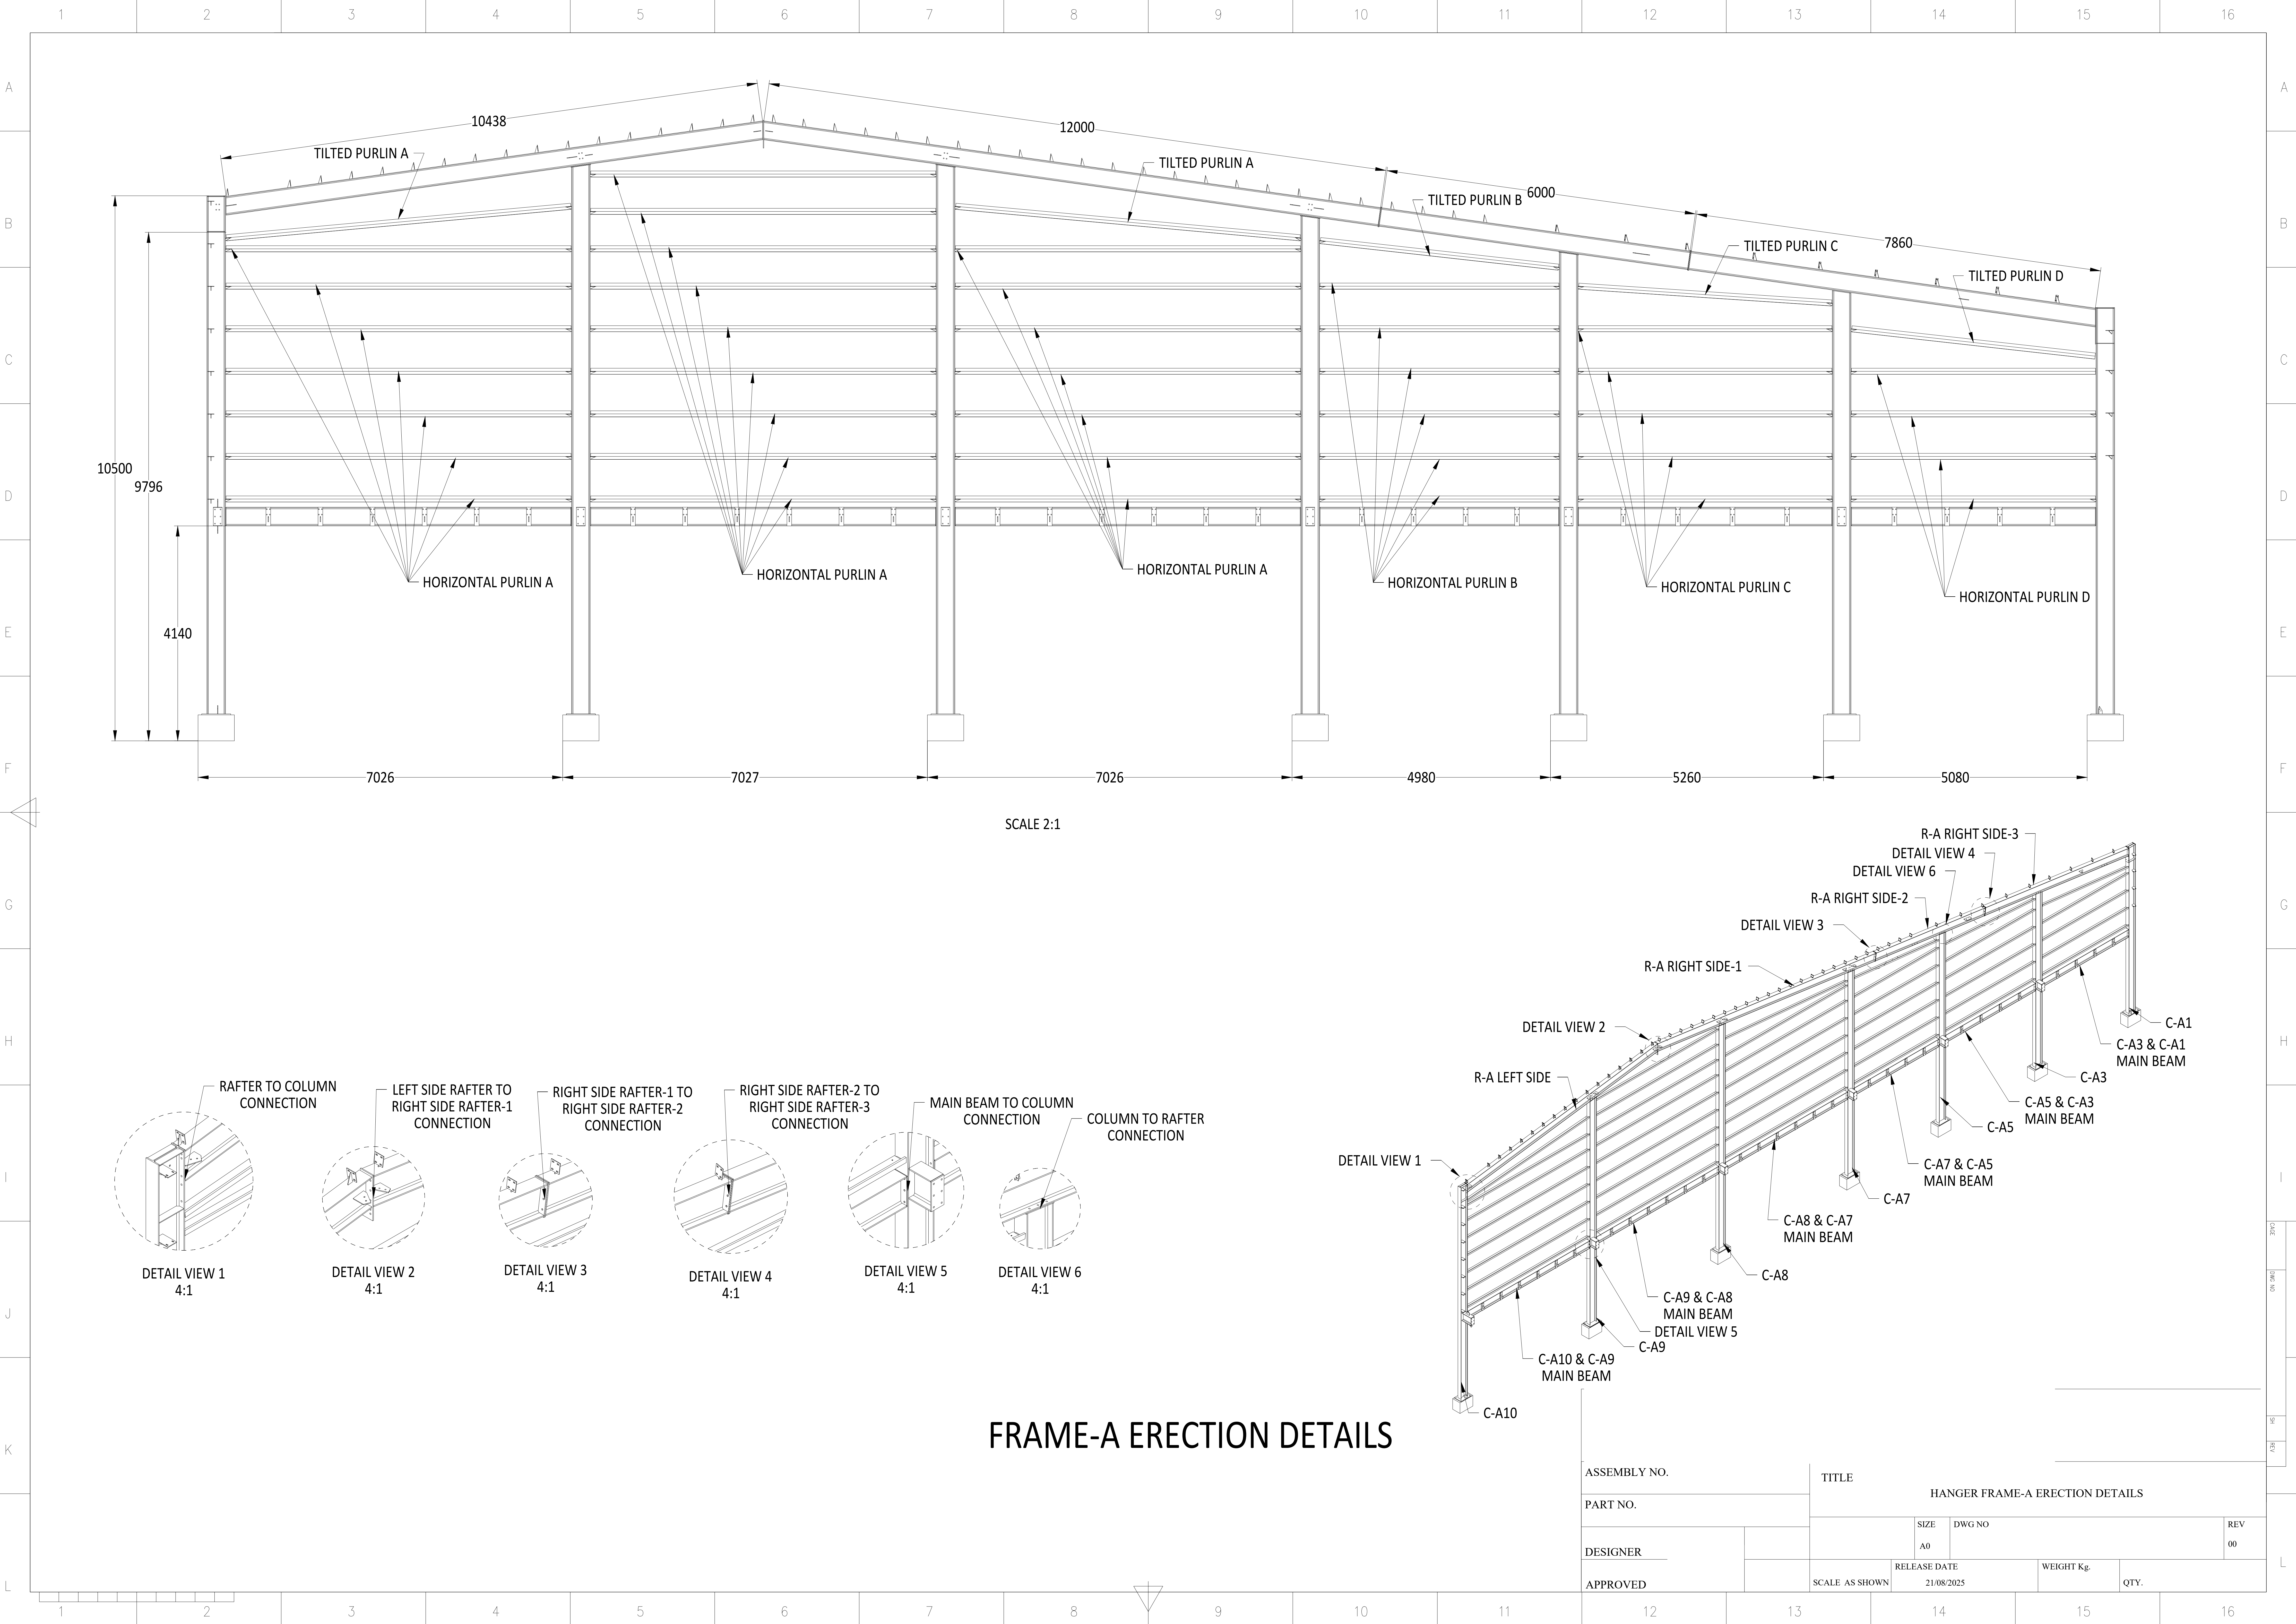

ASSEMBLY NO.		TITLE			
PART NO.		HANGER FRAME-A ERECTION DETAILS			
DESIGNER		SIZE	DWG NO	REV	
APPROVED		A0		00	
SCALE AS SHOWN		RELEASE DATE	WEIGHT Kg.	QTY.	
		21/08/2025			

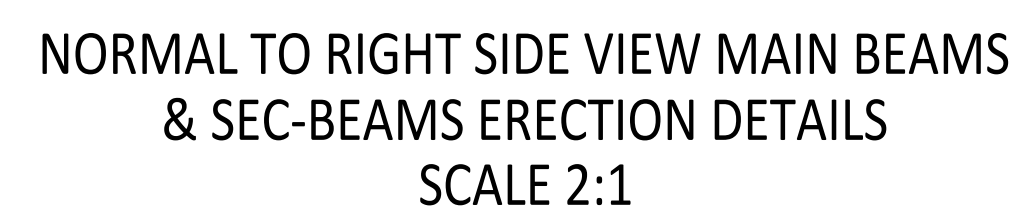


(FRAME-A & FRAME-B) MAIN BEAMS, SECONDARY BEAMS ERECTION DETAILS

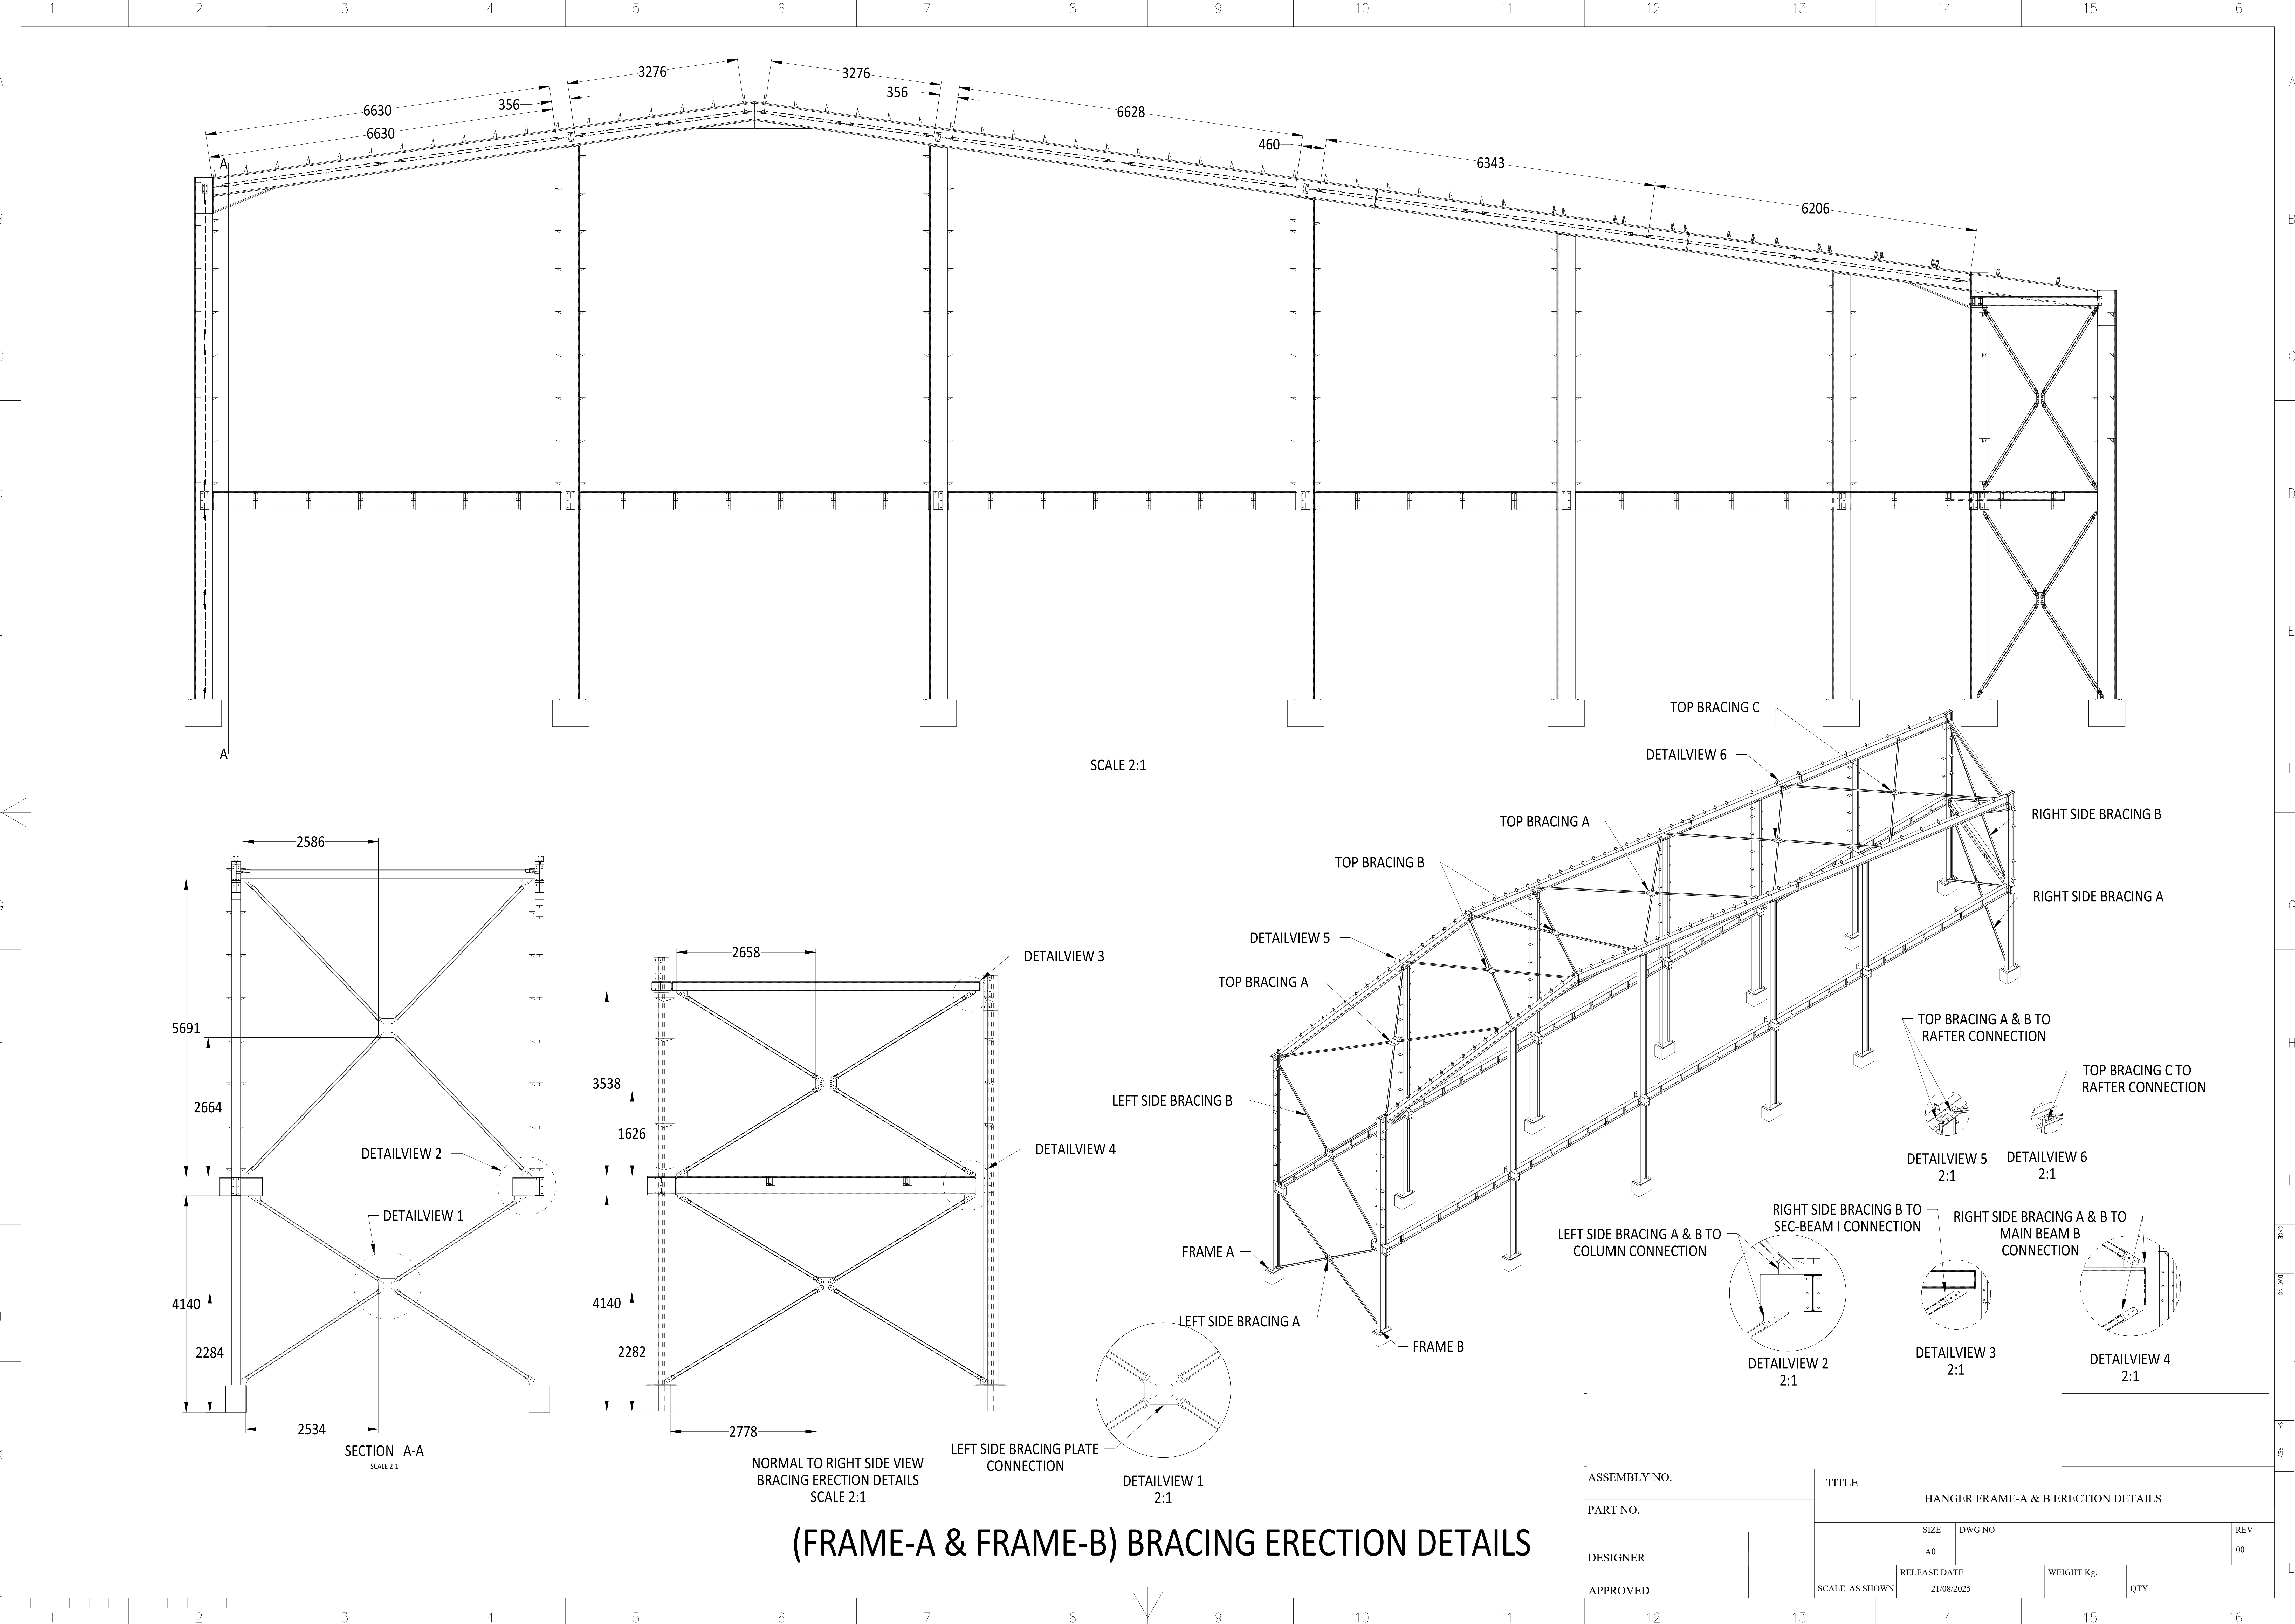




(FRAME-A & FRAME-B) BRACING ERECTION DETAILS

ASSEMBLY NO.		TITLE			
PART NO.		HANGER FRAME-A & B ERECTION DETAILS			
DESIGNER		SIZE	DWG NO	REV	
APPROVED		A0		00	
SCALE AS SHOWN		RELEASE DATE	WEIGHT Kg.	QTY.	
		21/08/2025			

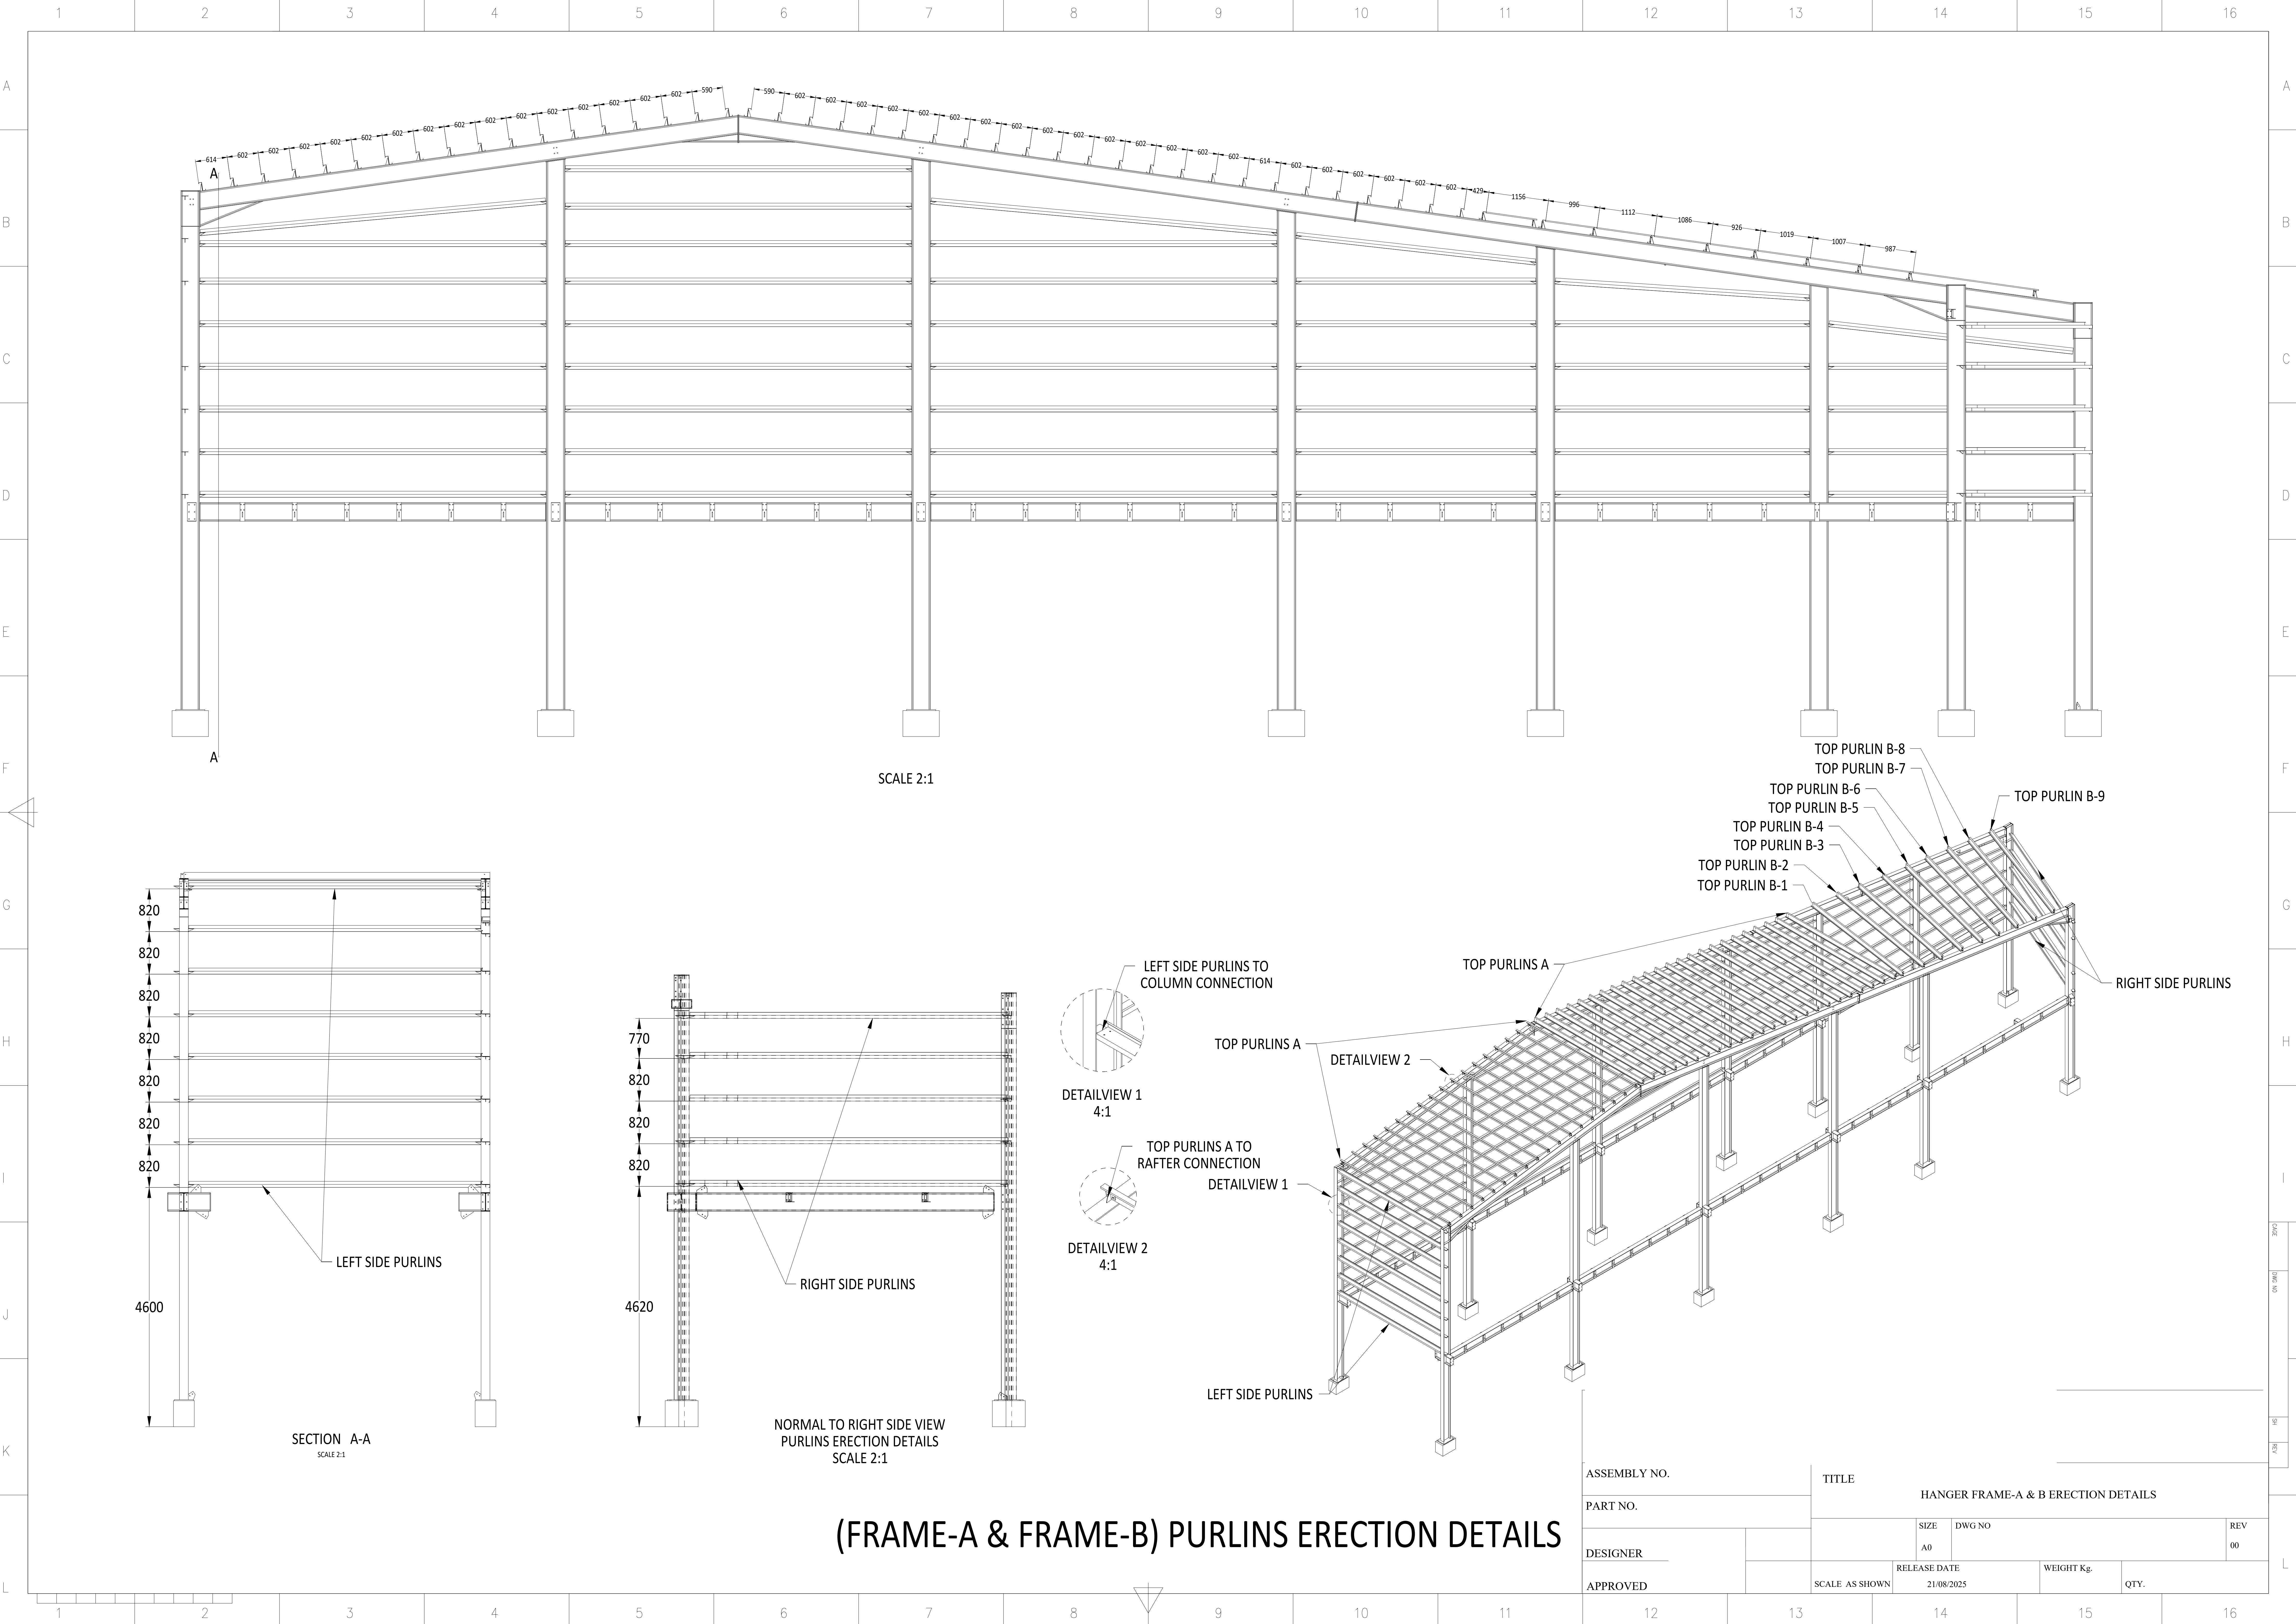

(FRAME-A & FRAME-B) PURLINS ERECTION DETAILS

ASSEMBLY NO.		TITLE			
PART NO.		HANGER FRAME-A & B ERECTION DETAILS			
DESIGNER		SIZE	DWG NO	REV	
APPROVED		A0		00	
SCALE AS SHOWN		RELEASE DATE		WEIGHT Kg.	QTY.
		21/08/2025			

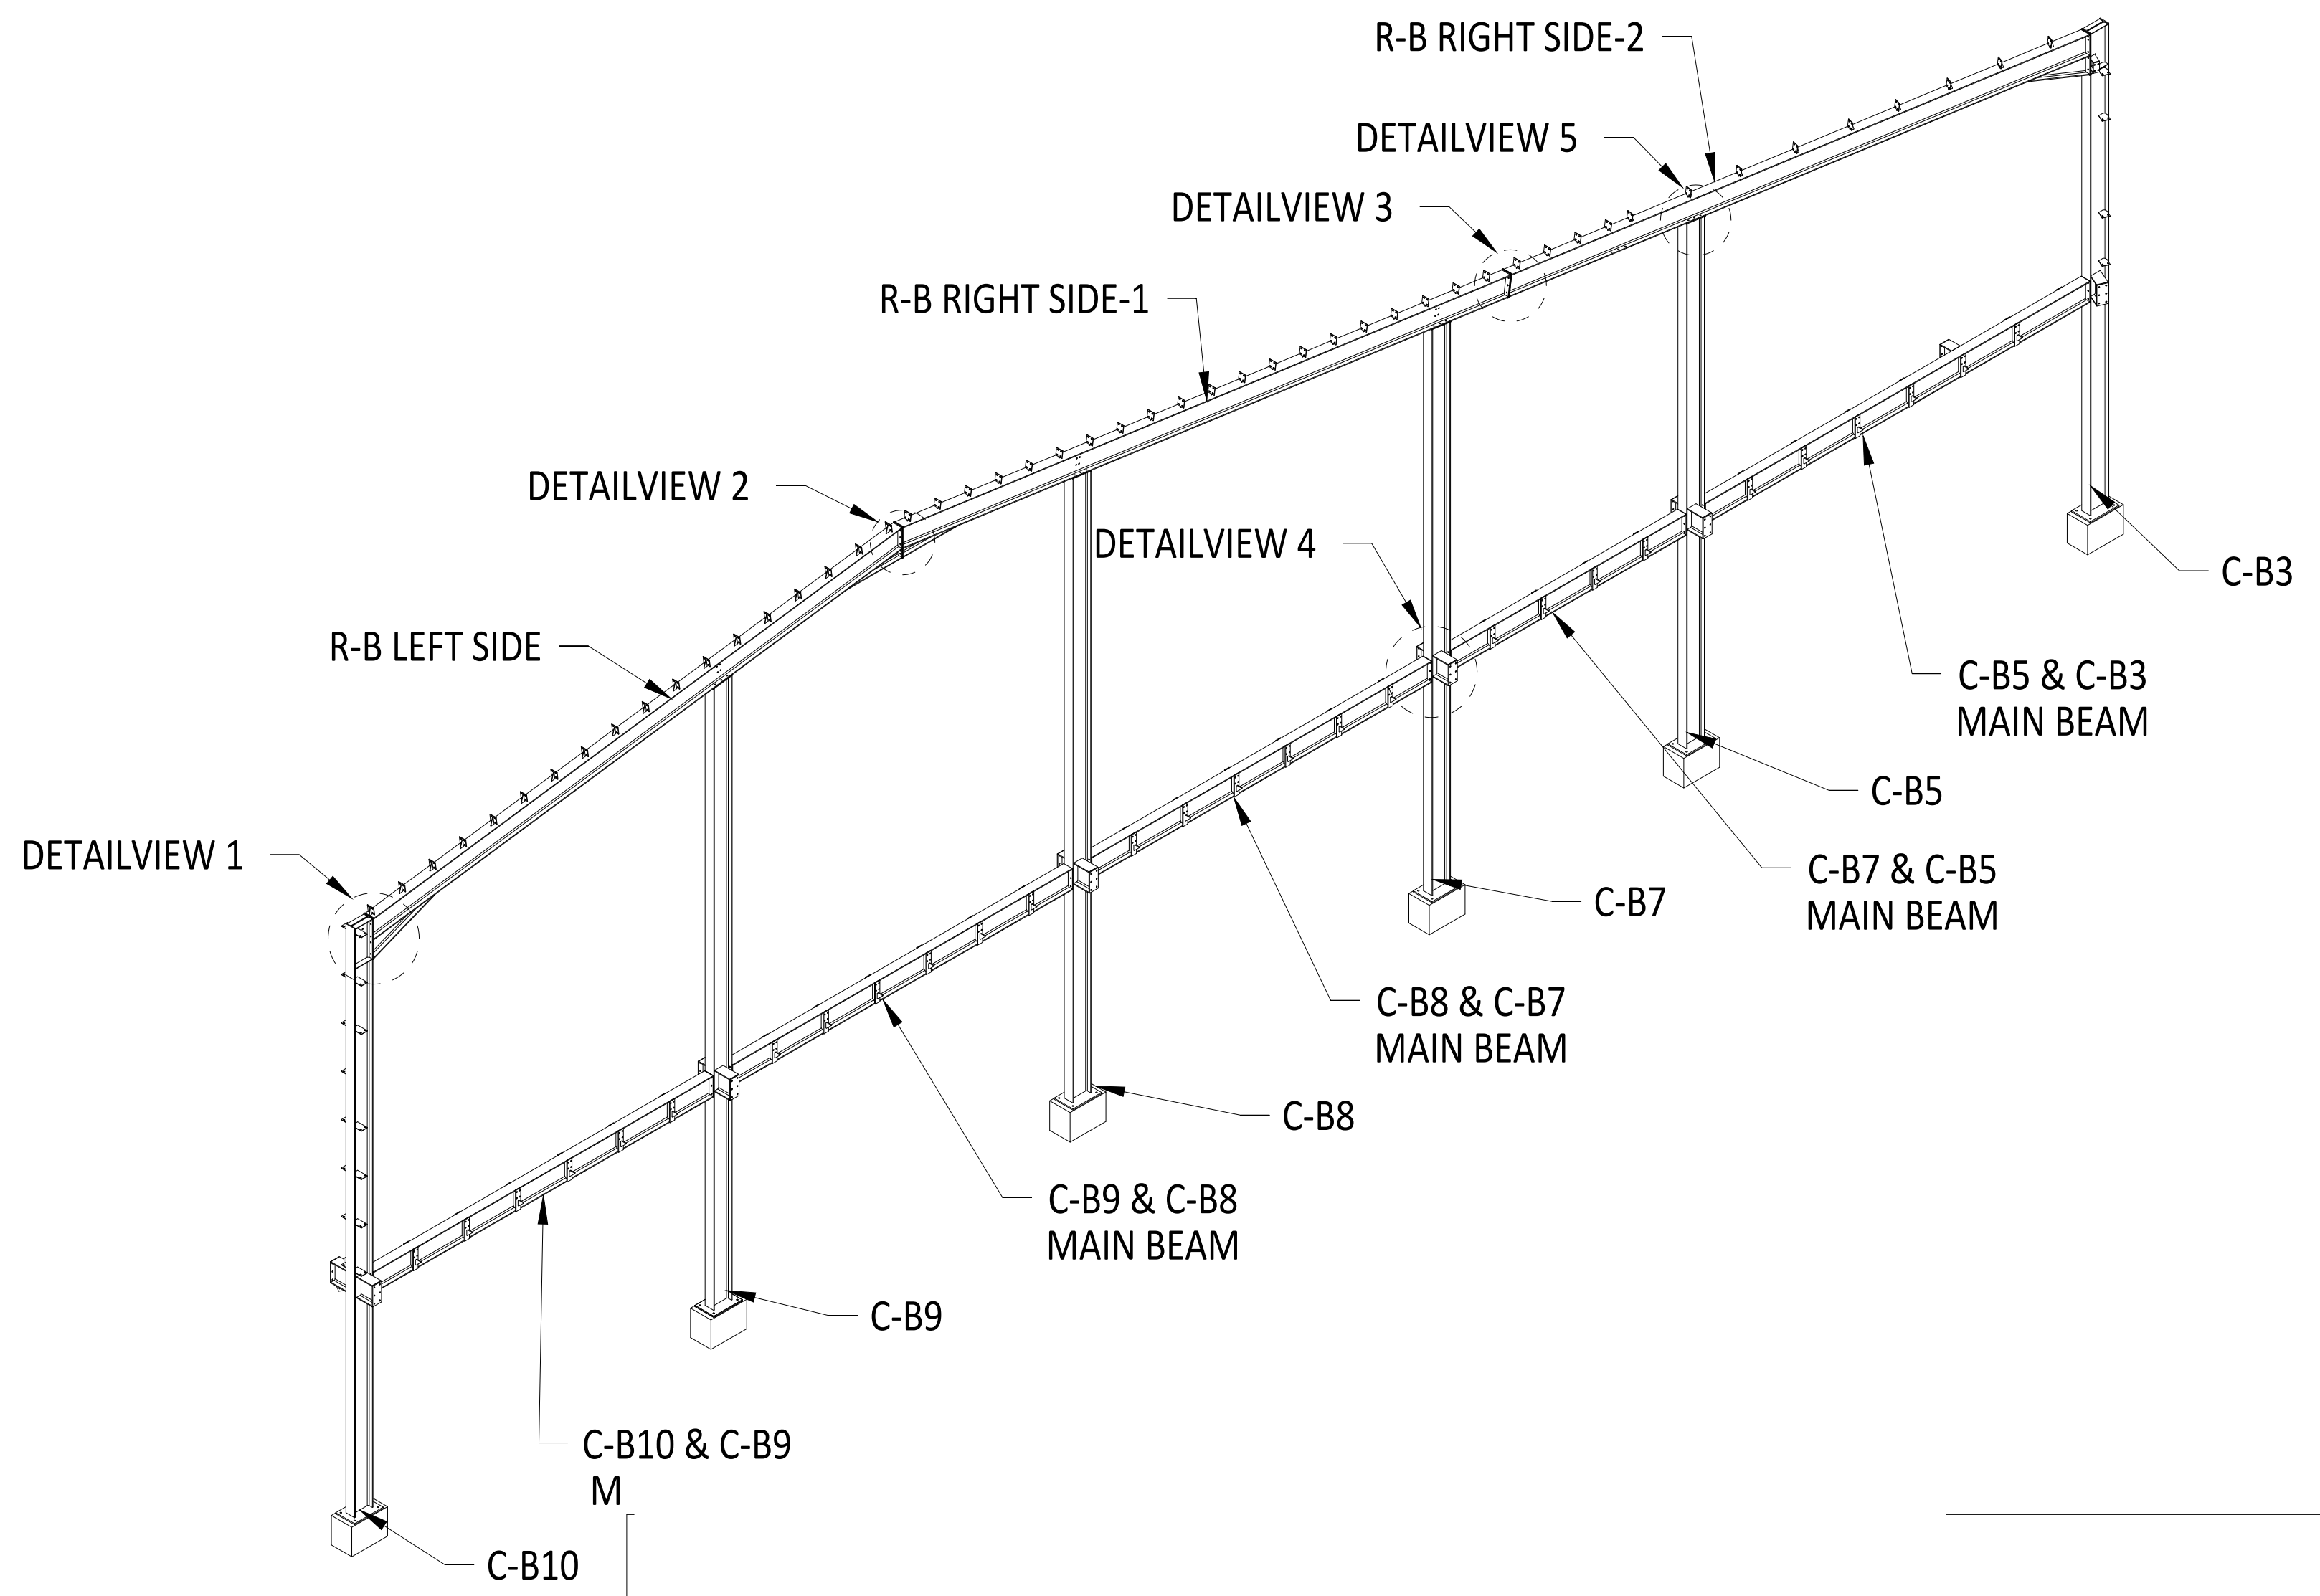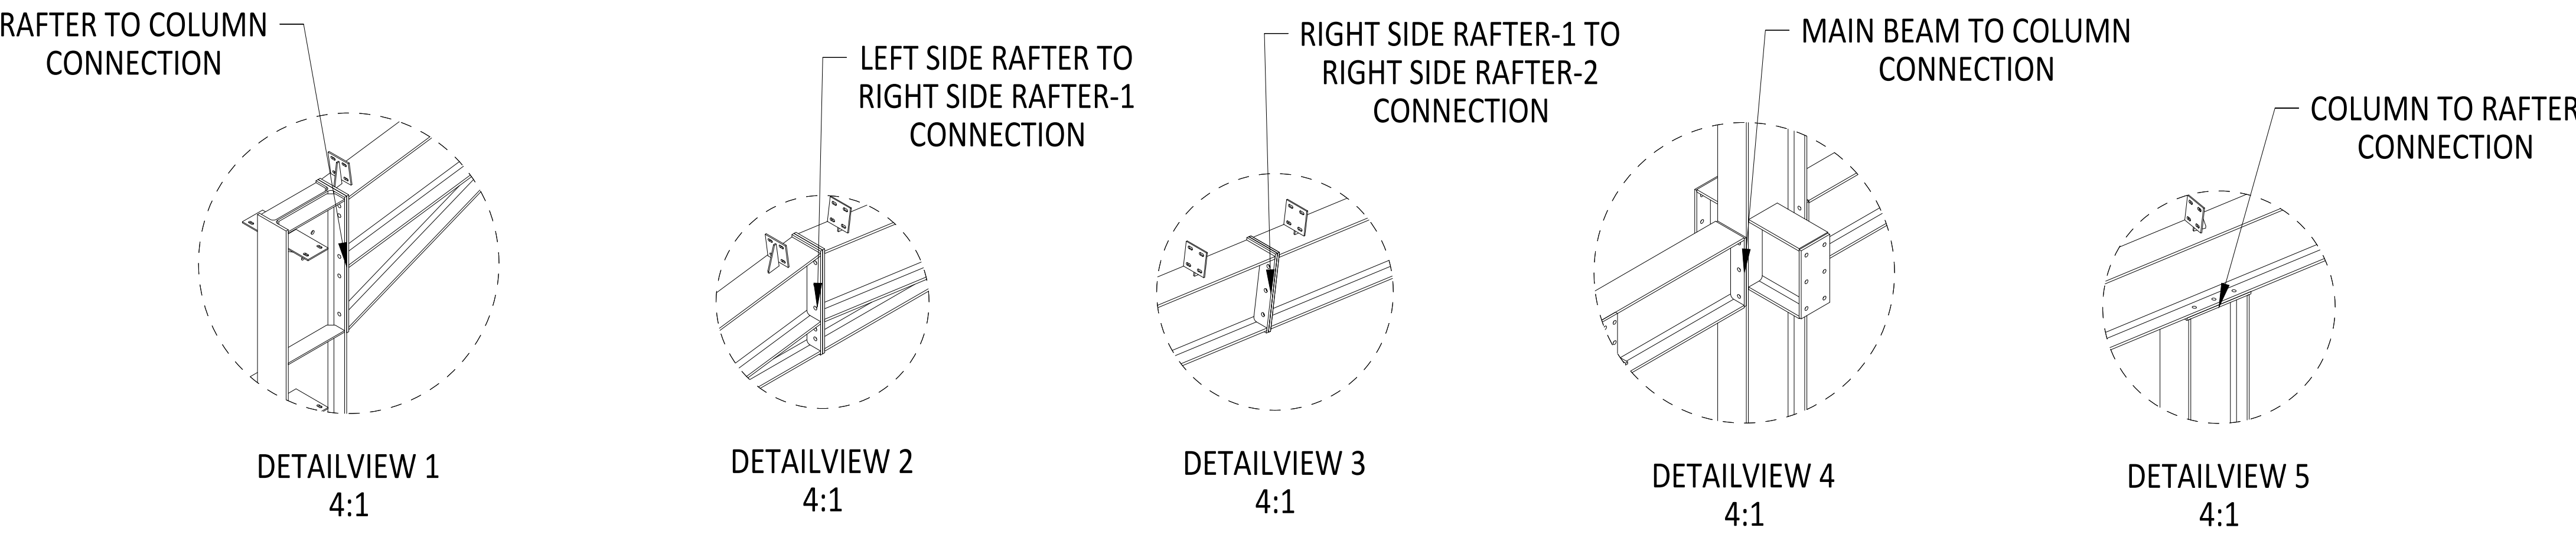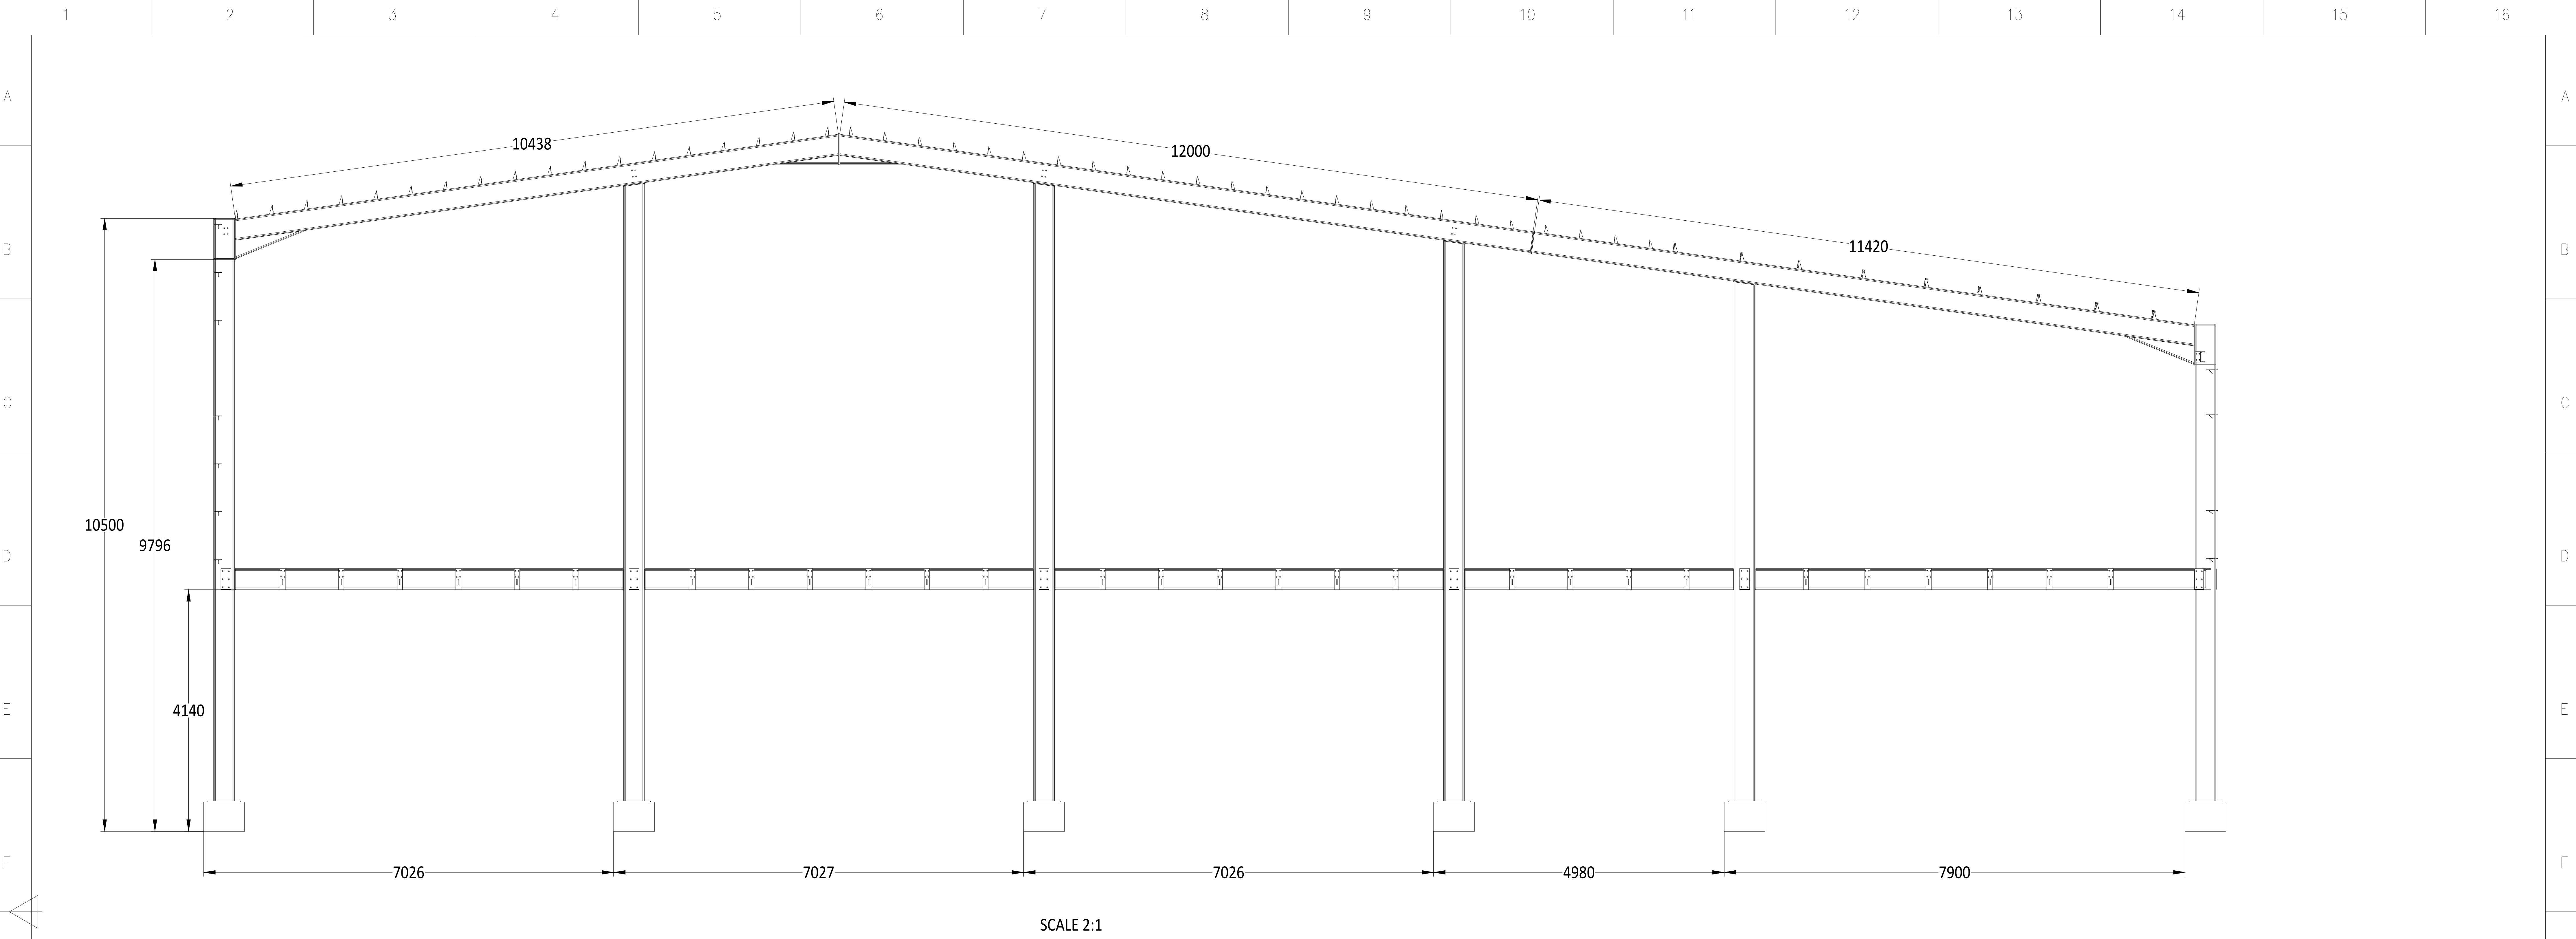


FRAME-B ERECTION DETAILS

ASSEMBLY NO.		TITLE			
PART NO.		HANGER FRAME B ERECTION DETAILS			
DESIGNER		SIZE	DWG NO	REV	
APPROVED		A0		00	
SCALE AS SHOWN		RELEASE DATE		WEIGHT Kg.	QTY.
		21/08/2025			



ASSEMBLY NO.		TITLE HANGER FRAME B & C ERECTION DETAILS				
PART NO.						
			SIZE A0	DWG NO		REV 00
DESIGNER			RELEASE DATE		WEIGHT Kg.	QTY.
APPROVED		SCALE AS SHOWN	21/08/2025			

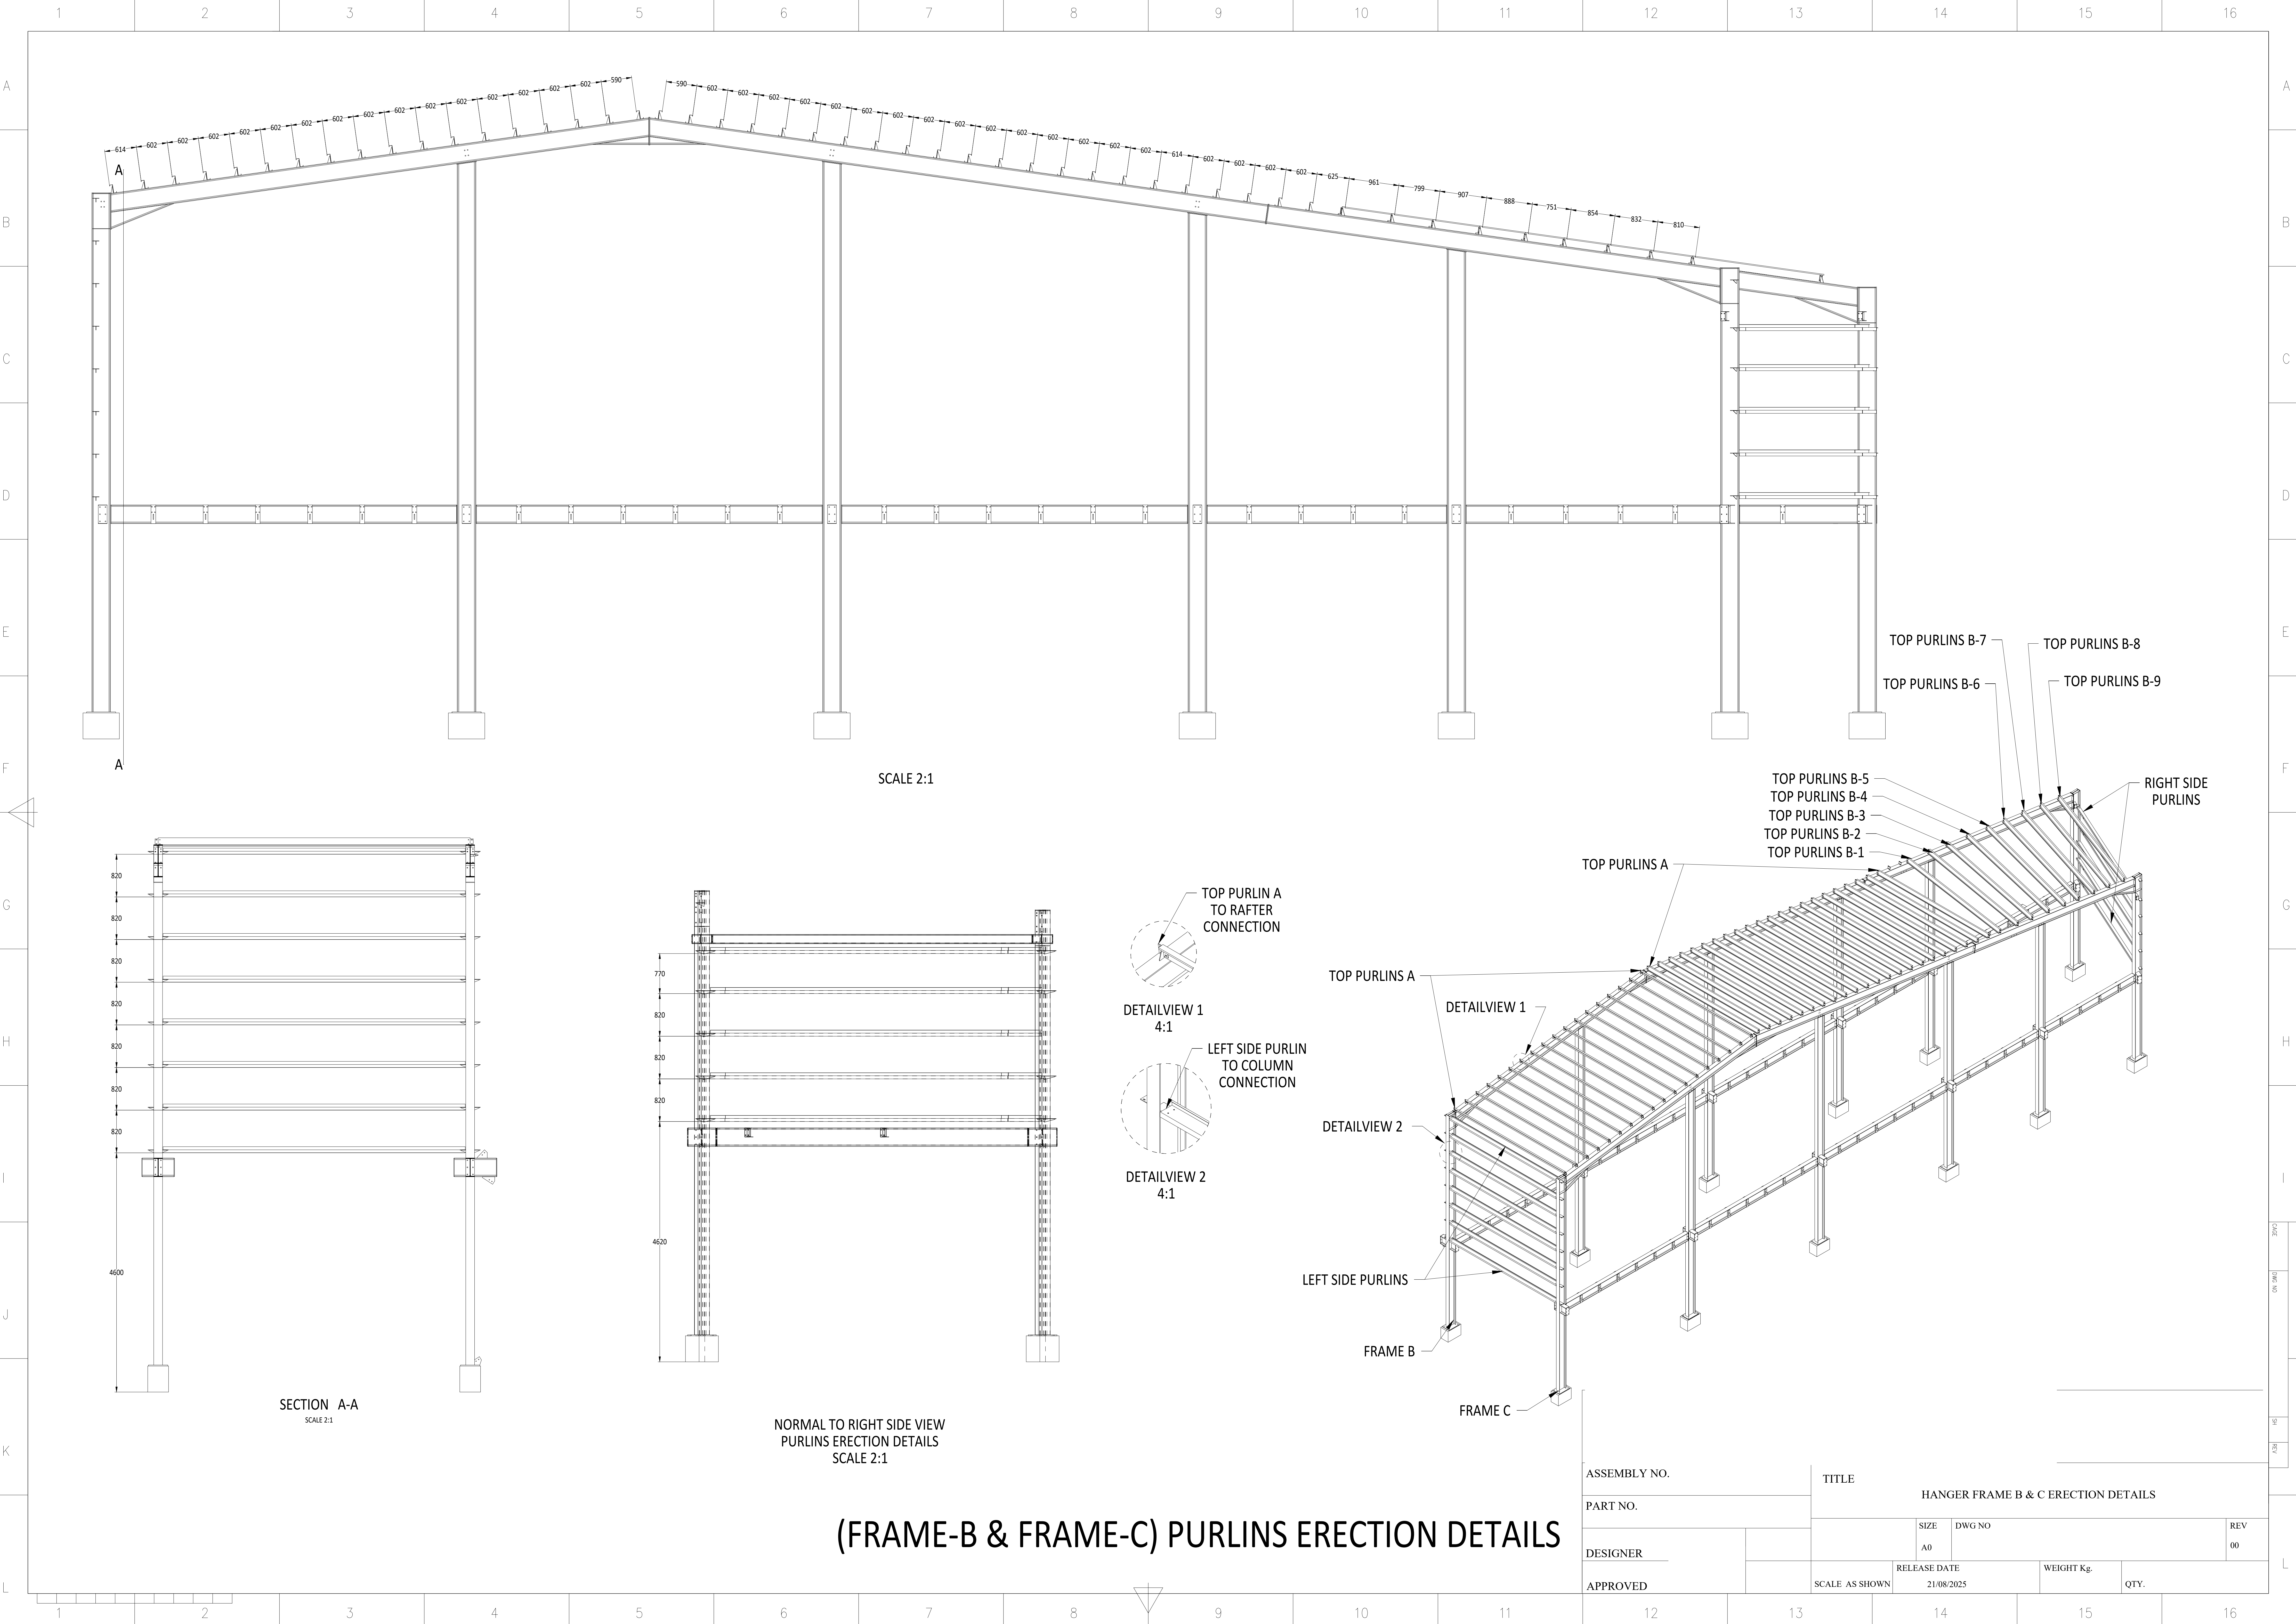



SECTION A-A
SCALE 2:1

NORMAL TO RIGHT SIDE VIEW
PURLINS ERECTION DETAILS
SCALE 2:1

(FRAME-B & FRAME-C) PURLINS ERECTION DETAILS

ASSEMBLY NO.		TITLE			
PART NO.		HANGER FRAME B & C ERECTION DETAILS			
DESIGNER		SIZE A0	DWG NO	REV 00	
APPROVED		SCALE AS SHOWN	RELEASE DATE 21/08/2025	WEIGHT Kg.	QTY.

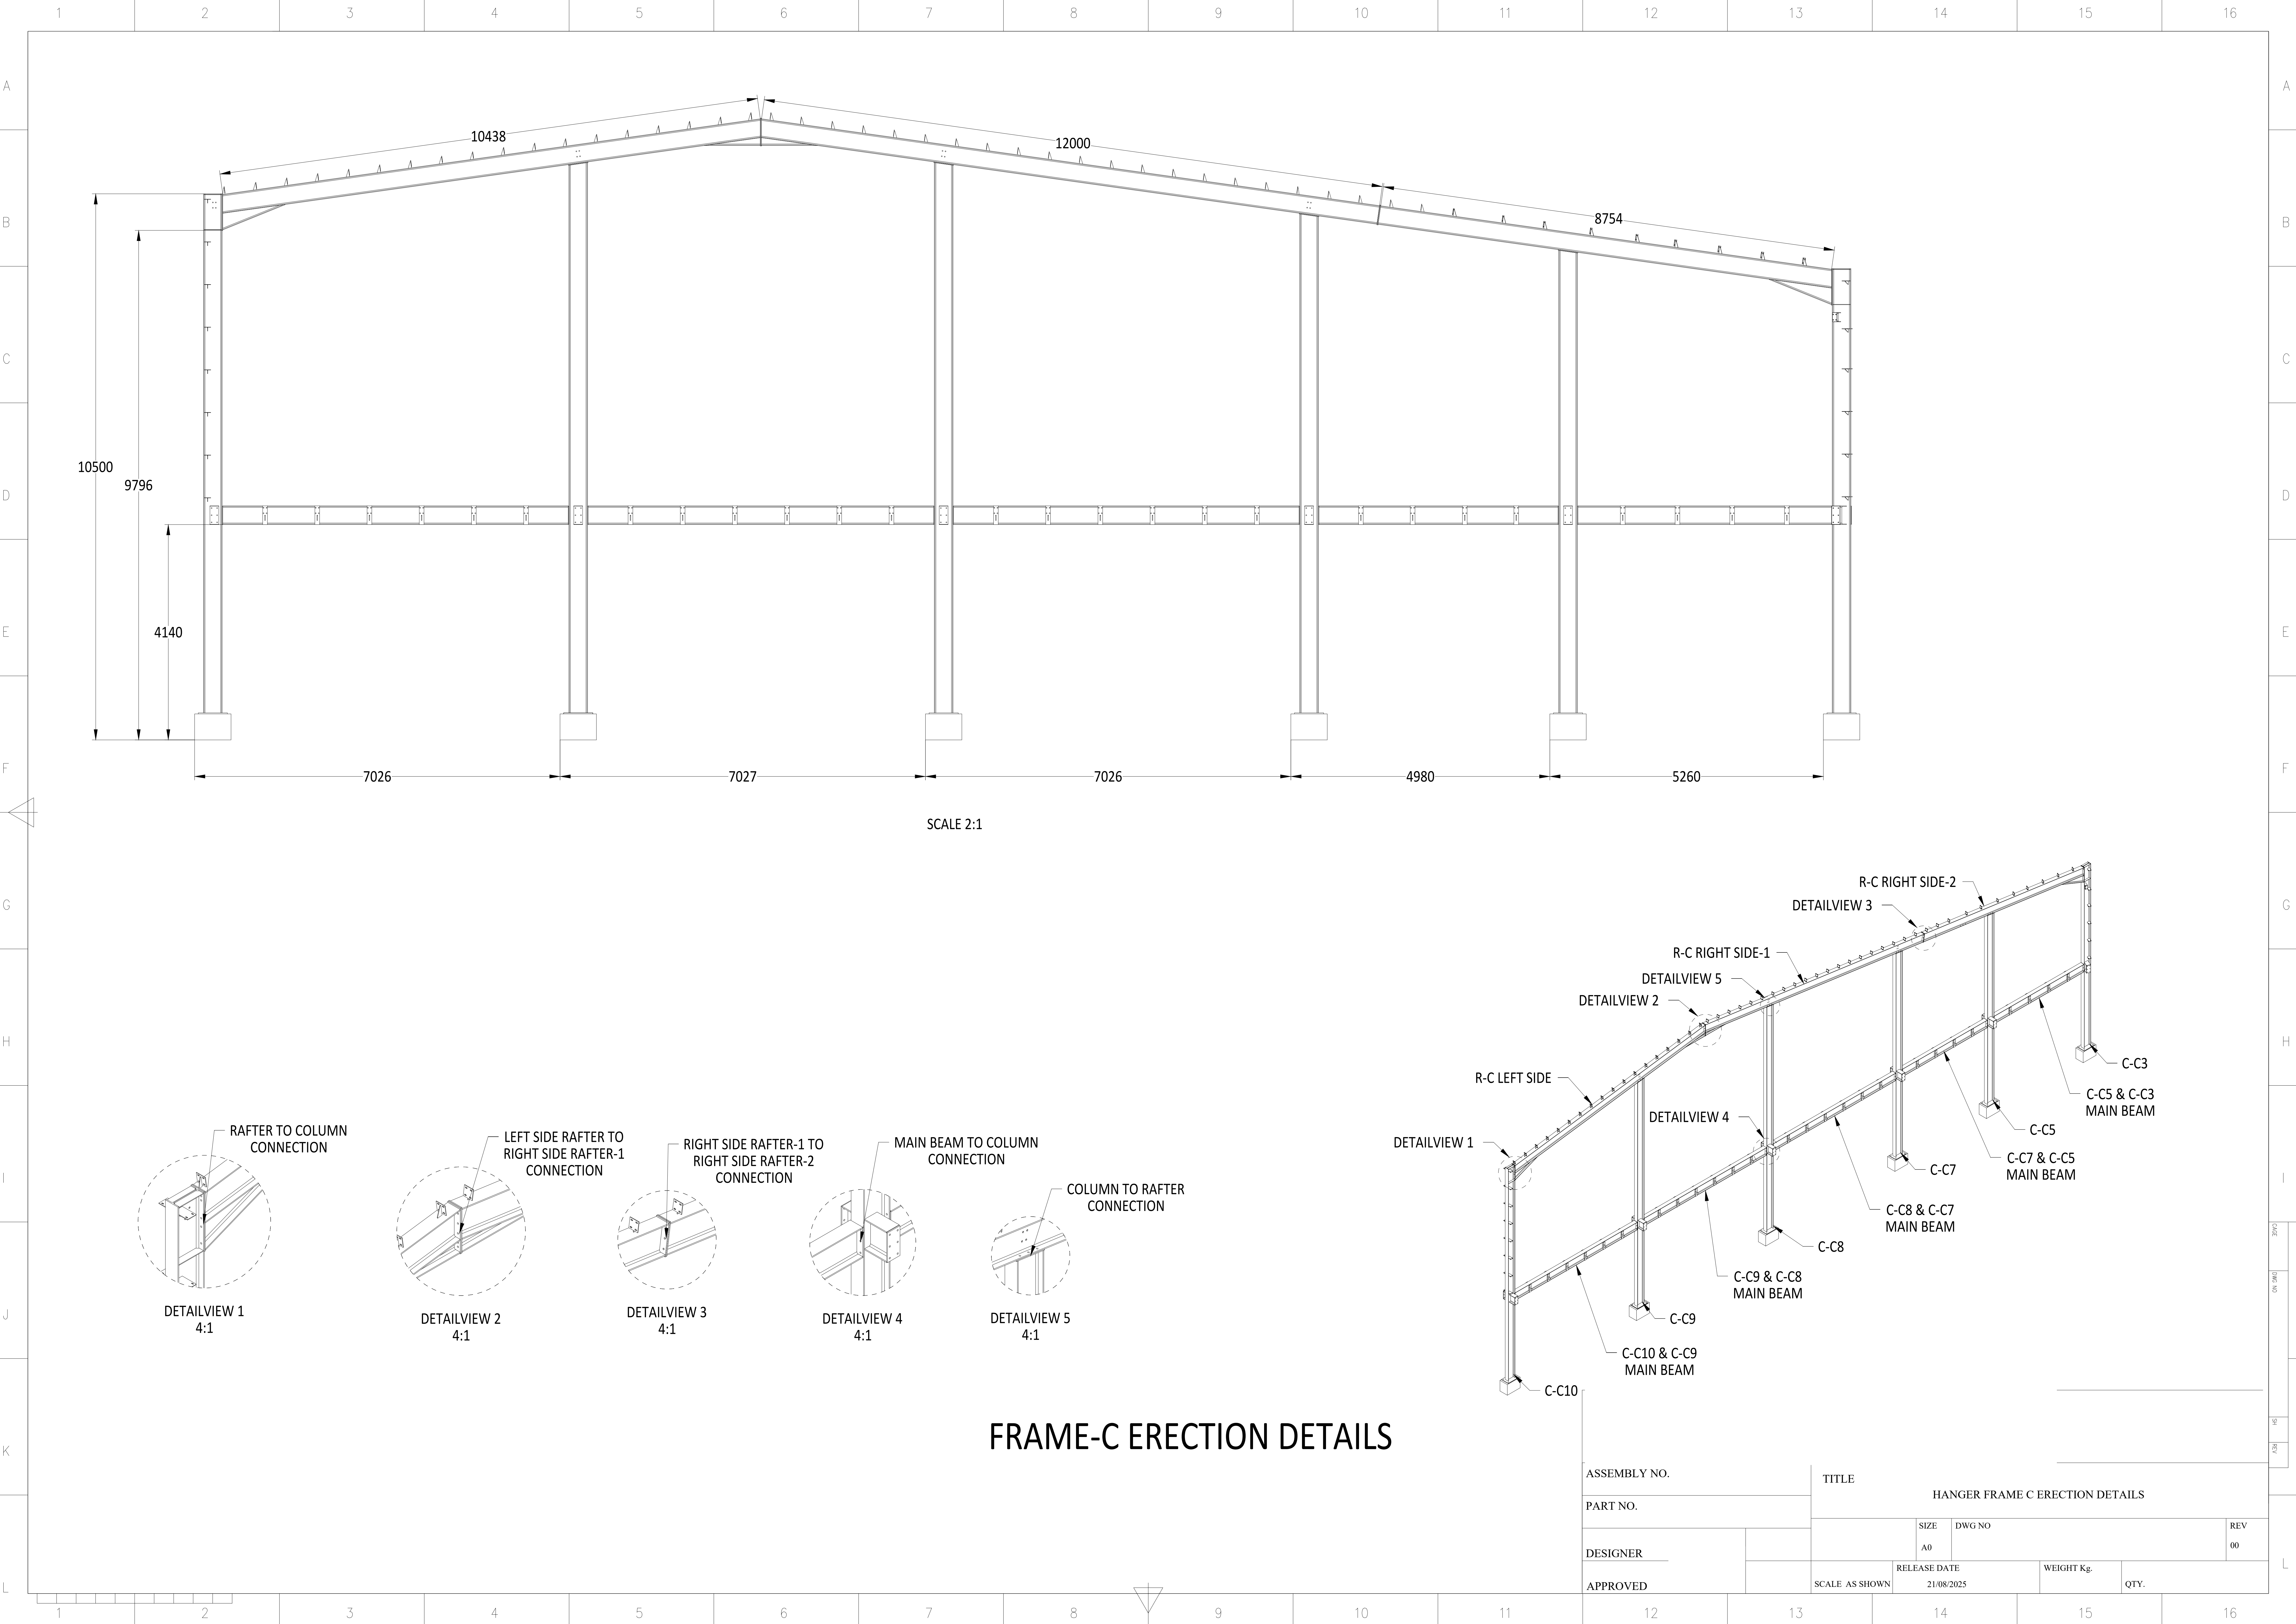

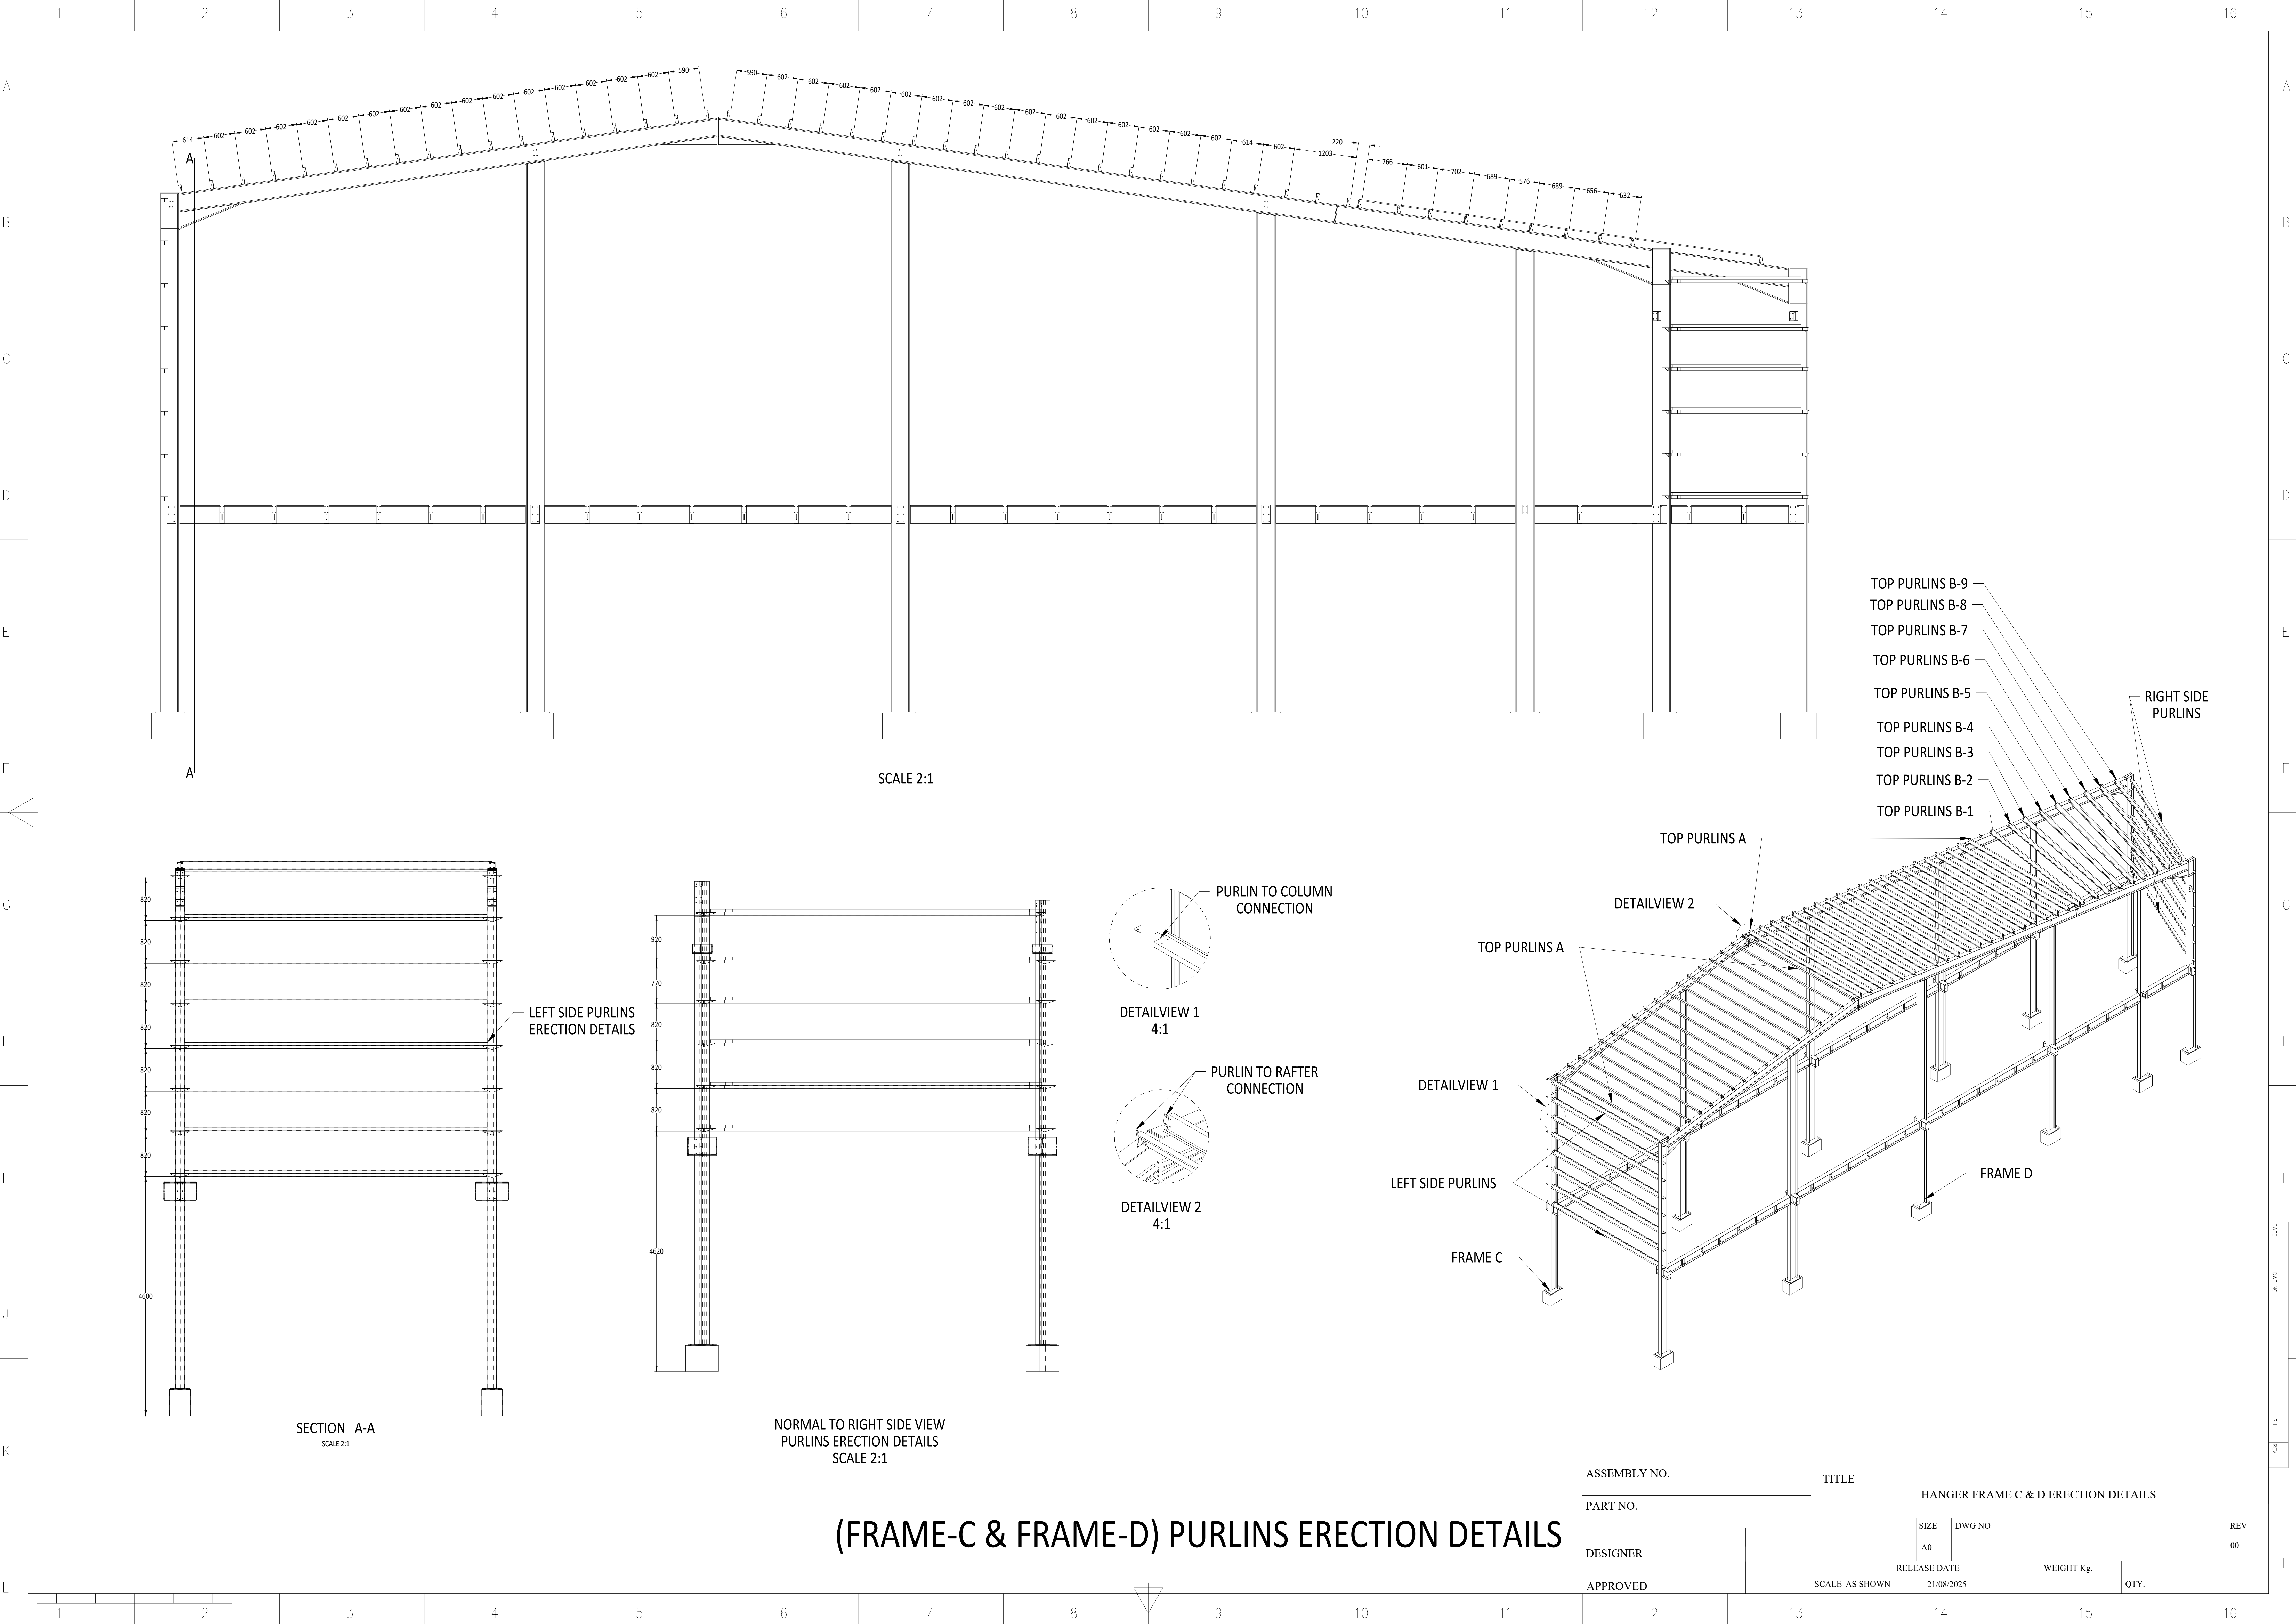

A

A

SCALE 2:1

SECTION A-A
SCALE 2:1

NORMAL TO RIGHT SIDE VIEW
PURLINS ERECTION DETAILS
SCALE 2:1


DETAILVIEW 1
4:1

DETAILVIEW 2
4:1

PURLIN TO COLUMN
CONNECTION


PURLIN TO RAFTER
CONNECTION

- TOP PURLINS B-9
- TOP PURLINS B-8
- TOP PURLINS B-7
- TOP PURLINS B-6
- TOP PURLINS B-5
- TOP PURLINS B-4
- TOP PURLINS B-3
- TOP PURLINS B-2
- TOP PURLINS B-1
- RIGHT SIDE PURLINS

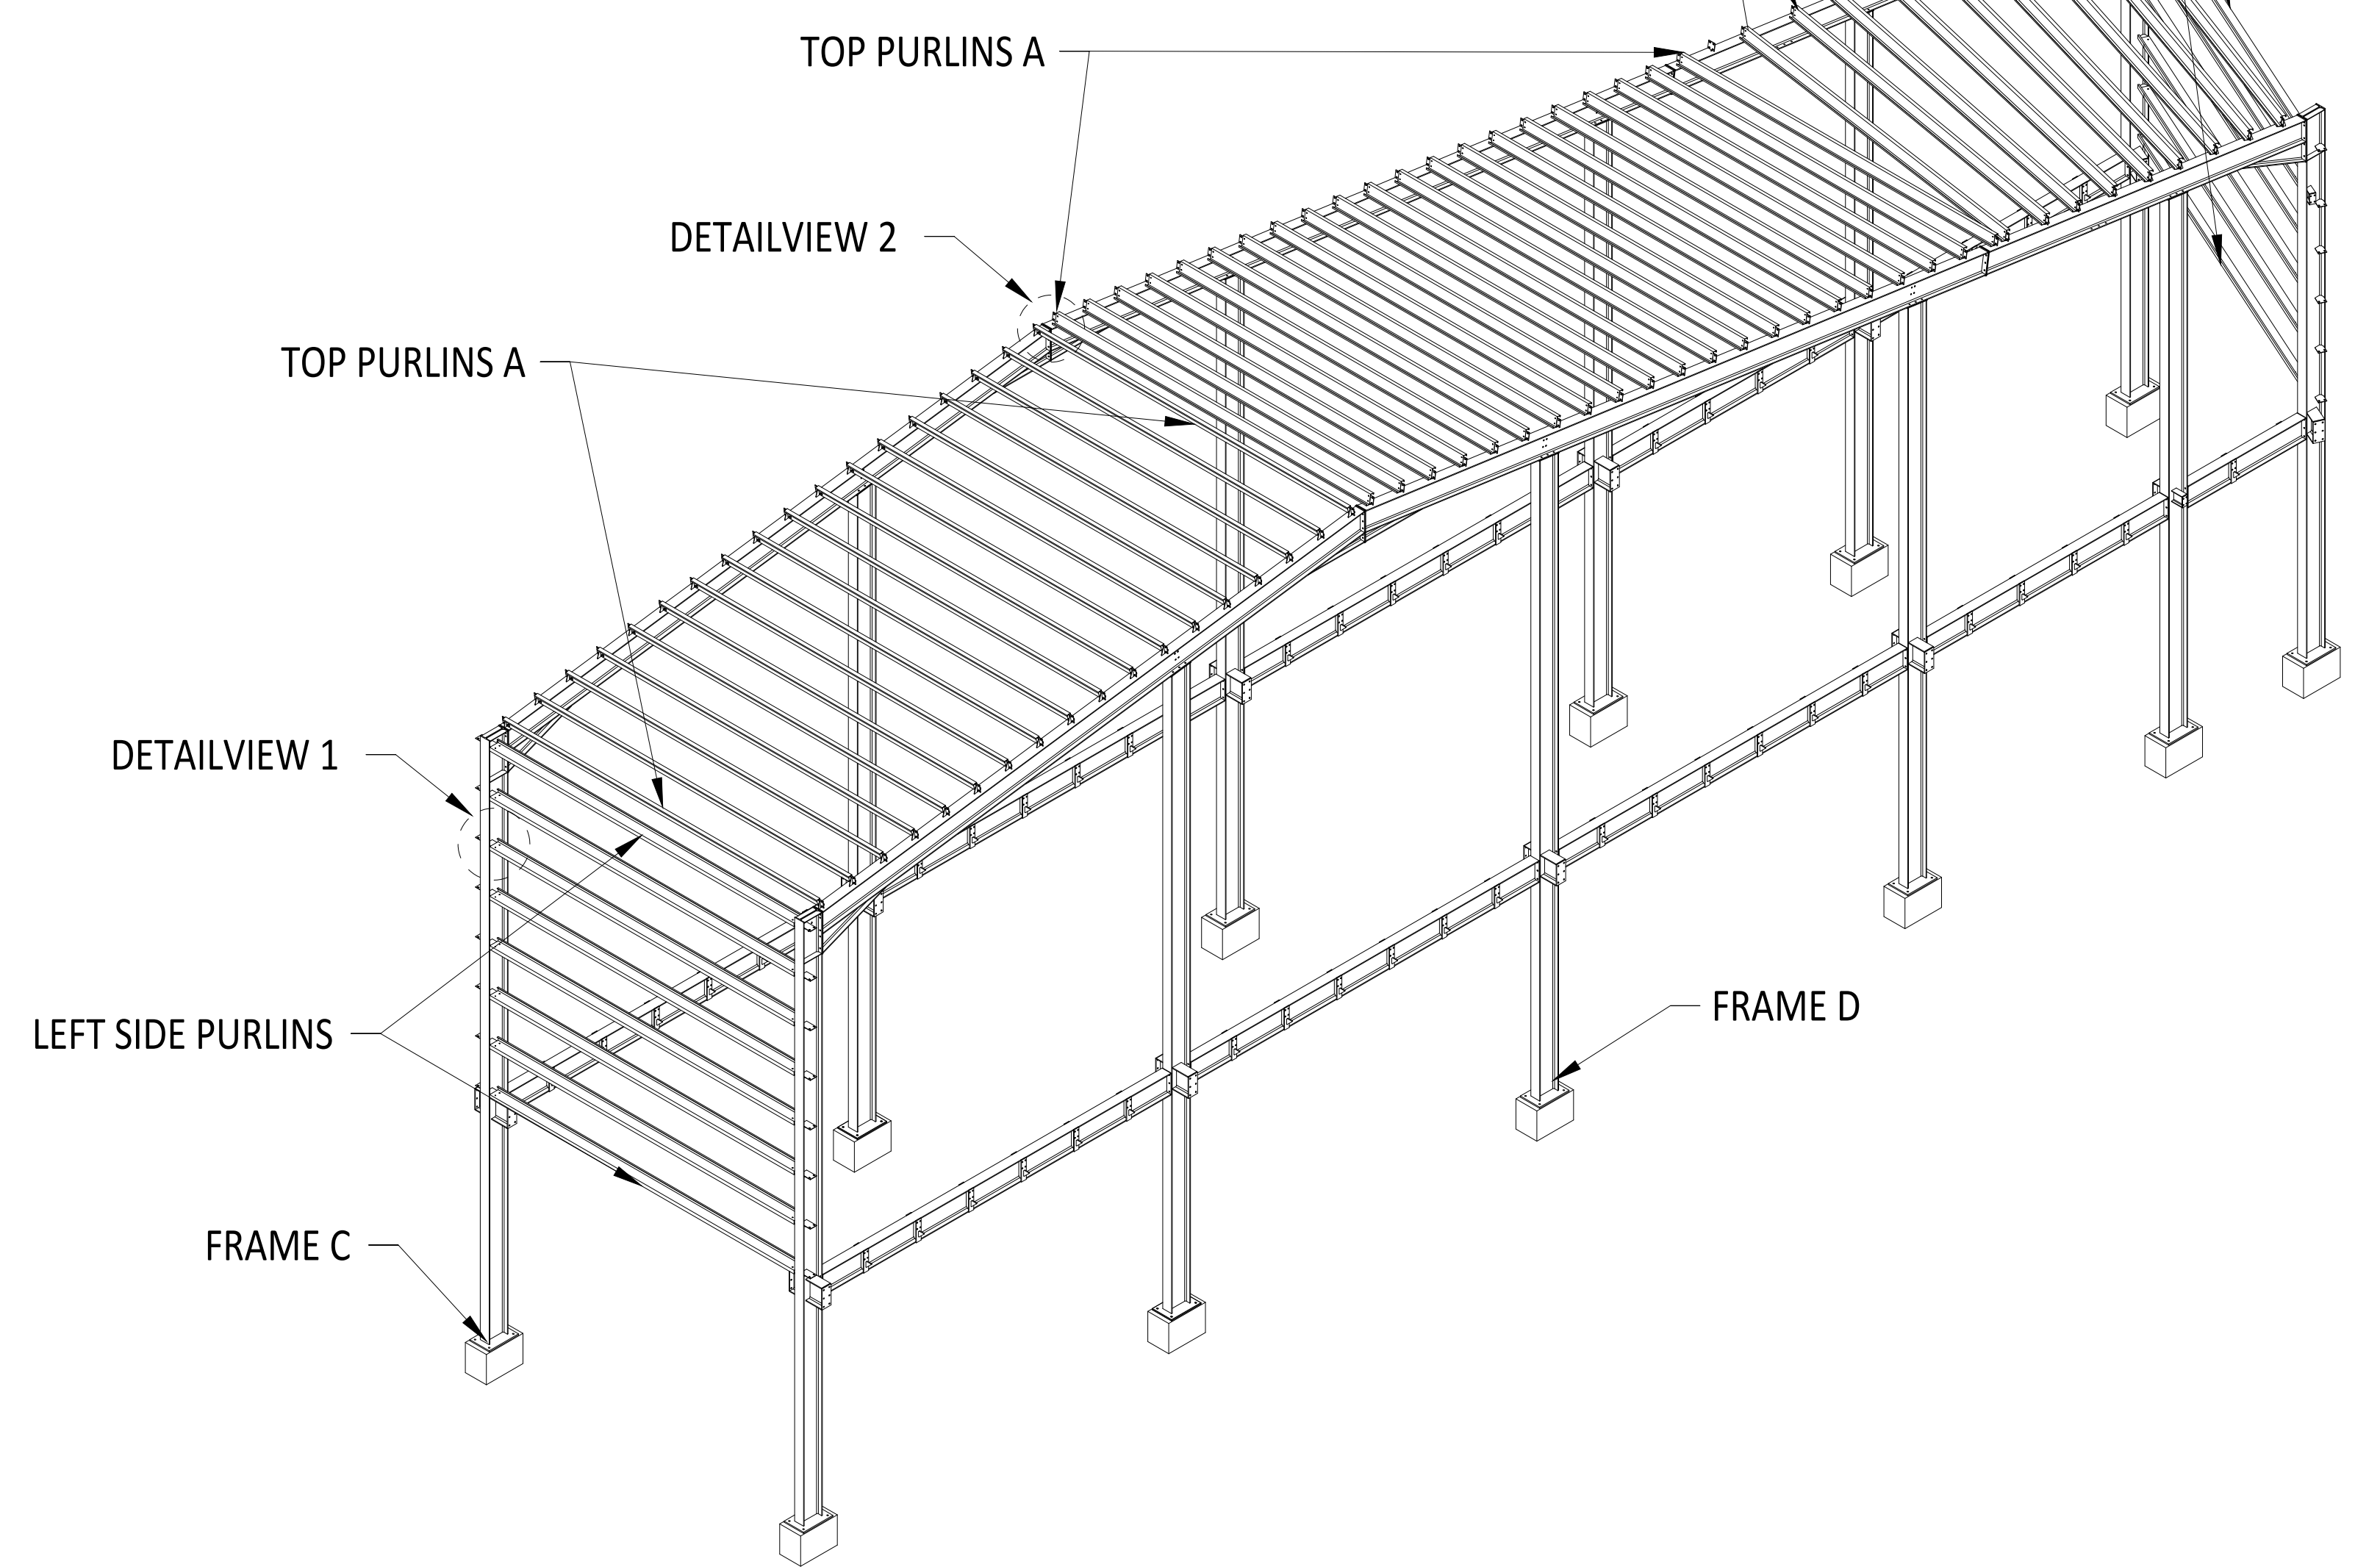


ASSEMBLY NO.		TITLE			
PART NO.		HANGER FRAME C & D ERECTION DETAILS			
DESIGNER		SIZE	DWG NO	REV	
APPROVED		A0		00	
		RELEASE DATE	WEIGHT Kg.	QTY.	
		21/08/2025			
		SCALE AS SHOWN			

(FRAME-C & FRAME-D) PURLINS ERECTION DETAILS


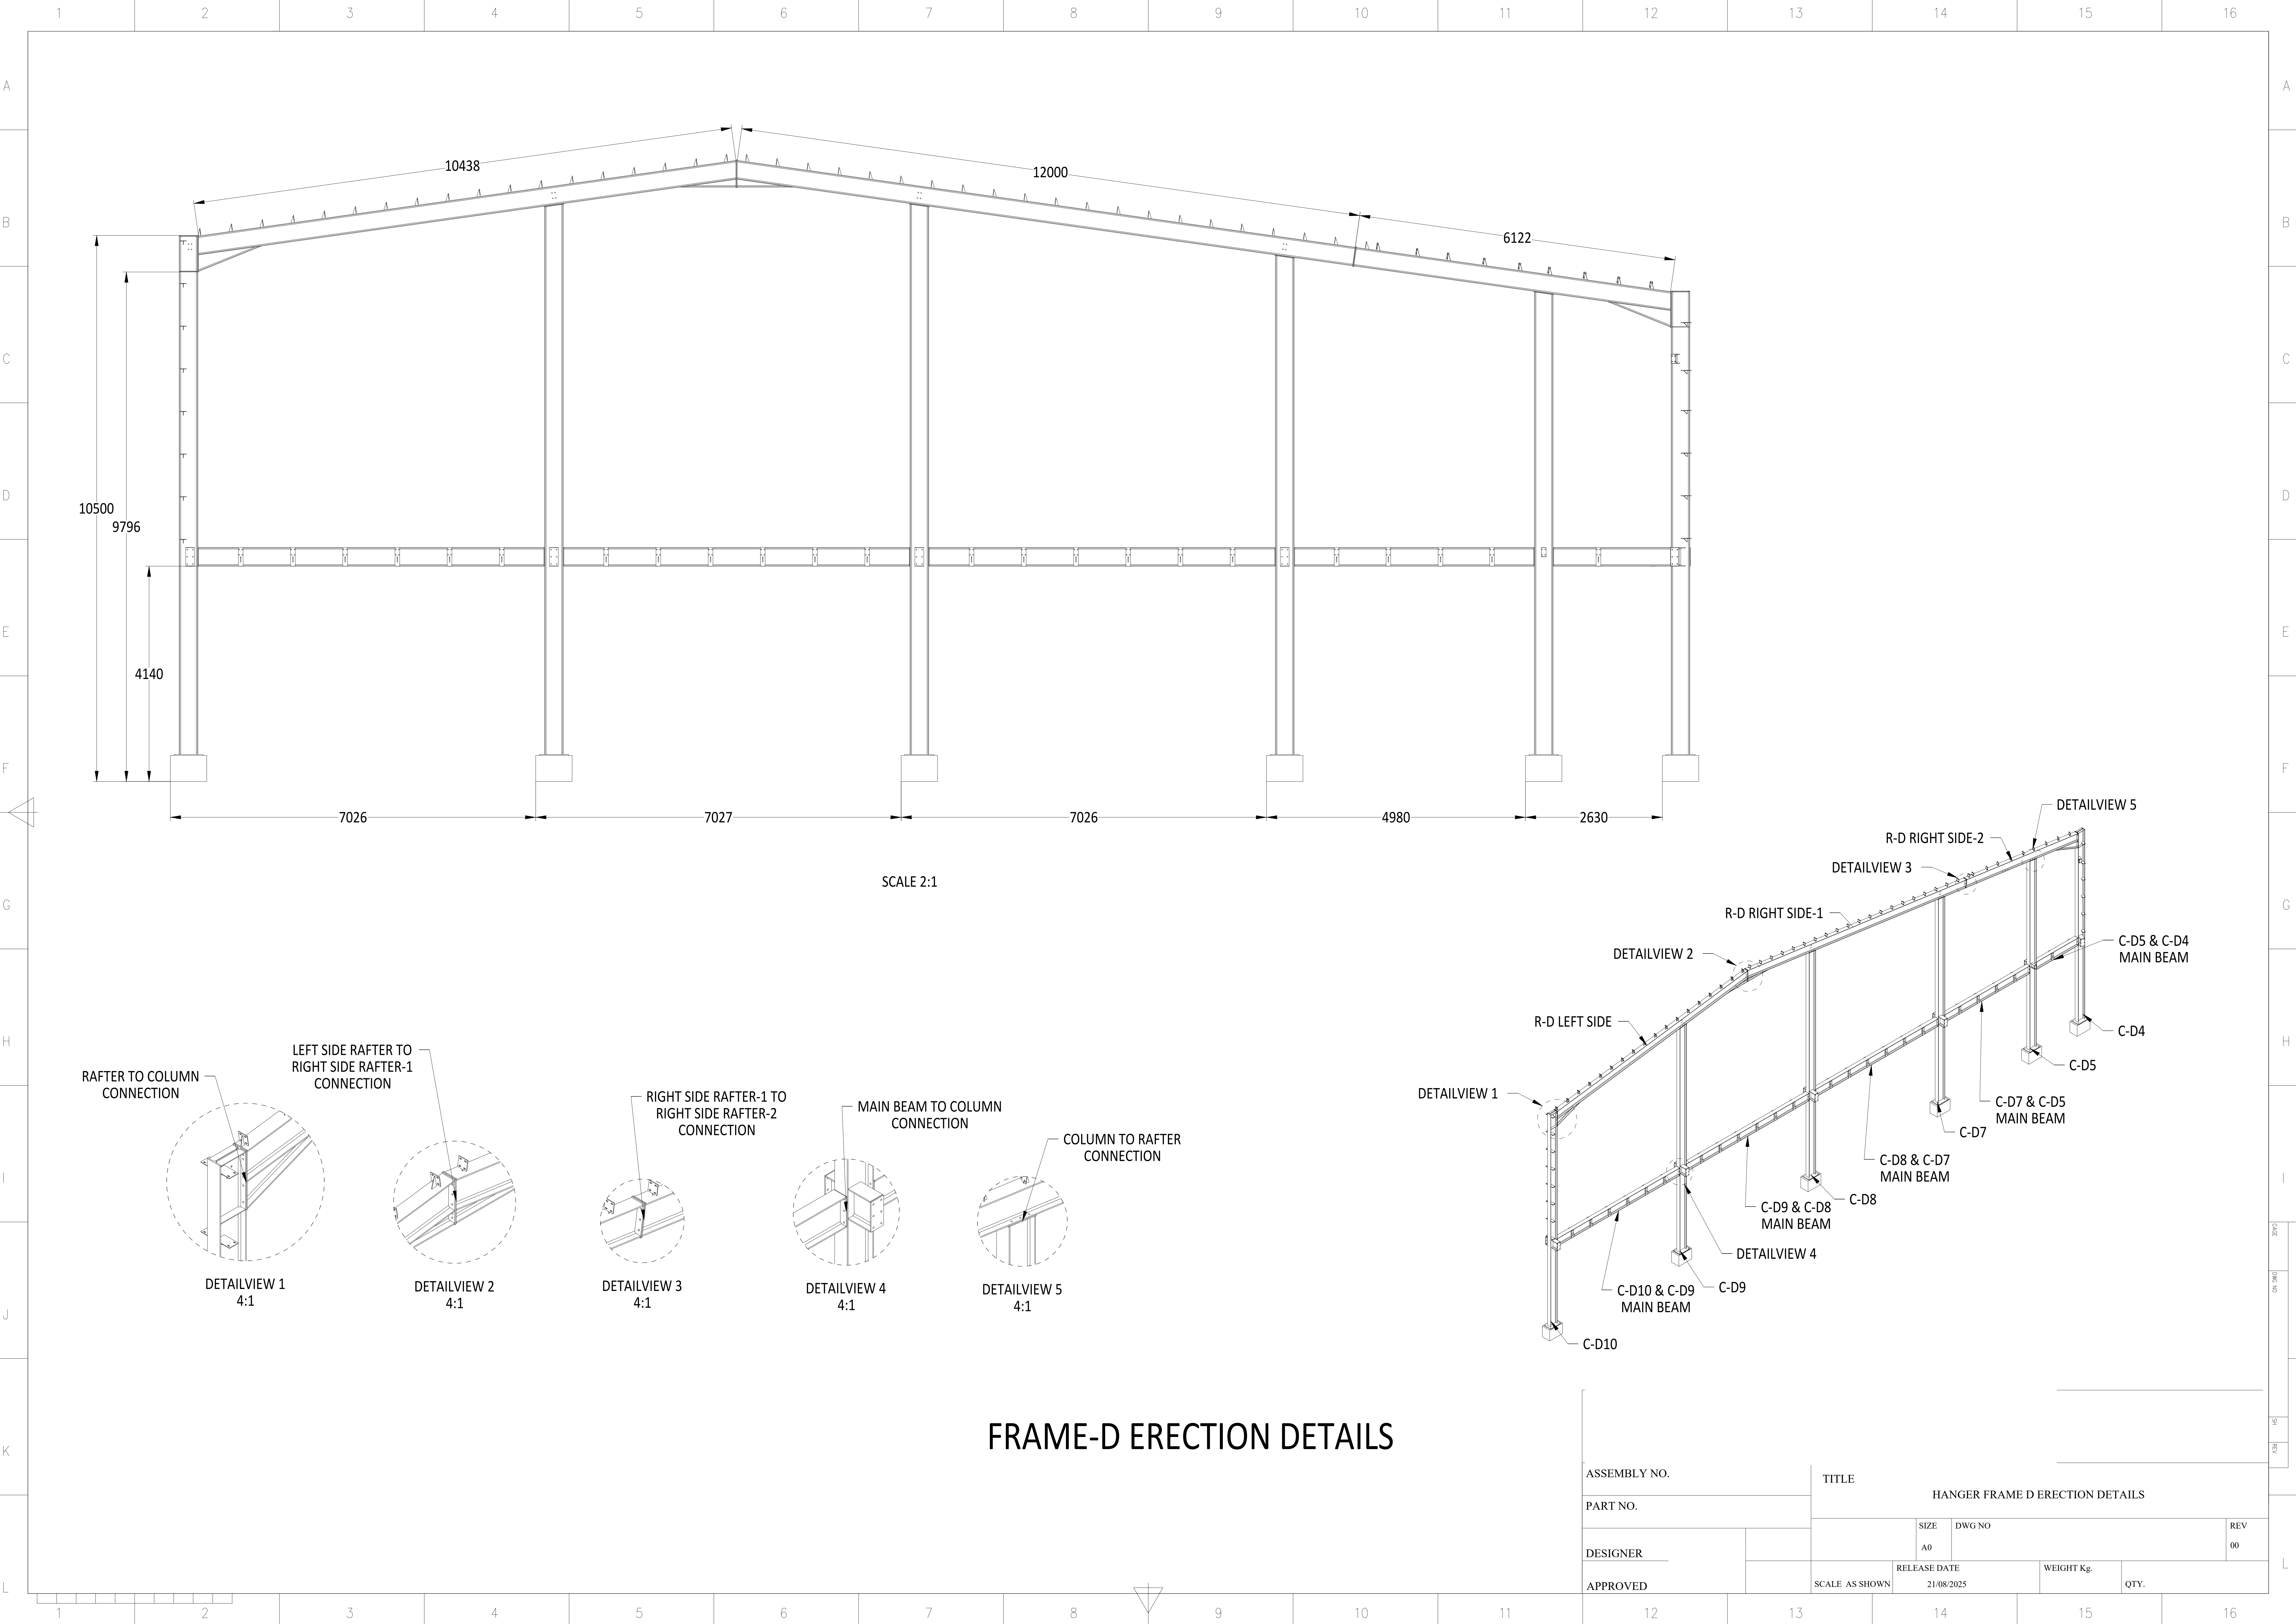


FRAME-D ERECTION DETAILS


ASSEMBLY NO.		TITLE			
PART NO.		HANGER FRAME D ERECTION DETAILS			
DESIGNER		SIZE	DWG NO	REV	
APPROVED		A0		00	
		RELEASE DATE	WEIGHT Kg.	QTY.	
		21/08/2025			

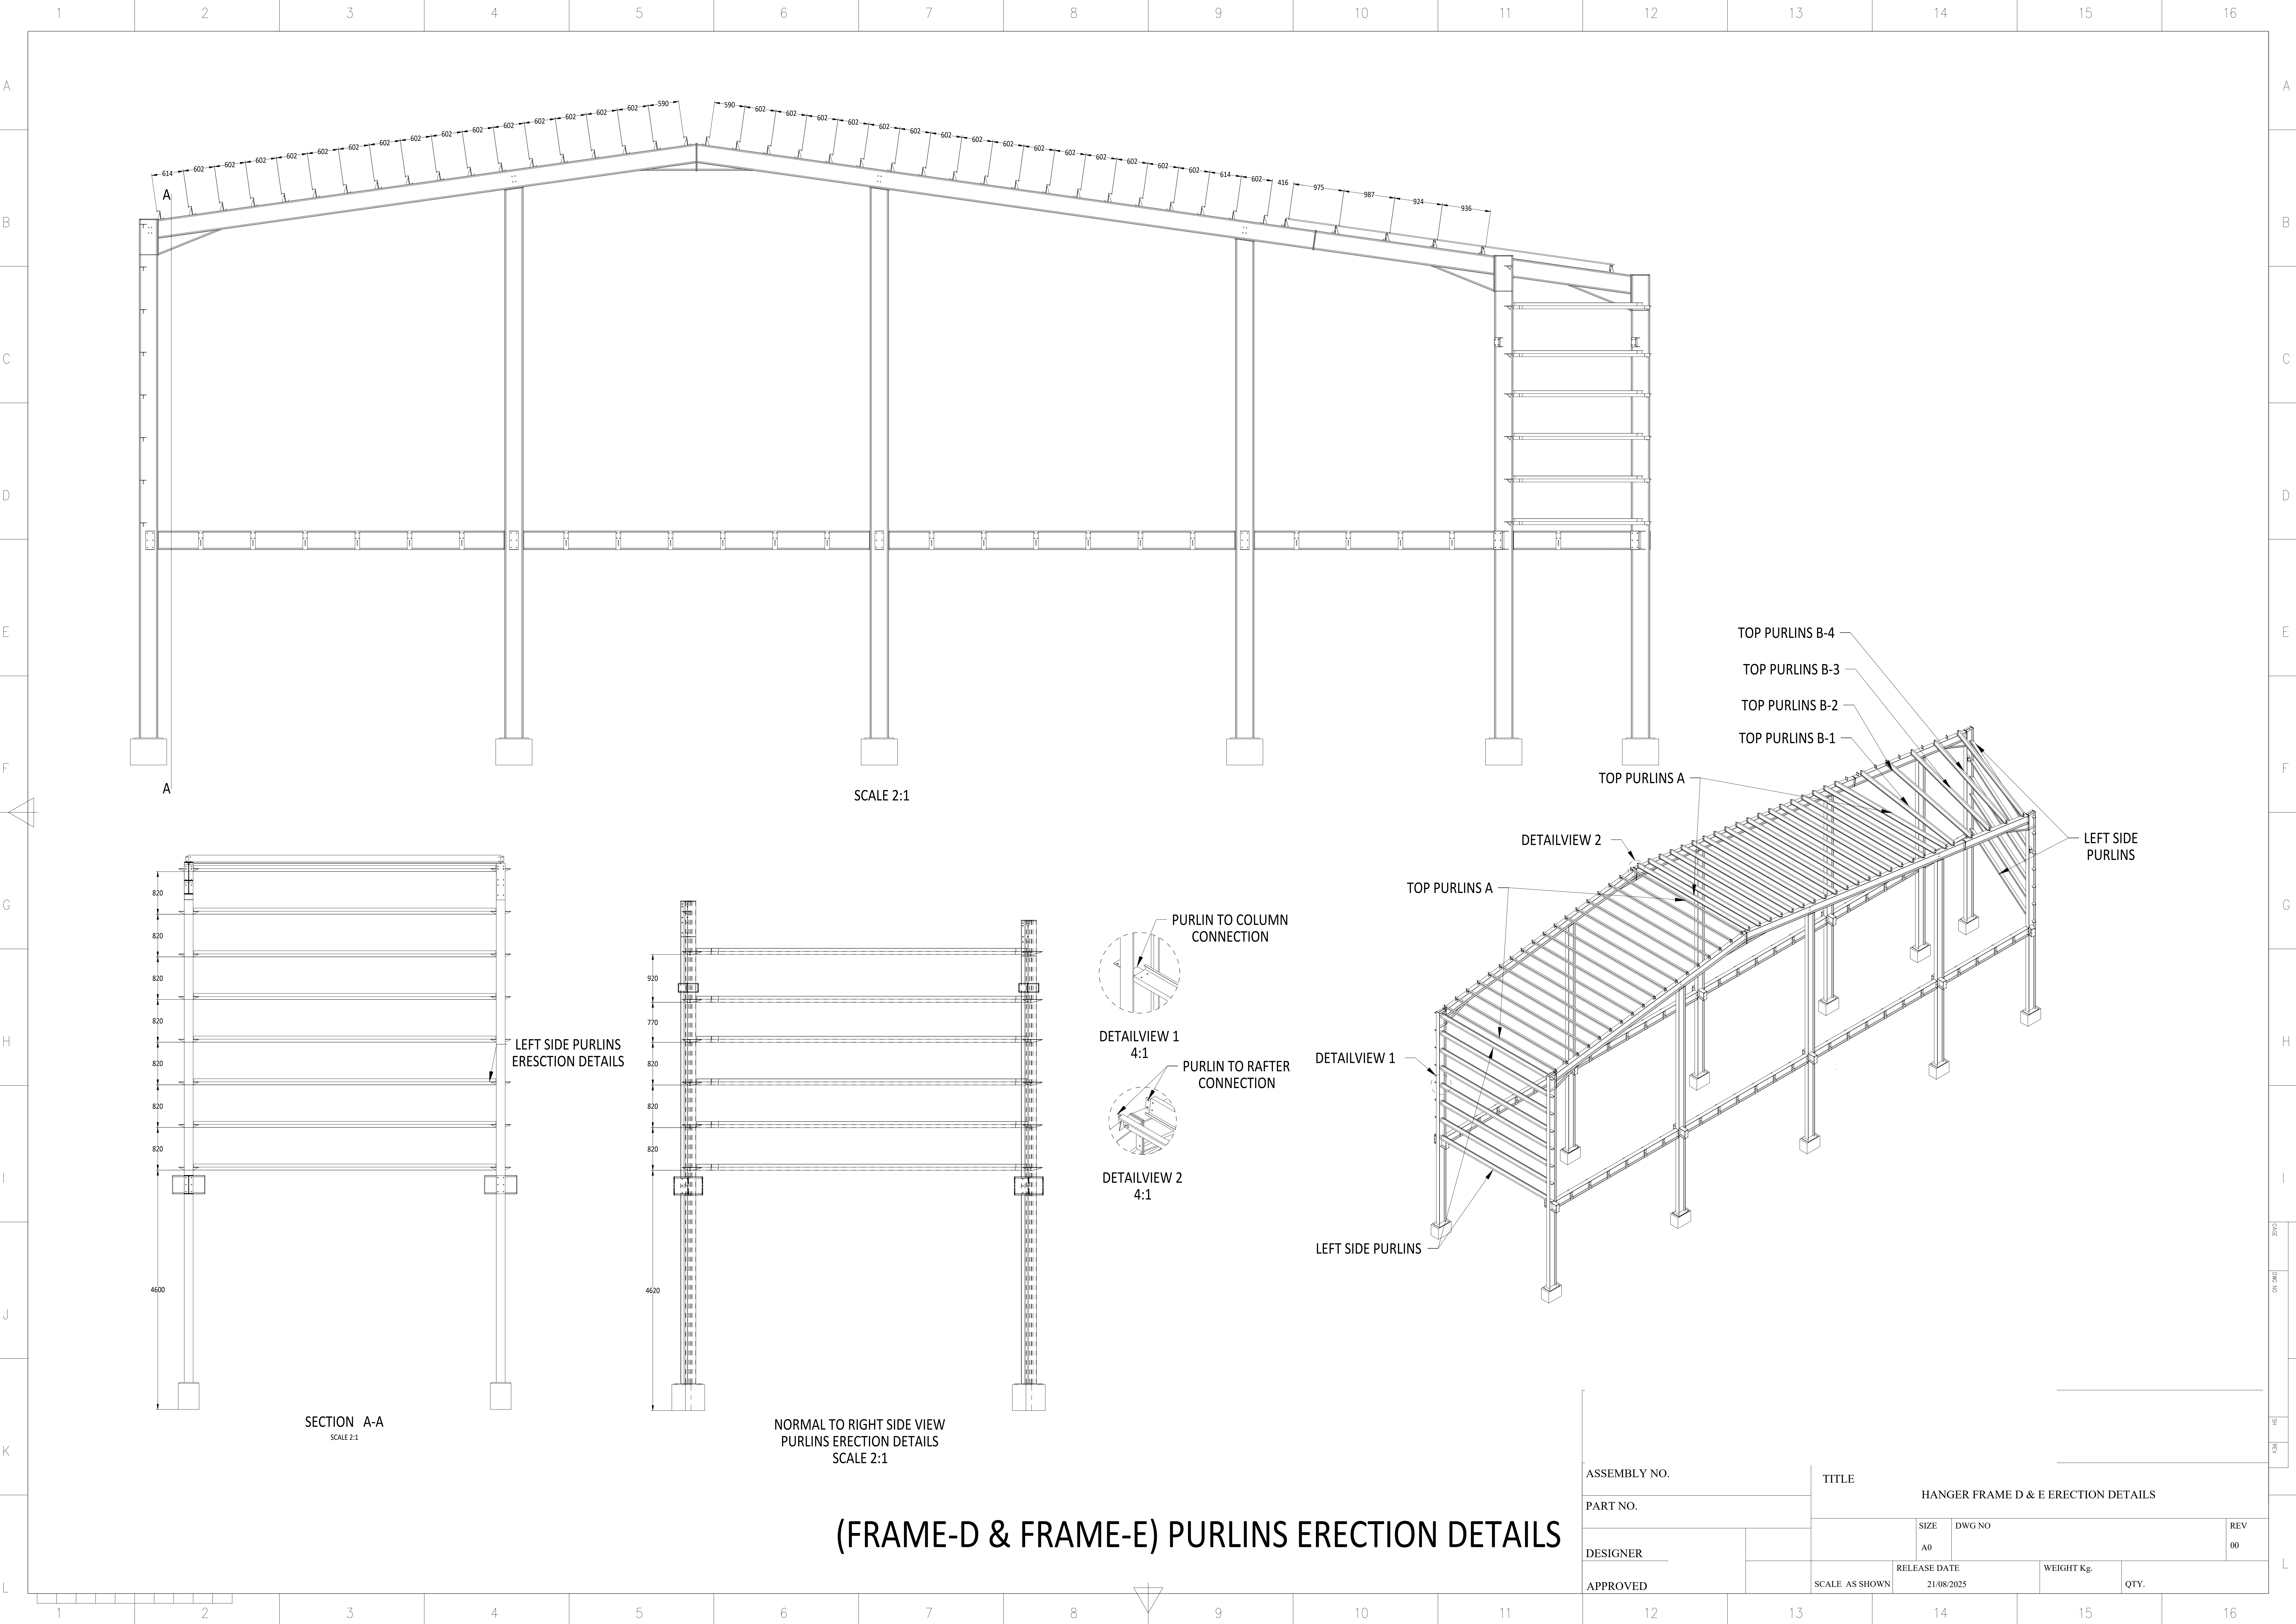


ASSEMBLY NO.		TITLE			
PART NO.		HANGER FRAME D & E ERECTION DETAILS			
DESIGNER		SIZE	DWG NO	REV	
APPROVED		A0		00	
		RELEASE DATE	WEIGHT Kg.	QTY.	
SCALE AS SHOWN		21/08/2025			

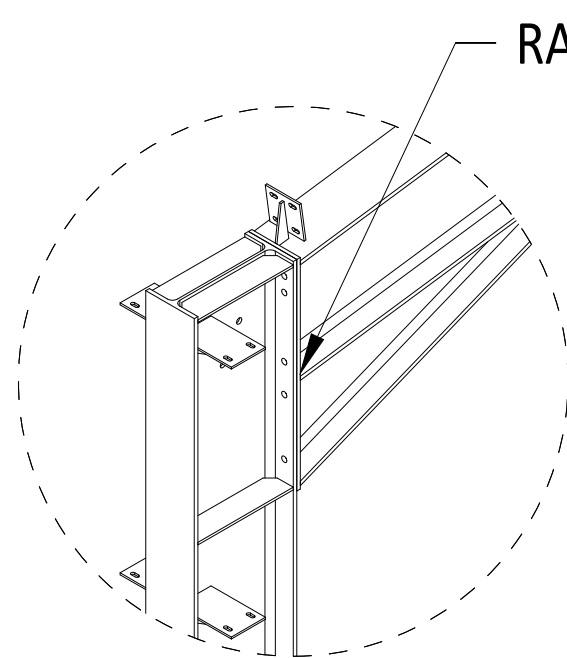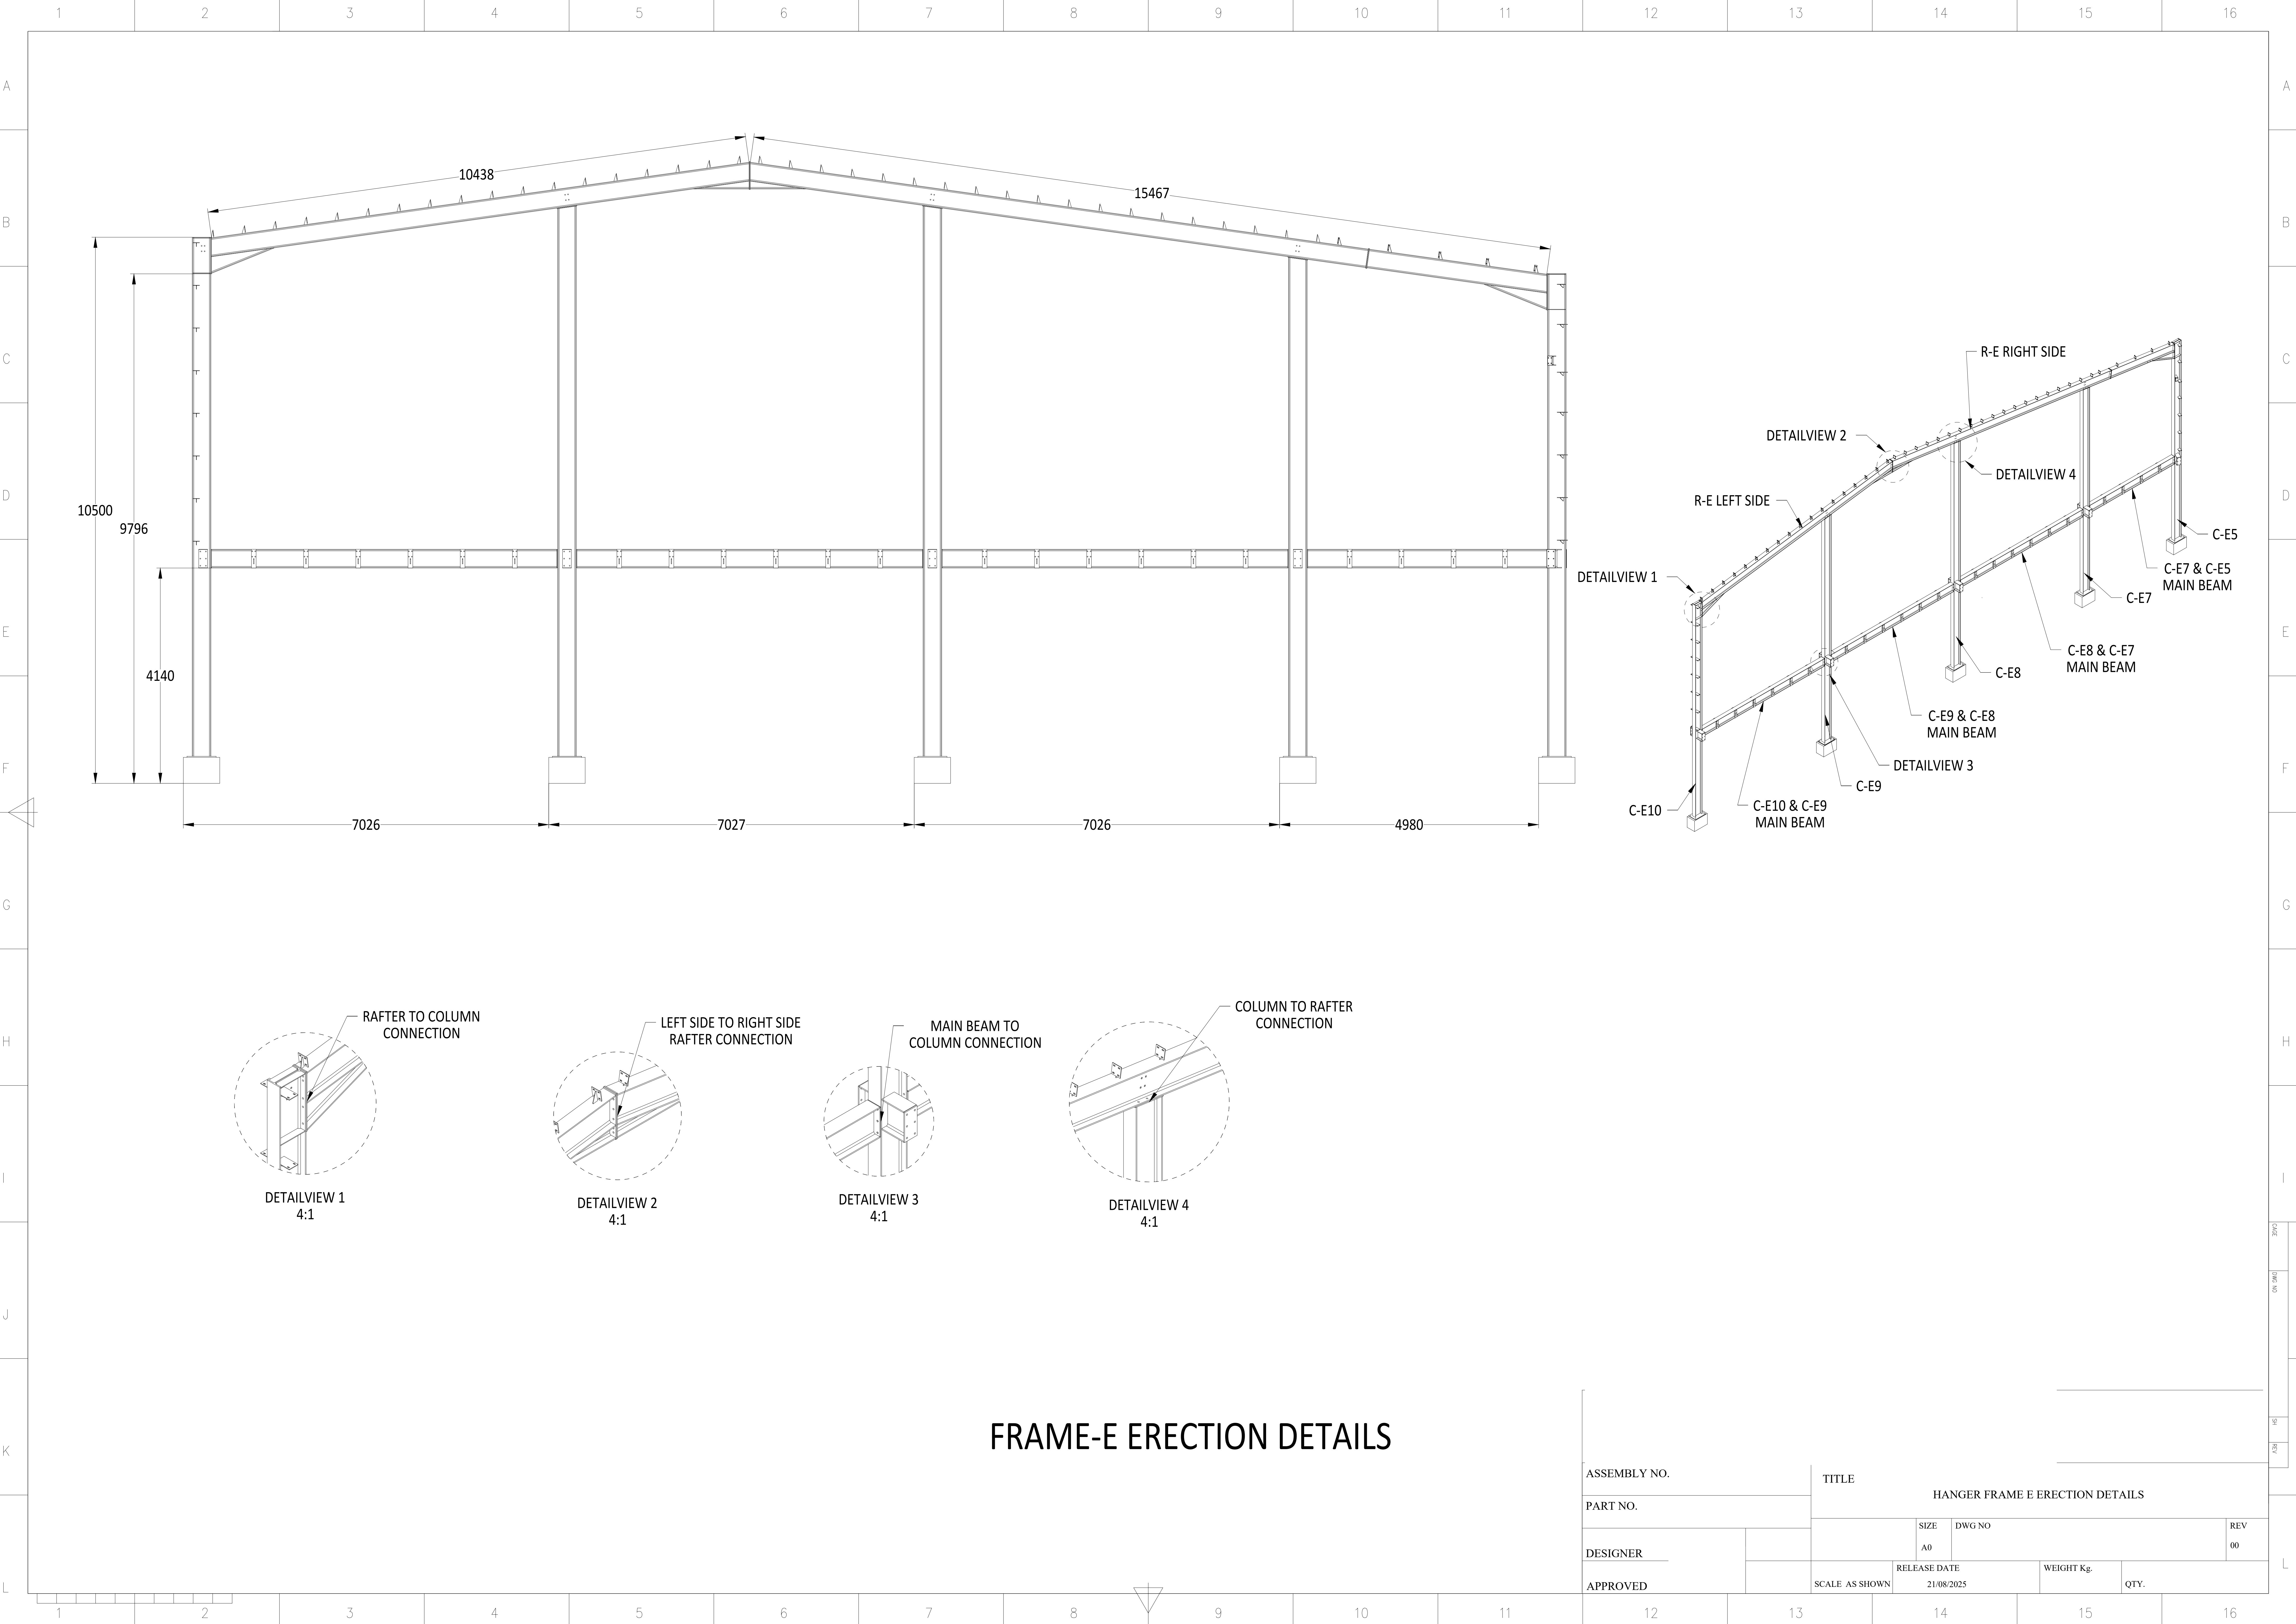


DETAILVIEW 1
4:1

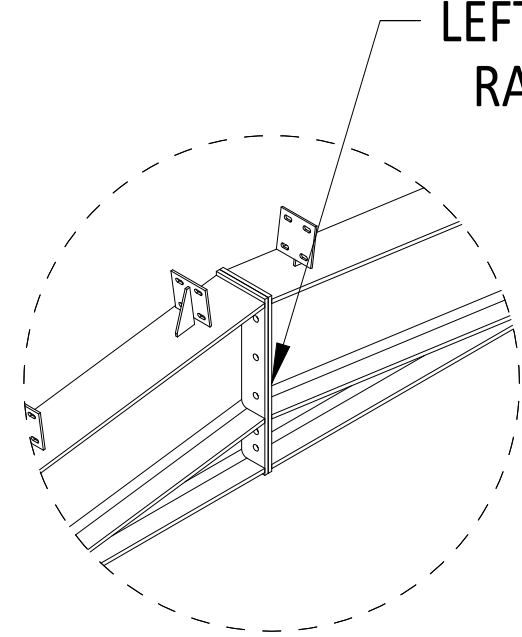

DETAILVIEW 2
4:1

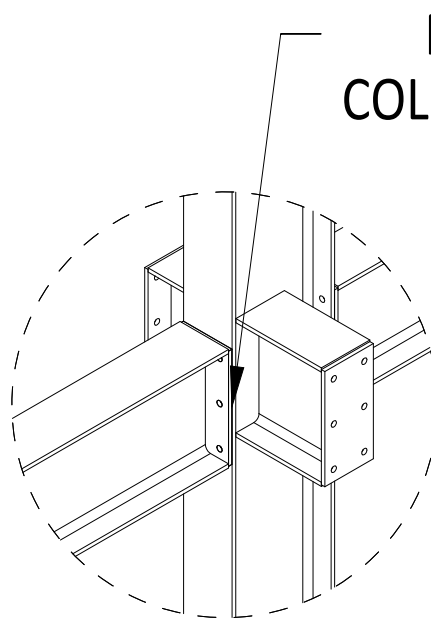


DETAILVIEW 3
4:1

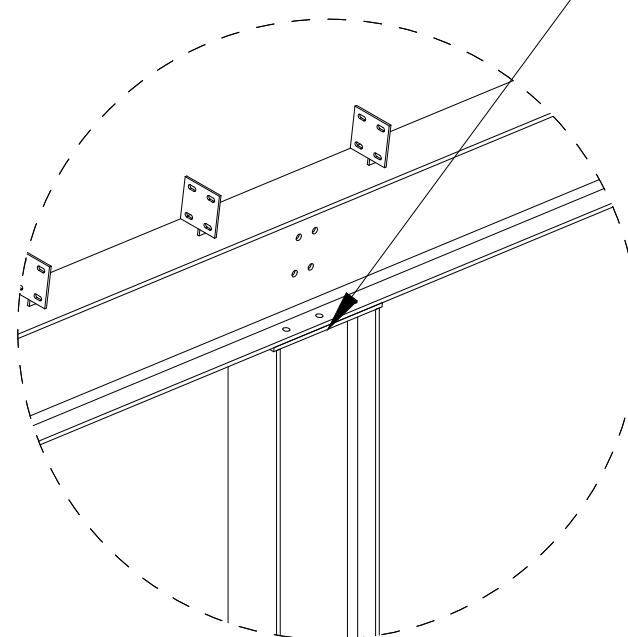

DETAILVIEW 4
4:1

FRAME-E ERECTION DETAILS

ASSEMBLY NO.		TITLE			
PART NO.		HANGER FRAME E ERECTION DETAILS			
DESIGNER		SIZE	DWG NO	REV	
APPROVED		A0		00	
SCALE AS SHOWN		RELEASE DATE		WEIGHT Kg.	QTY.
		21/08/2025			

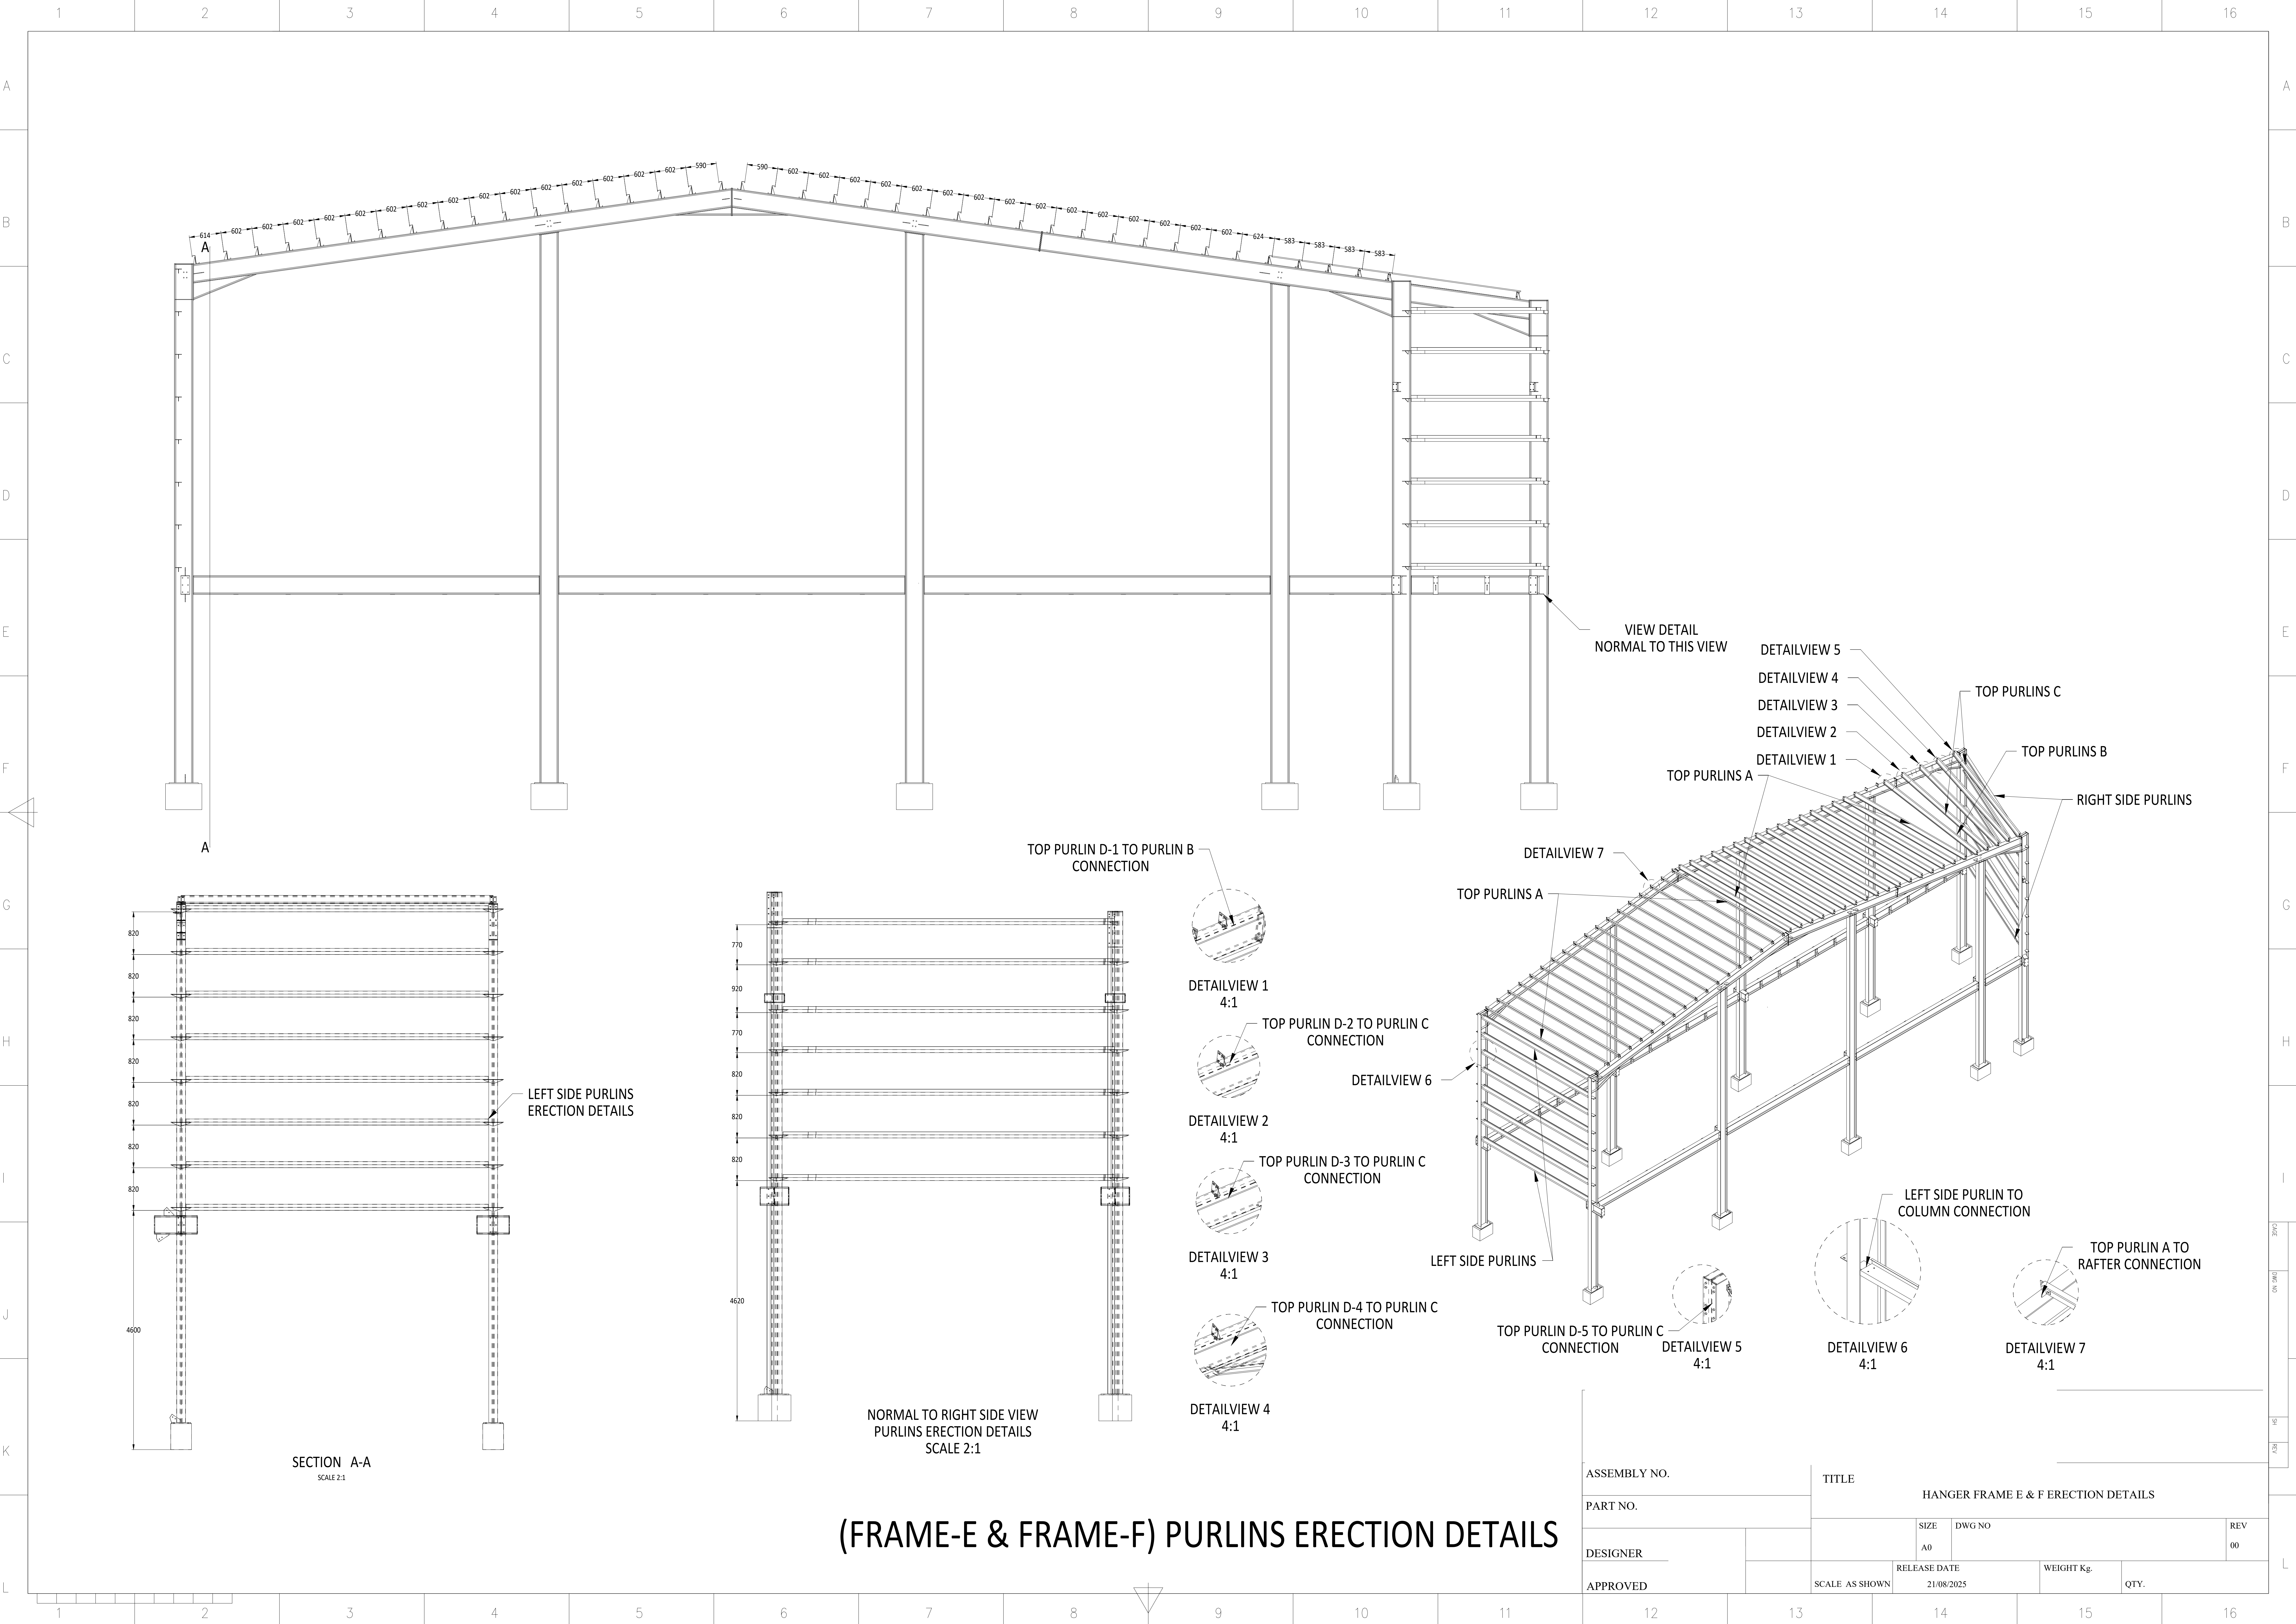

SECTION A-A
SCALE 2:1

NORMAL TO RIGHT SIDE VIEW
PURLINS ERECTION DETAILS
SCALE 2:1

(FRAME-E & FRAME-F) PURLINS ERECTION DETAILS

ASSEMBLY NO.

PART NO.

DESIGNER

APPROVED

TITLE

HANGER FRAME E & F ERECTION DETAILS

SIZE
A0


DWG NO

REV
00

RELEASE DATE
21/08/2025


WEIGHT Kg.

QTY.

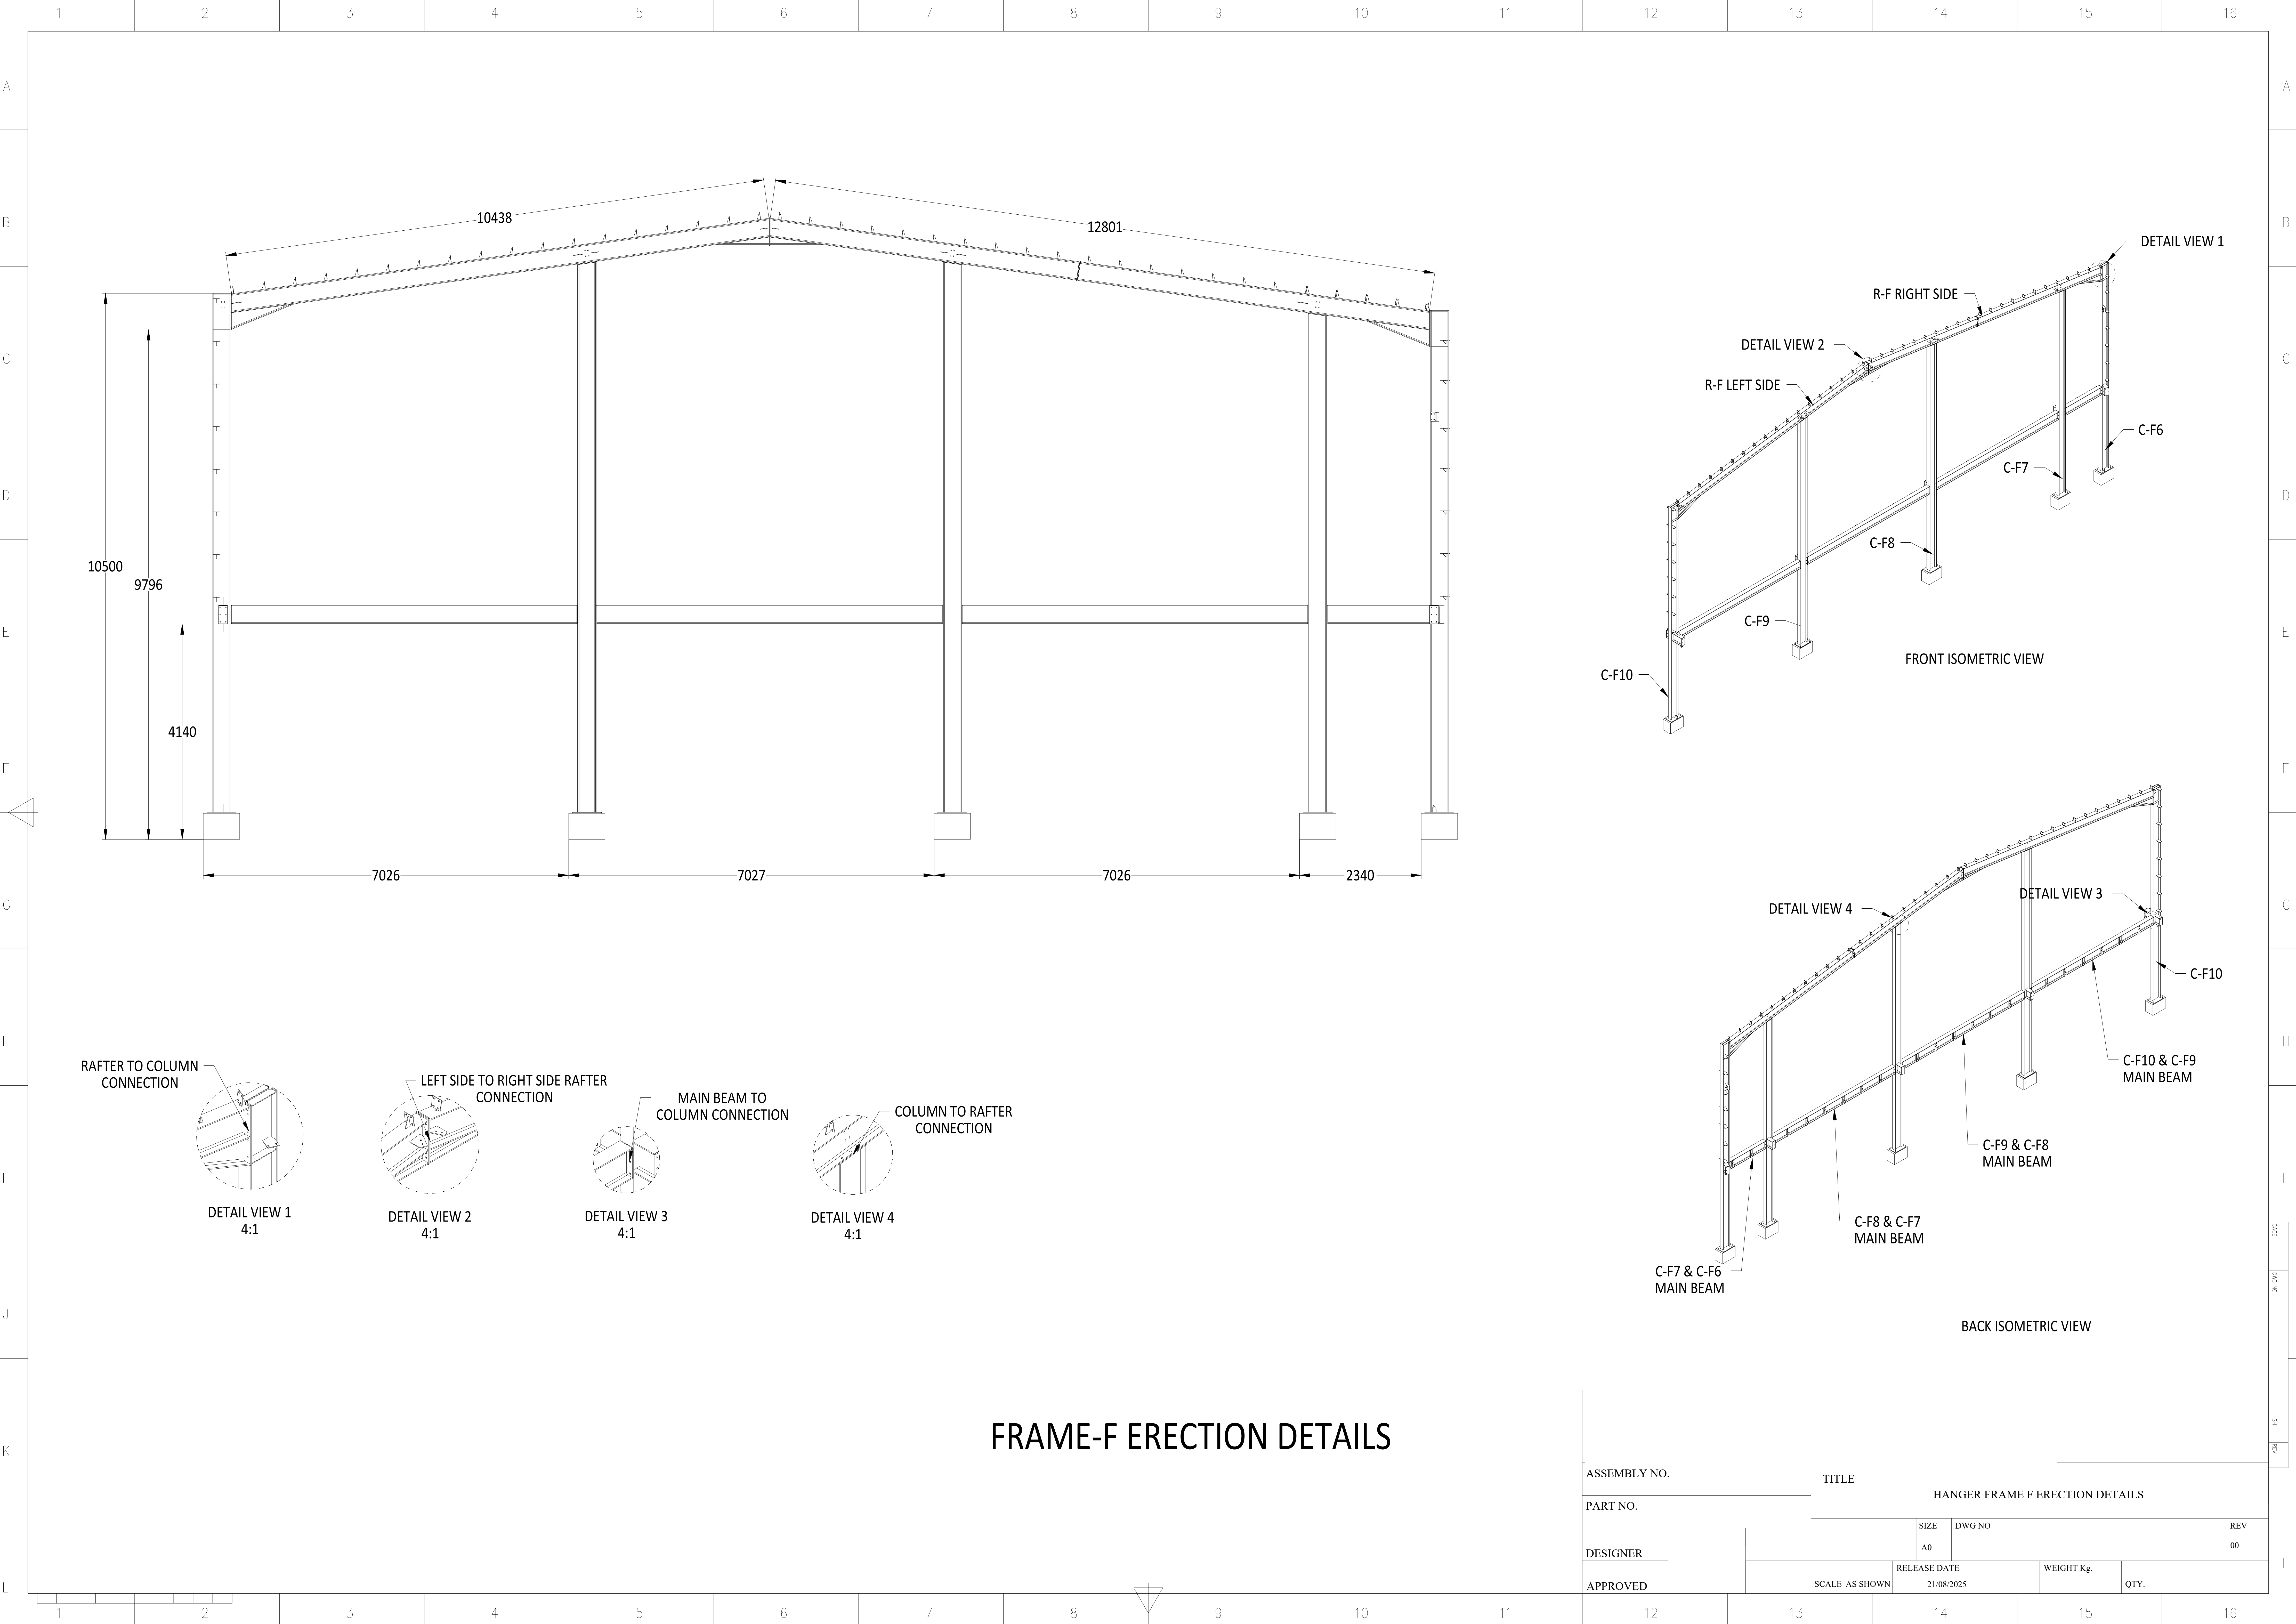


FRAME-F ERECTION DETAILS

ASSEMBLY NO.		TITLE			
PART NO.		HANGER FRAME F ERECTION DETAILS			
DESIGNER		SIZE	DWG NO	REV	
APPROVED		A0		00	
SCALE AS SHOWN		RELEASE DATE		WEIGHT Kg.	QTY.
		21/08/2025			

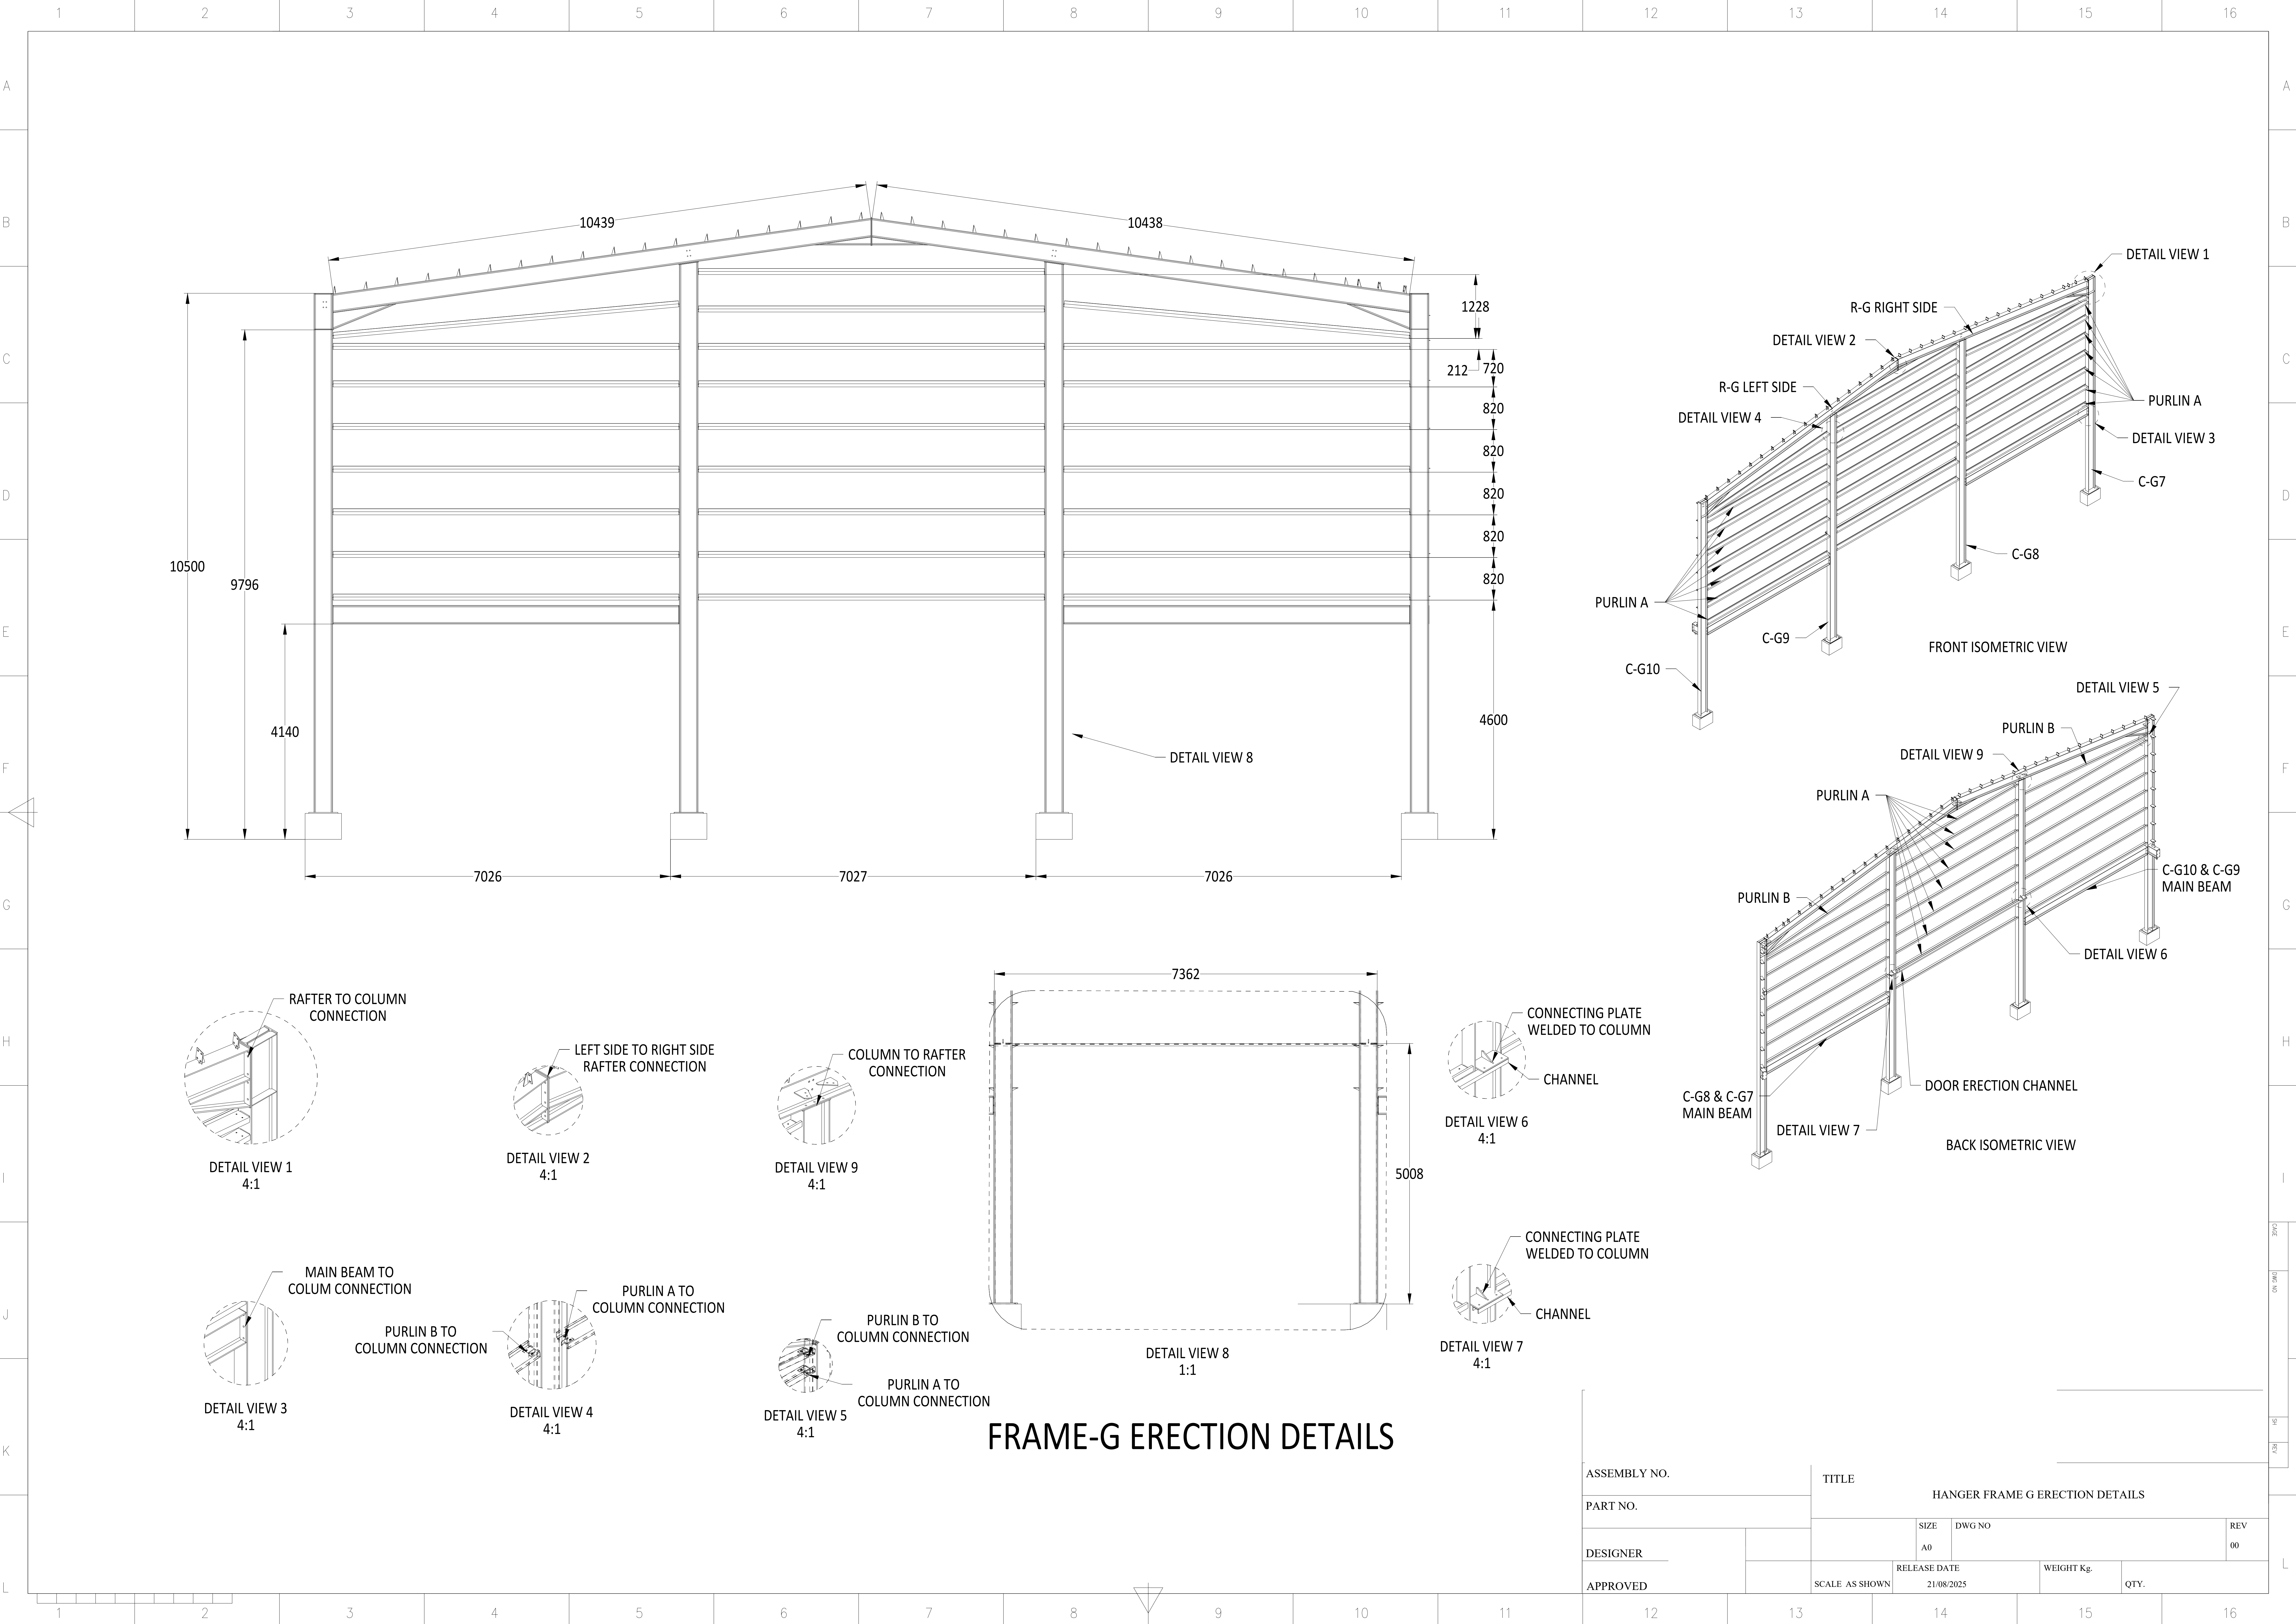



ASSEMBLY NO.		TITLE			
PART NO.		HANGER FRAME G ERECTION DETAILS			
DESIGNER		SIZE	DWG NO	REV	
APPROVED		A0		00	
SCALE AS SHOWN		RELEASE DATE		WEIGHT Kg.	QTY.
		21/08/2025			

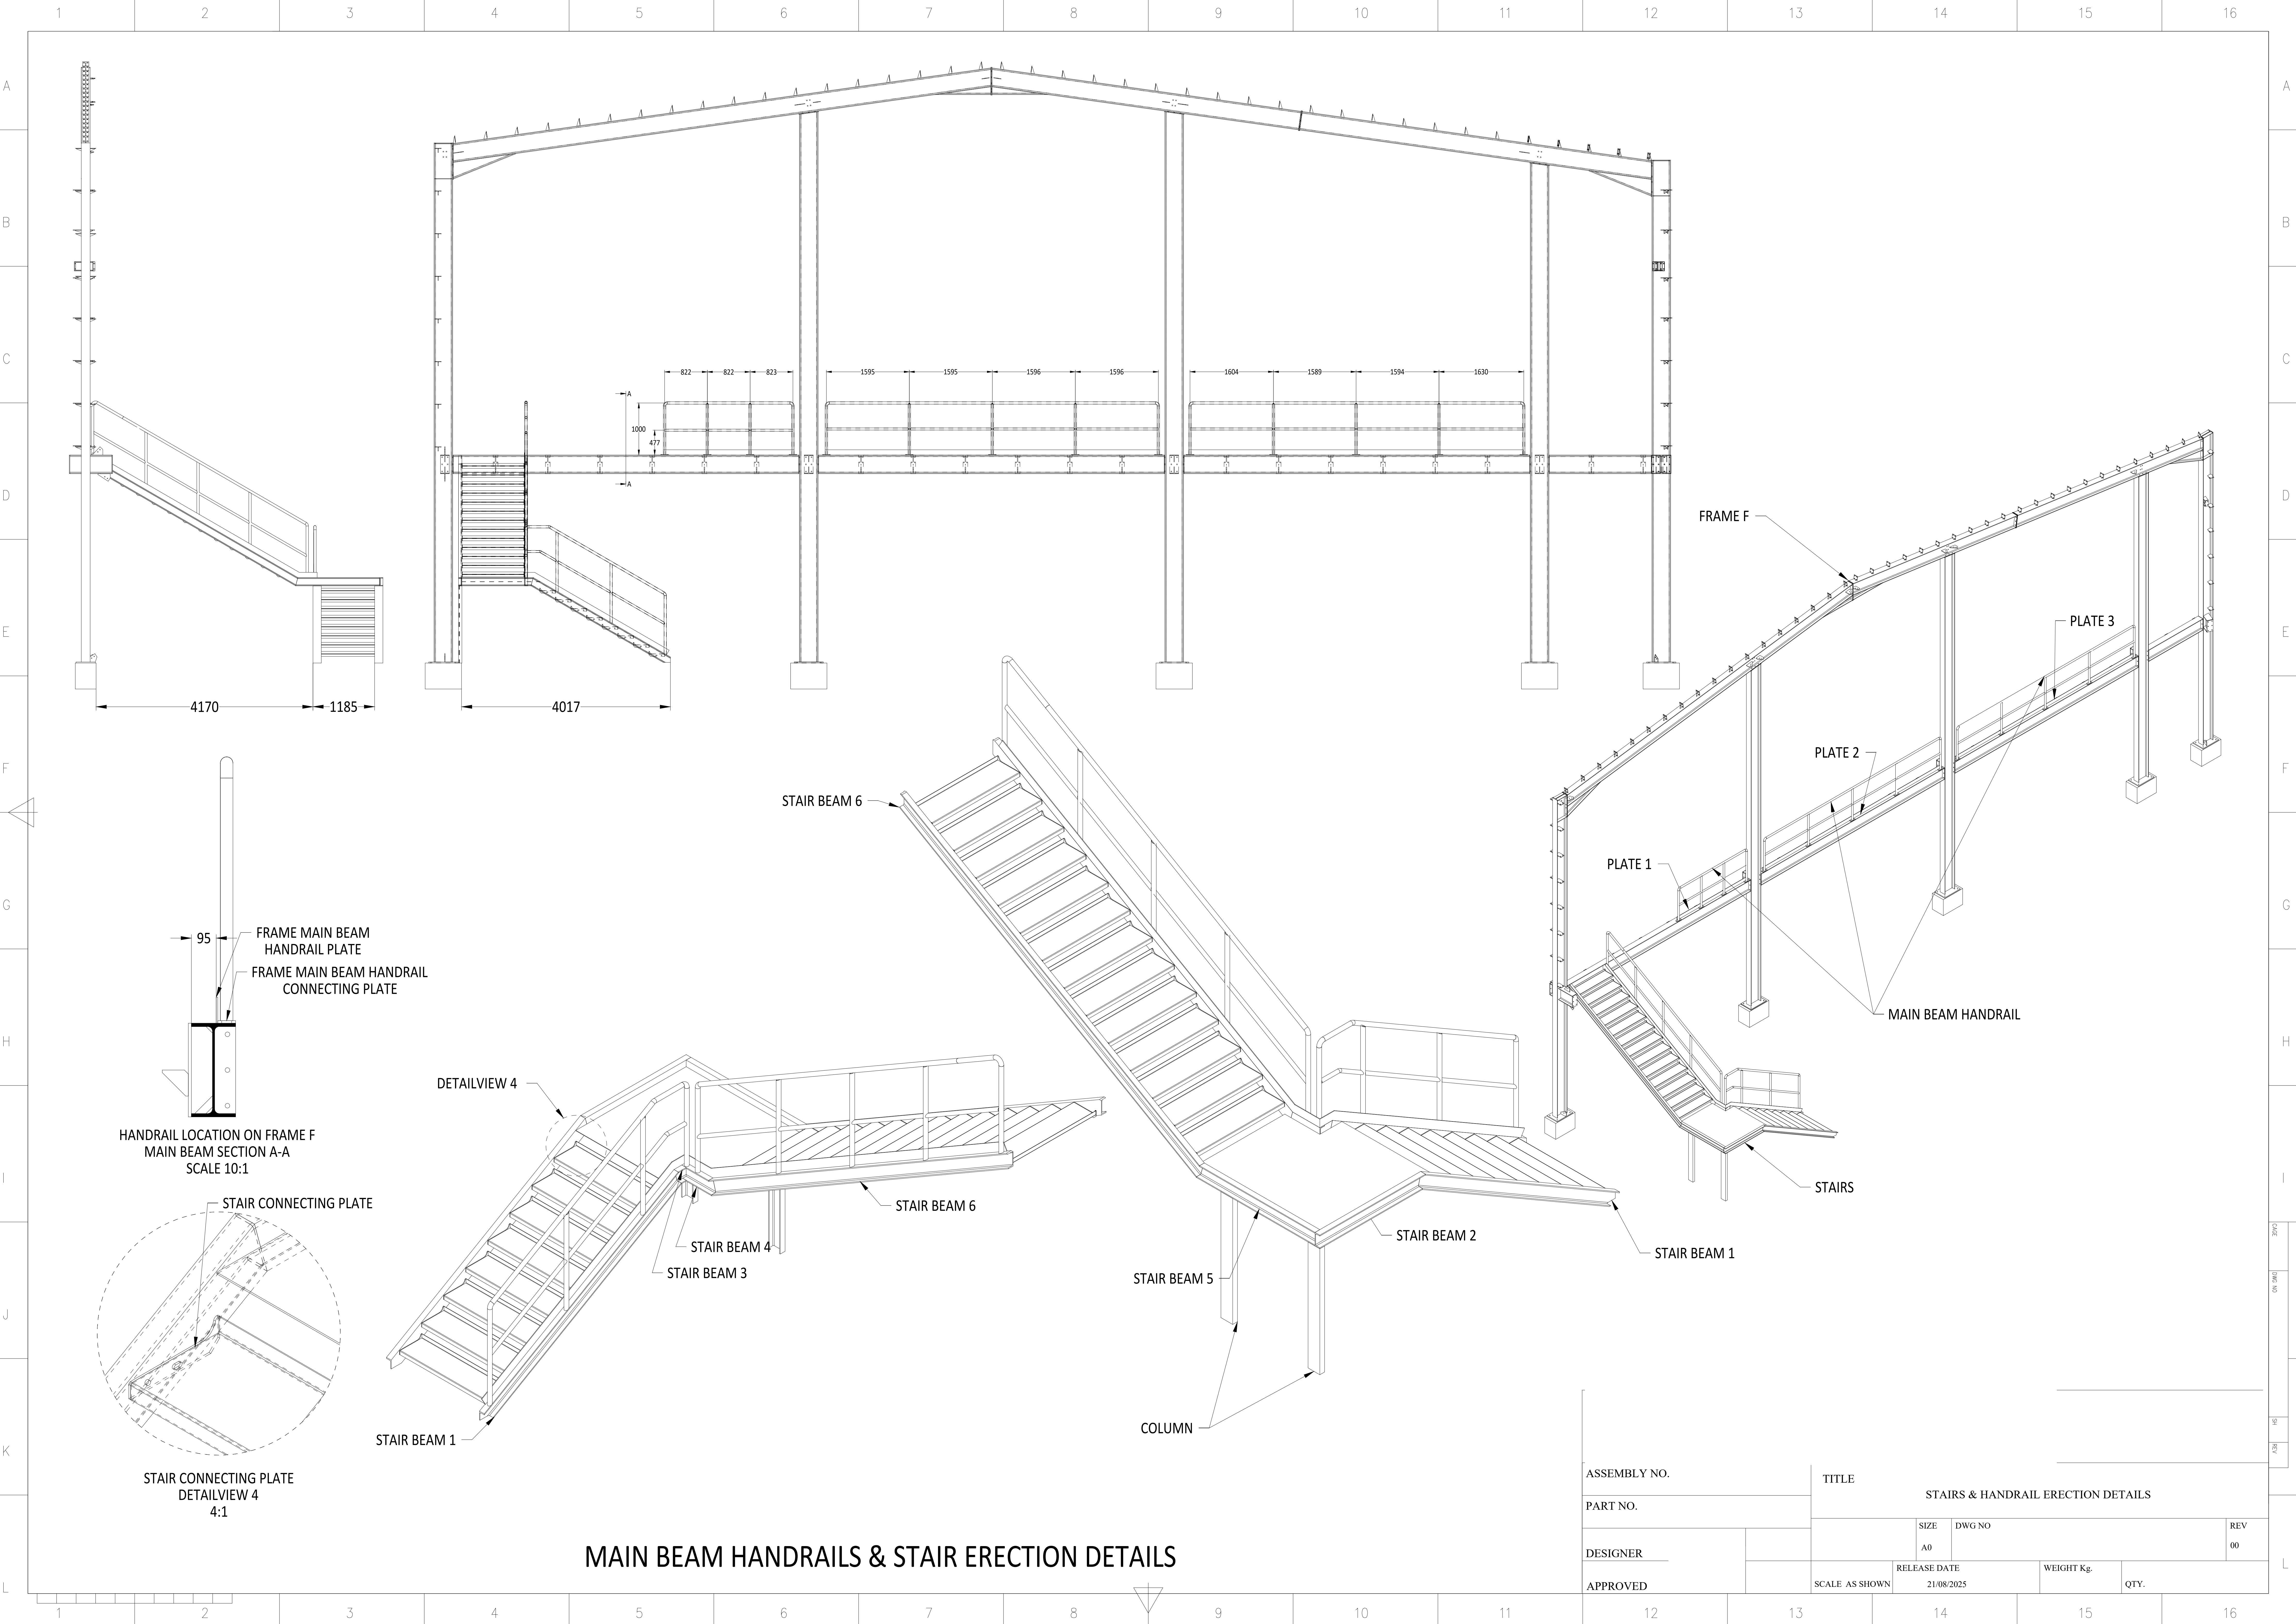

MAIN BEAM HANDRAILS & STAIR ERECTION DETAILS


ASSEMBLY NO.		TITLE			
PART NO.		STAIRS & HANDRAIL ERECTION DETAILS			
DESIGNER		SIZE	DWG NO	REV	
APPROVED		A0		00	
SCALE AS SHOWN		RELEASE DATE		WEIGHT Kg.	QTY.
		21/08/2025			

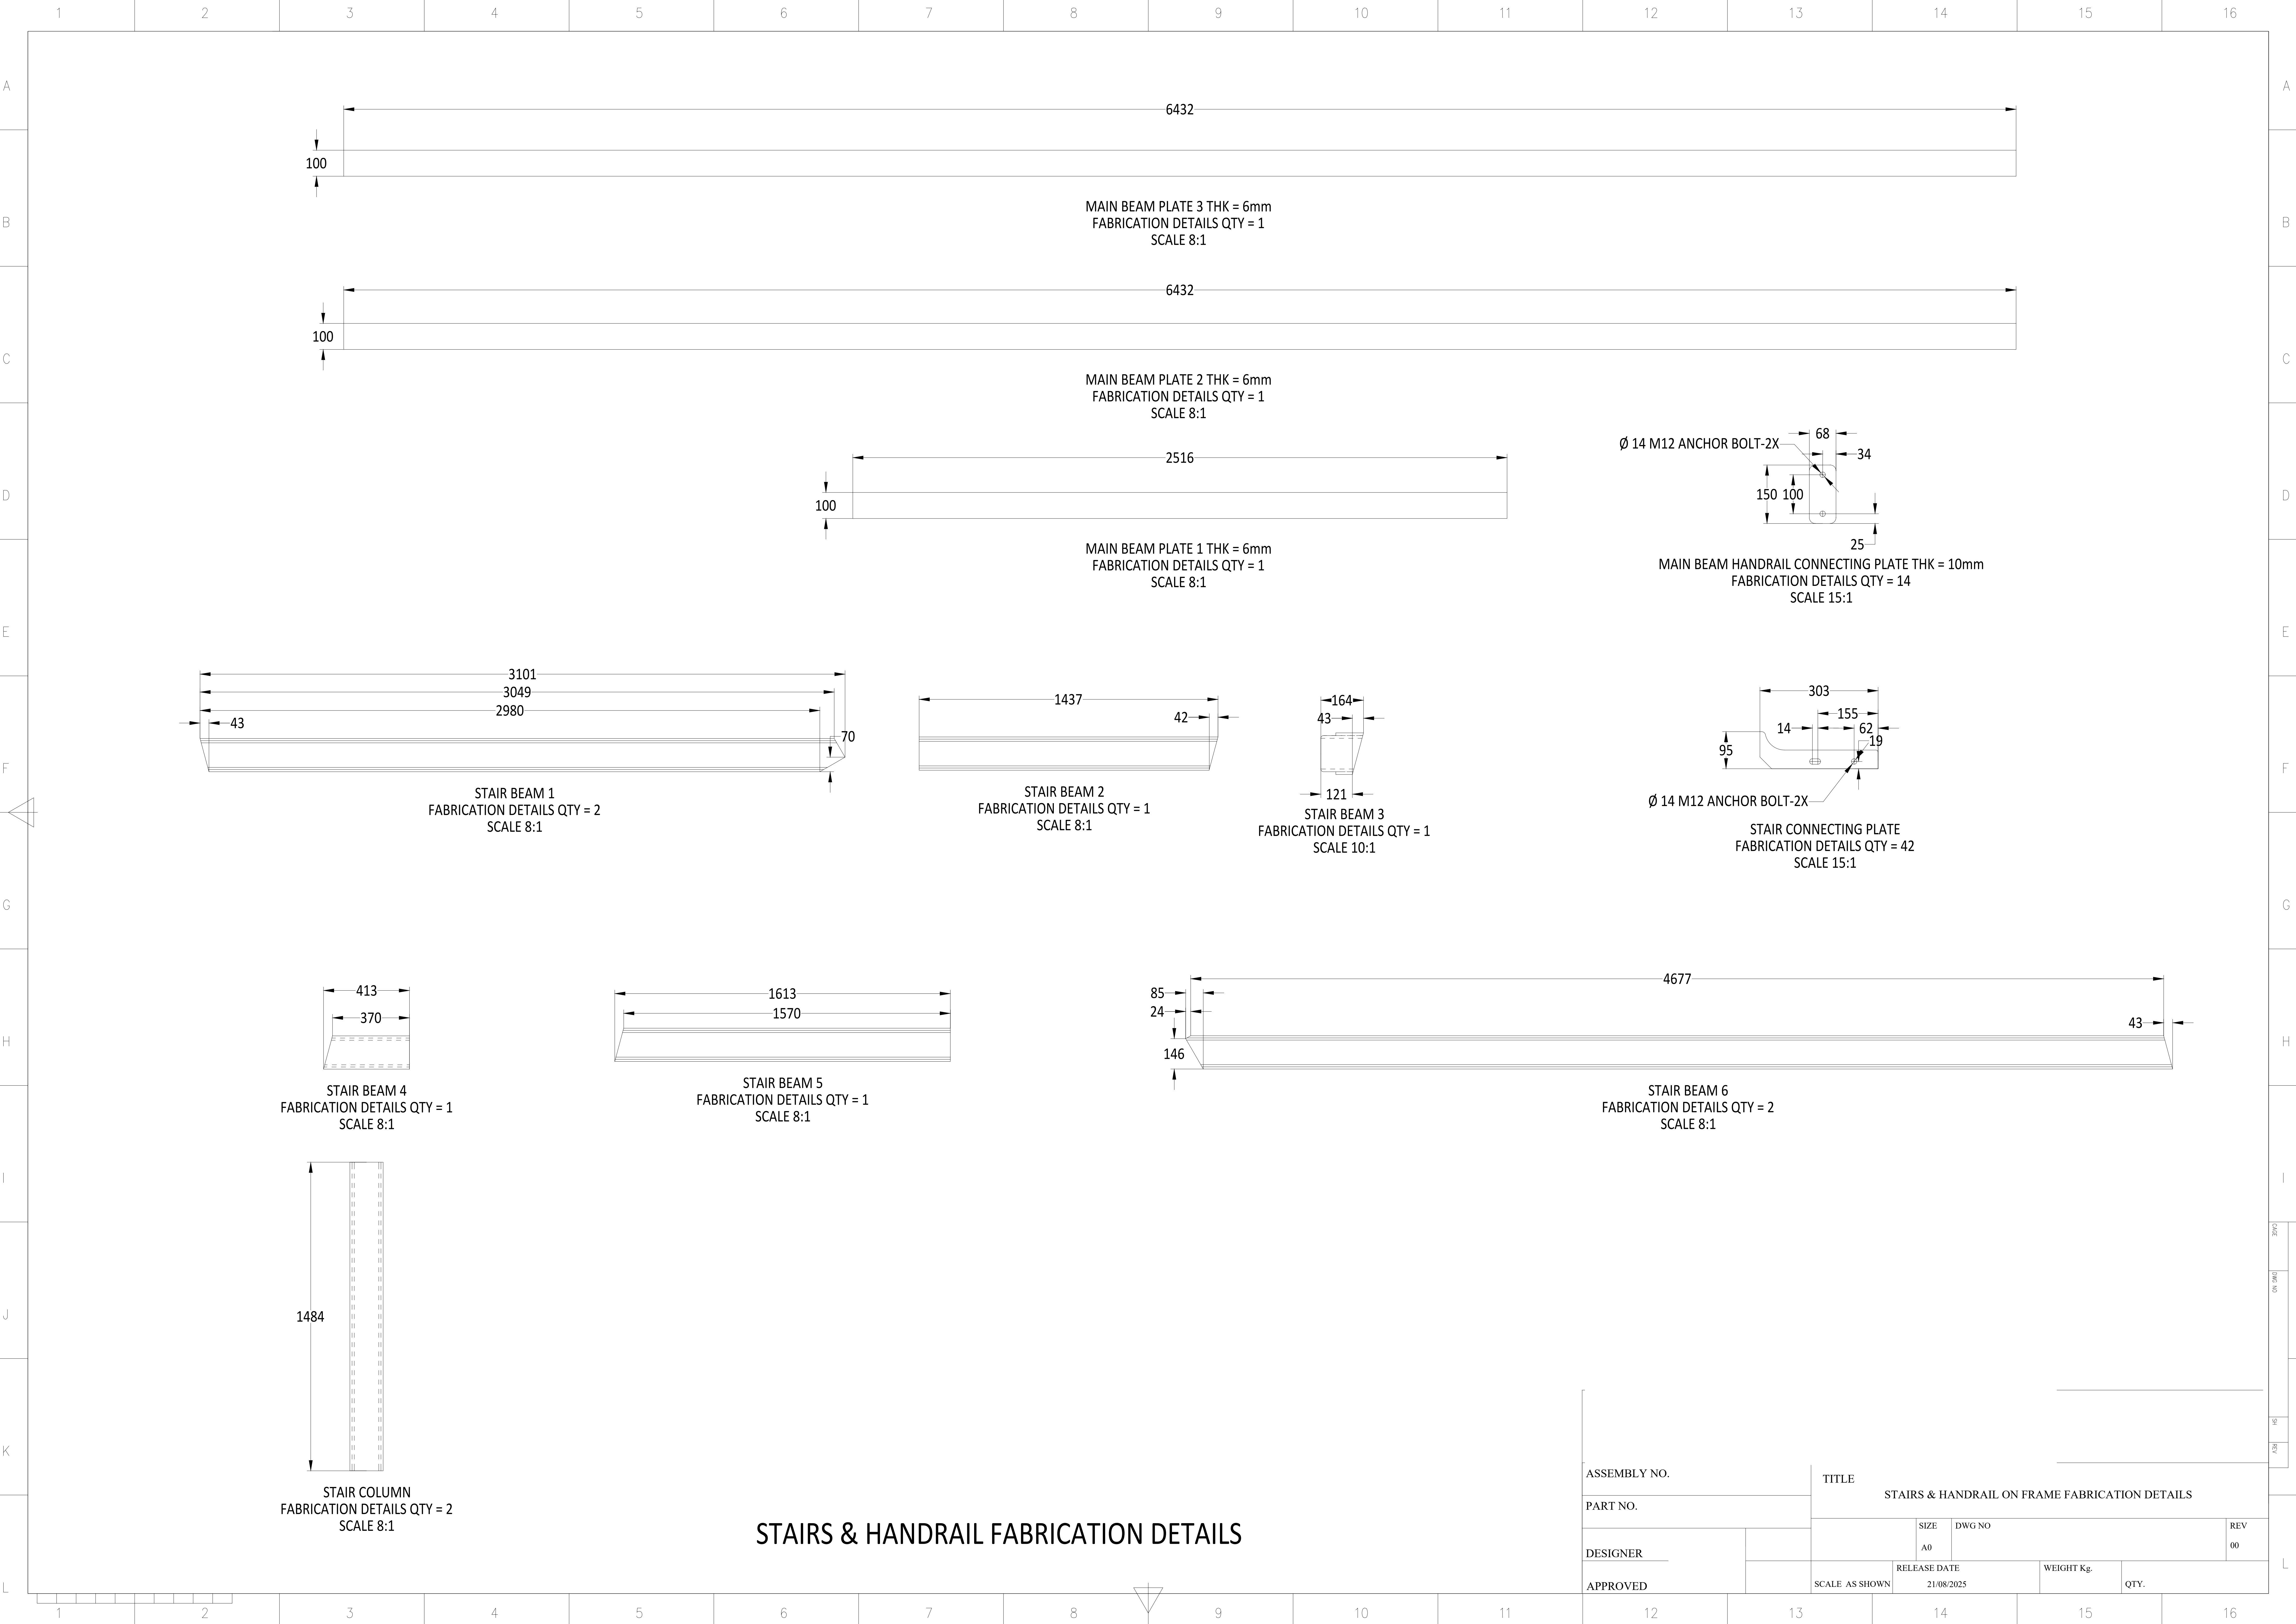

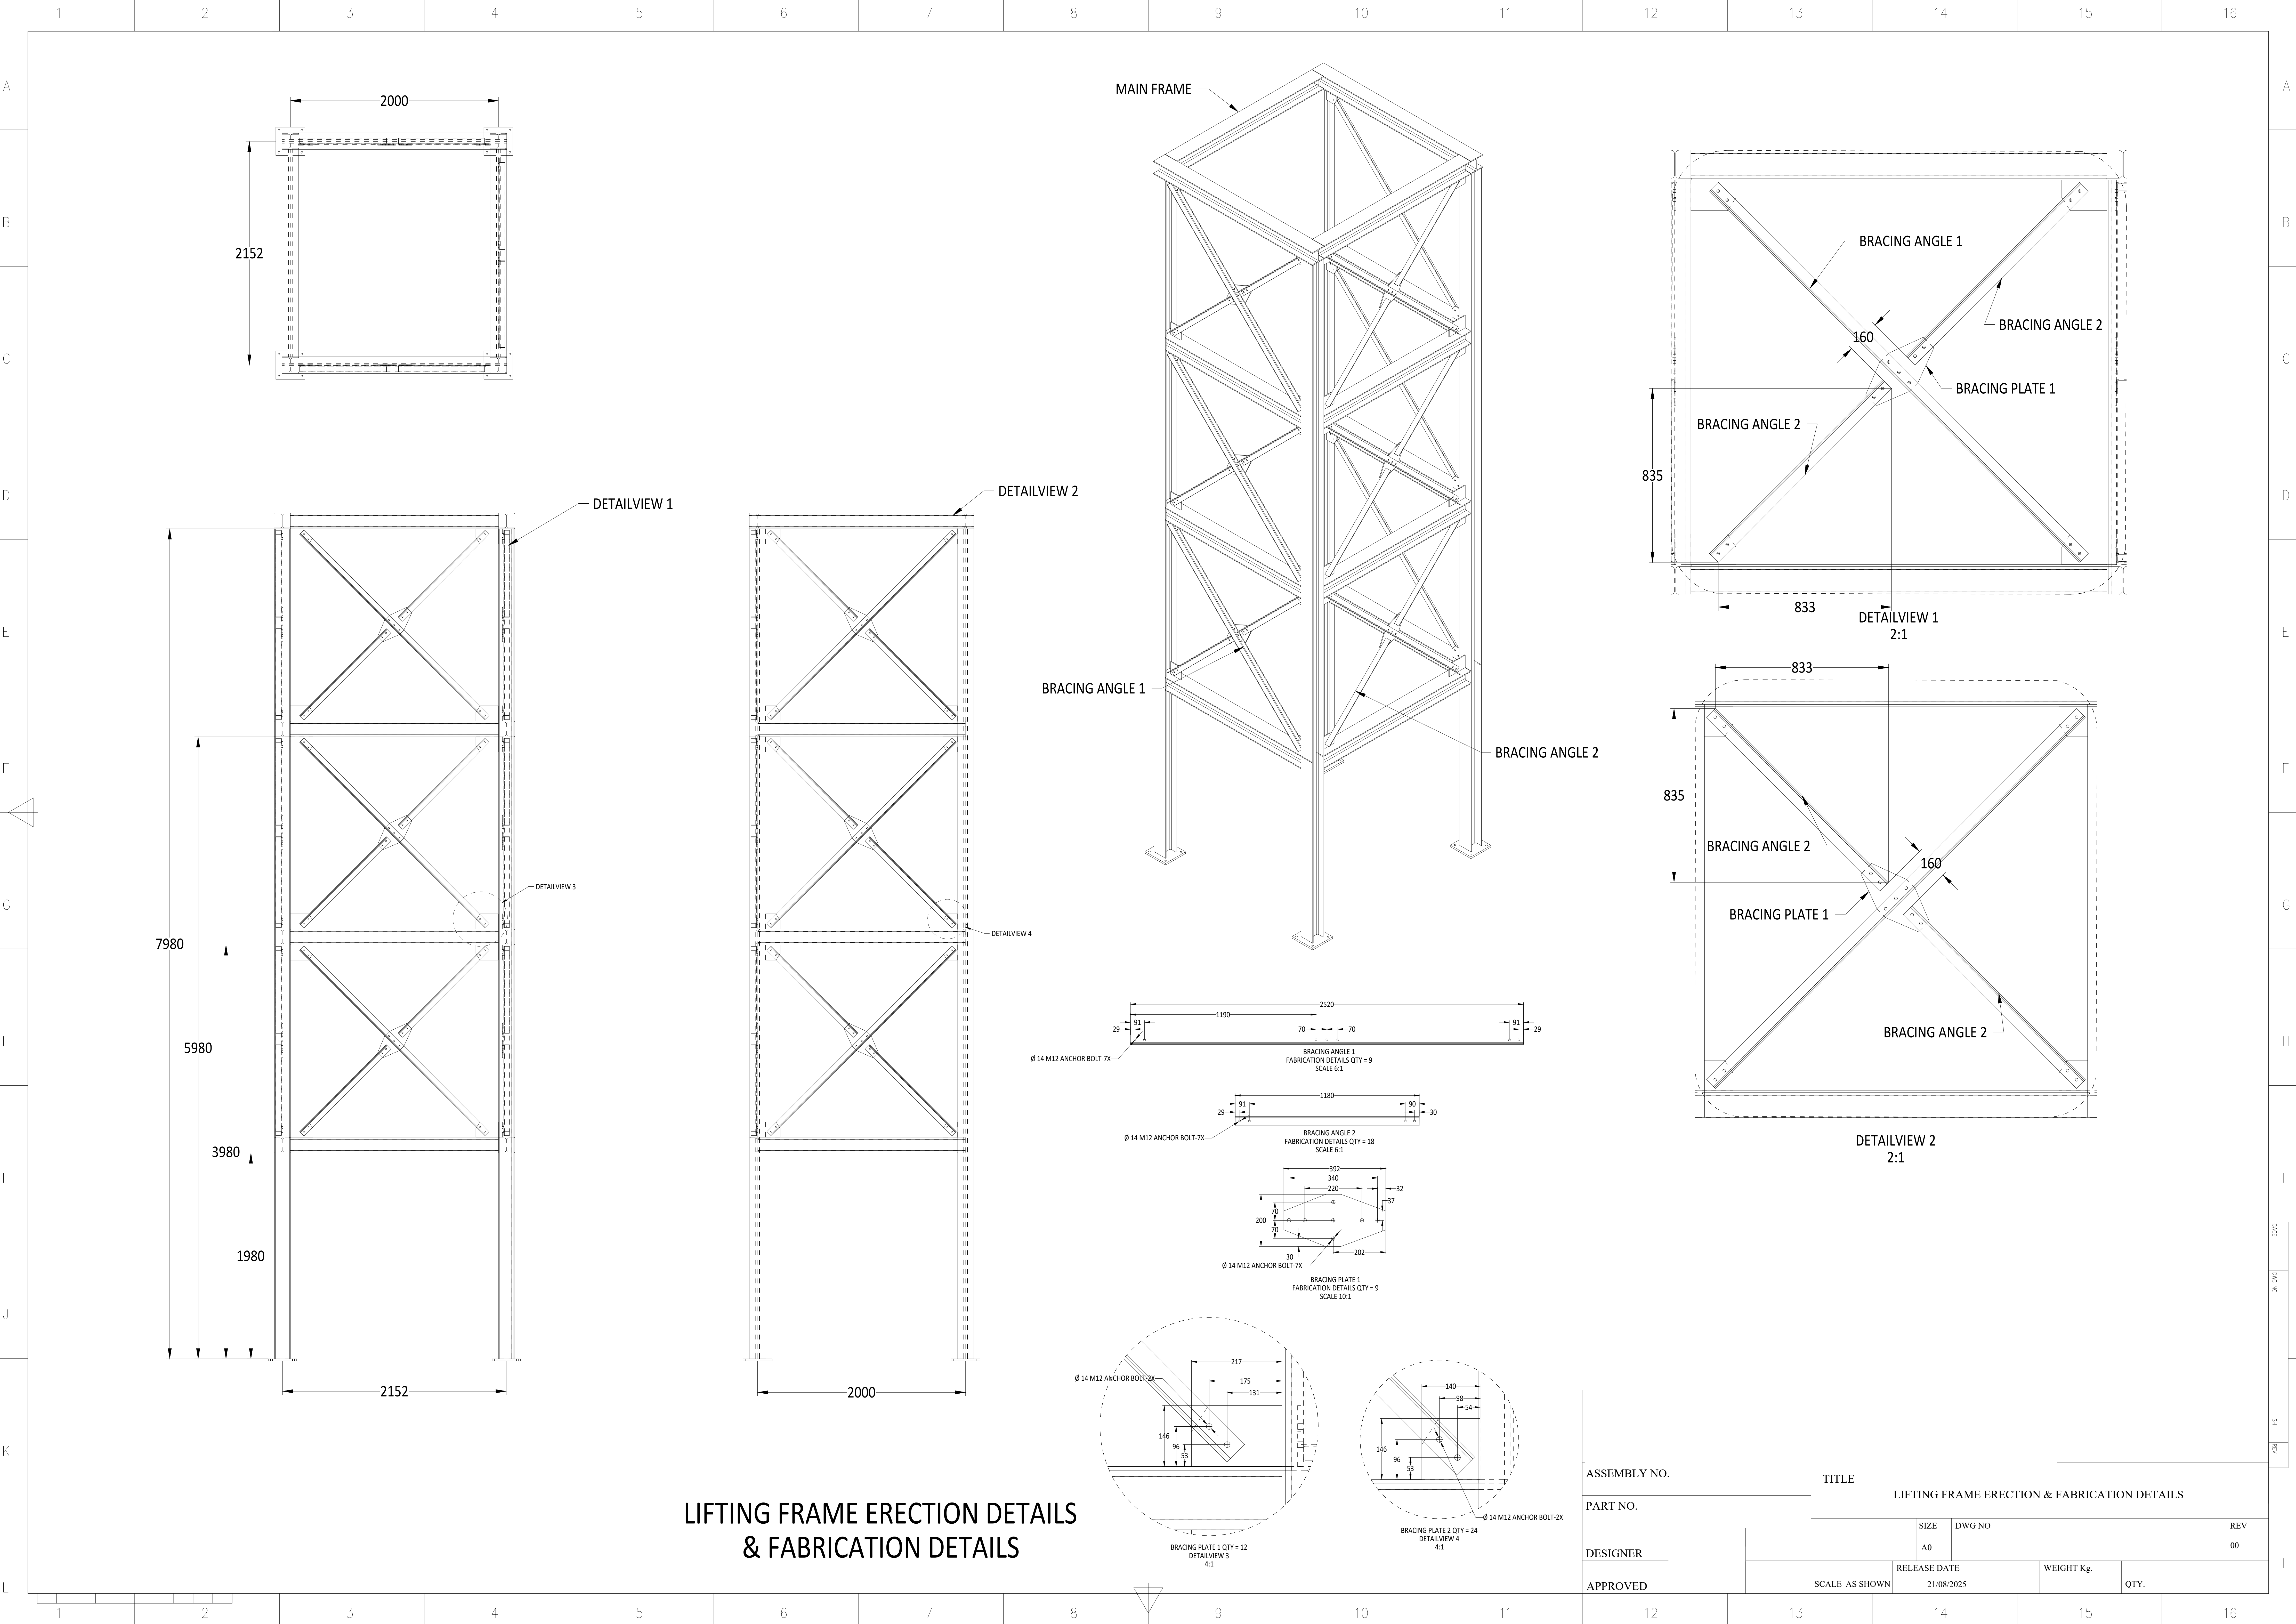


LIFTING FRAME ERECTION DETAILS
& FABRICATION DETAILS


ASSEMBLY NO.		TITLE			
PART NO.		LIFTING FRAME ERECTION & FABRICATION DETAILS			
DESIGNER		SIZE	DWG NO	REV	
APPROVED		A0		00	
SCALE AS SHOWN		RELEASE DATE	WEIGHT Kg.	QTY.	
		21/08/2025			

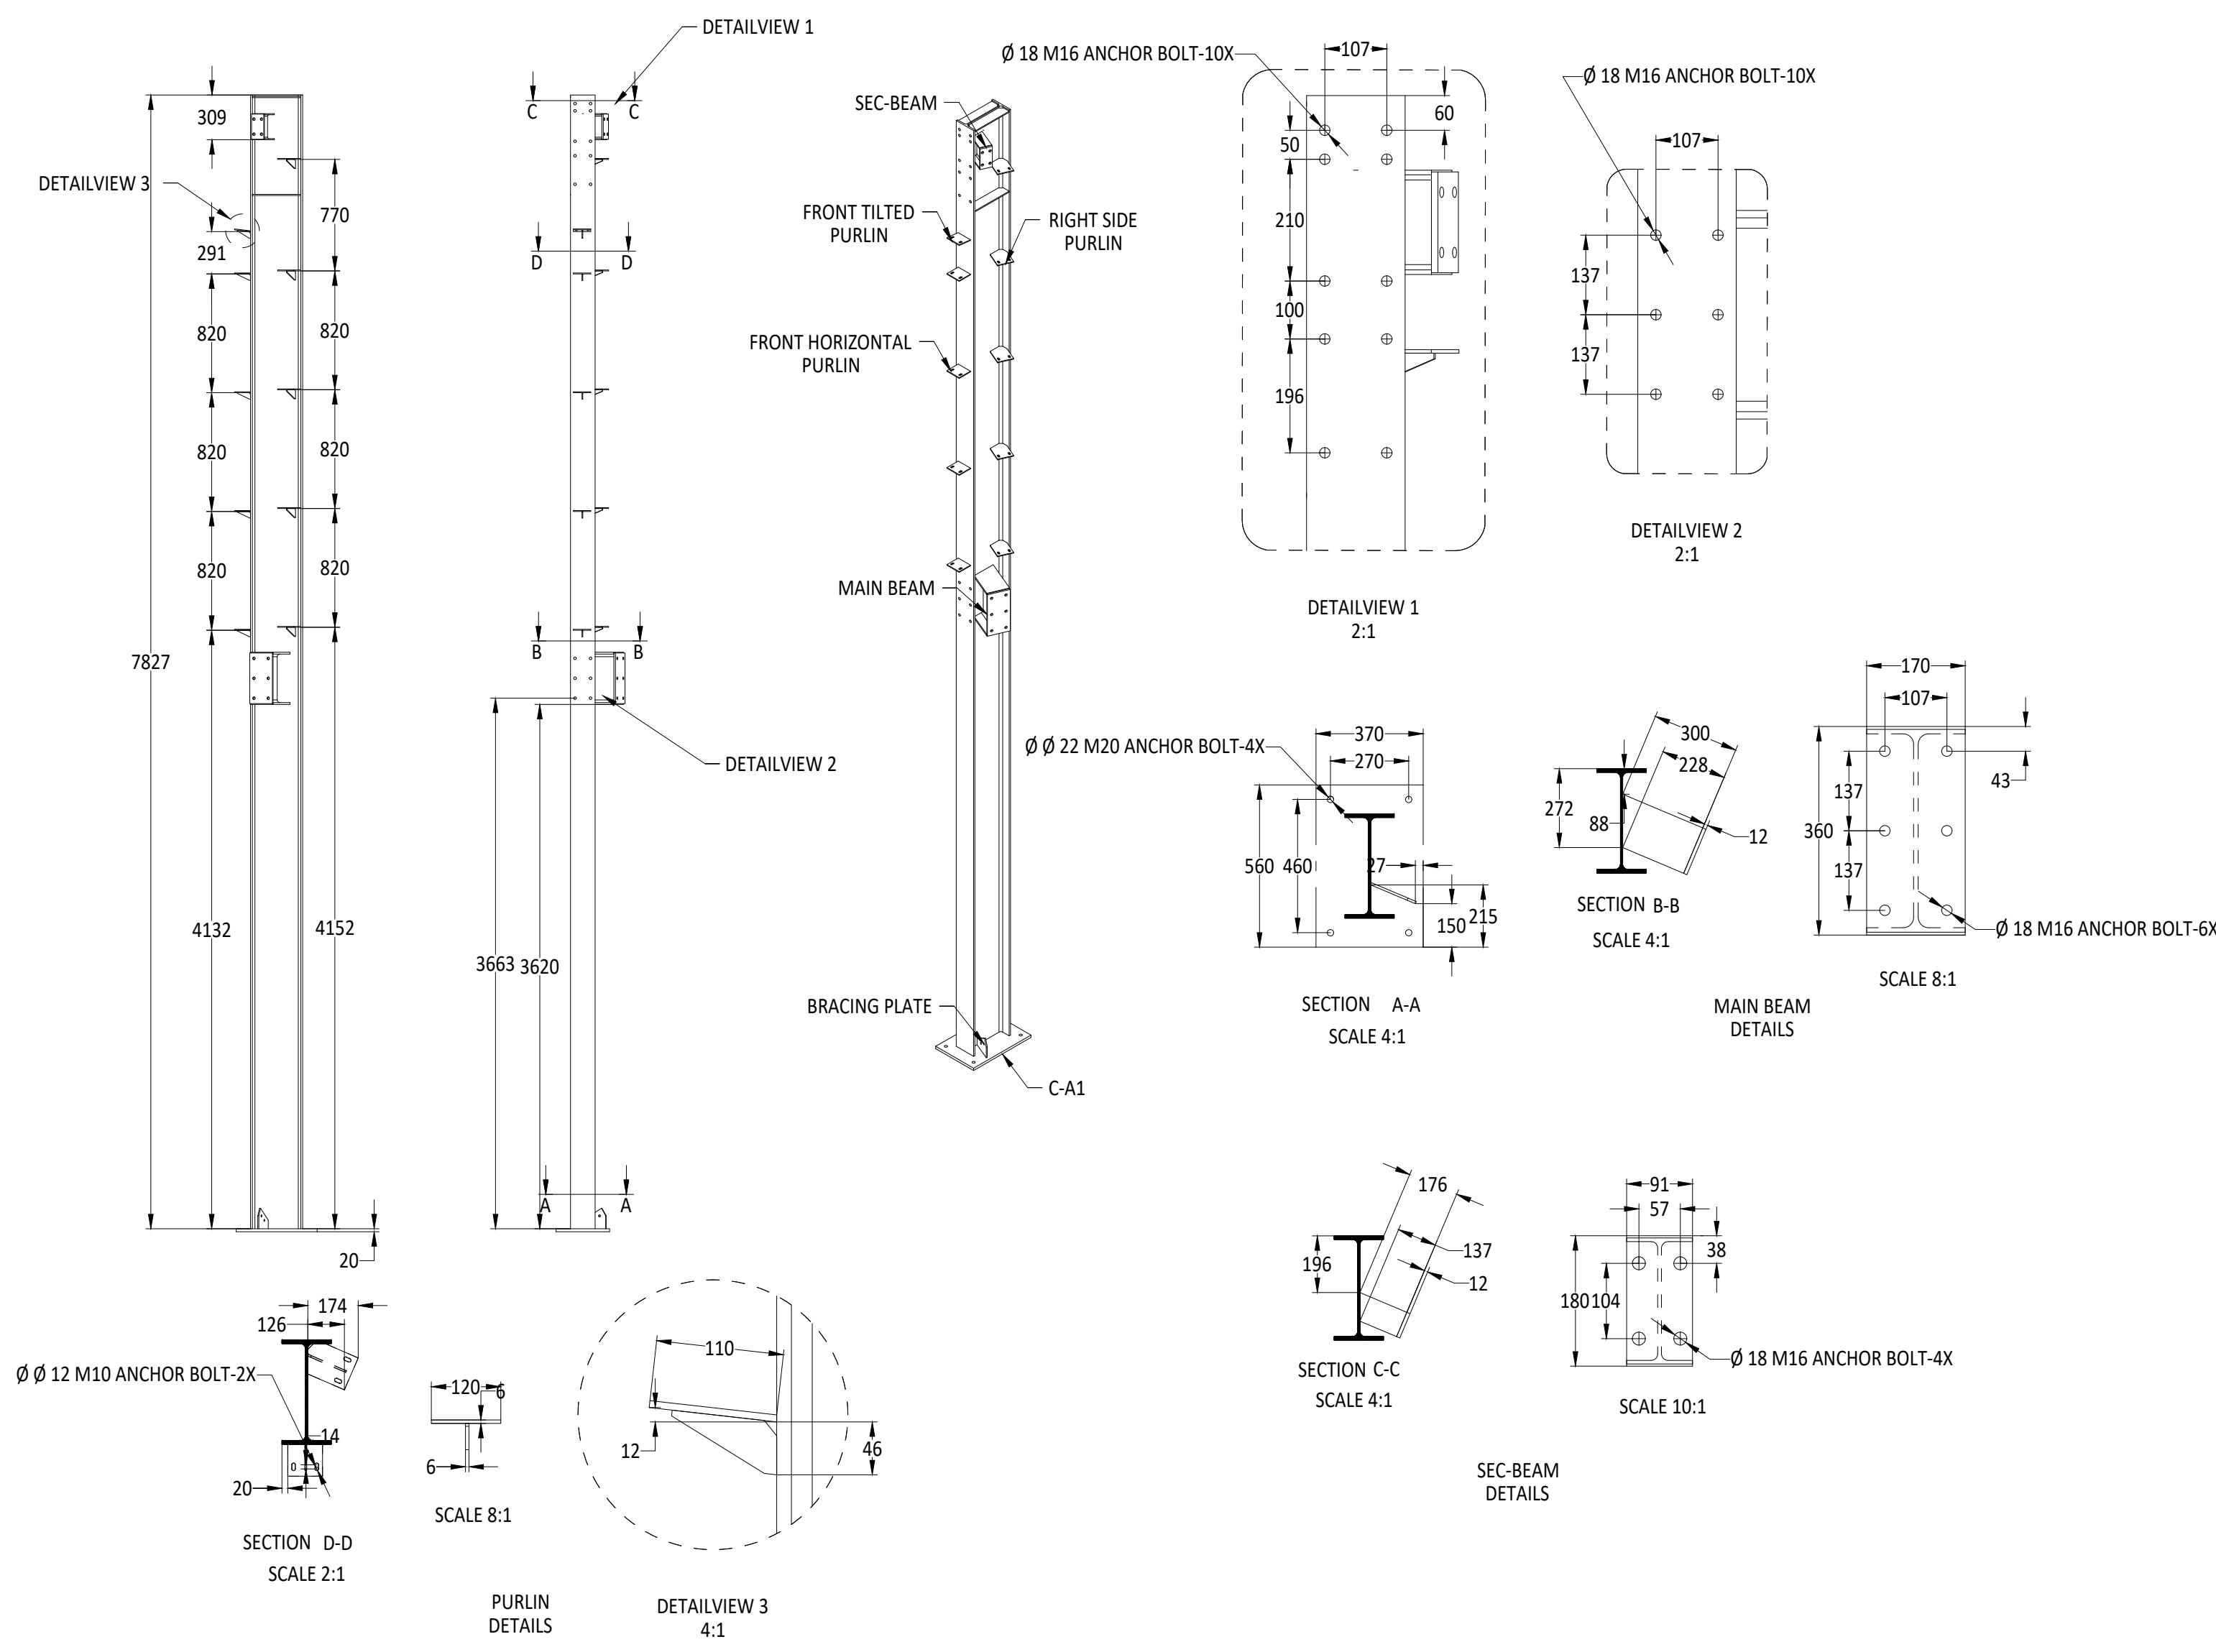


COLUMN C-A1 FABRICATION DETAILS

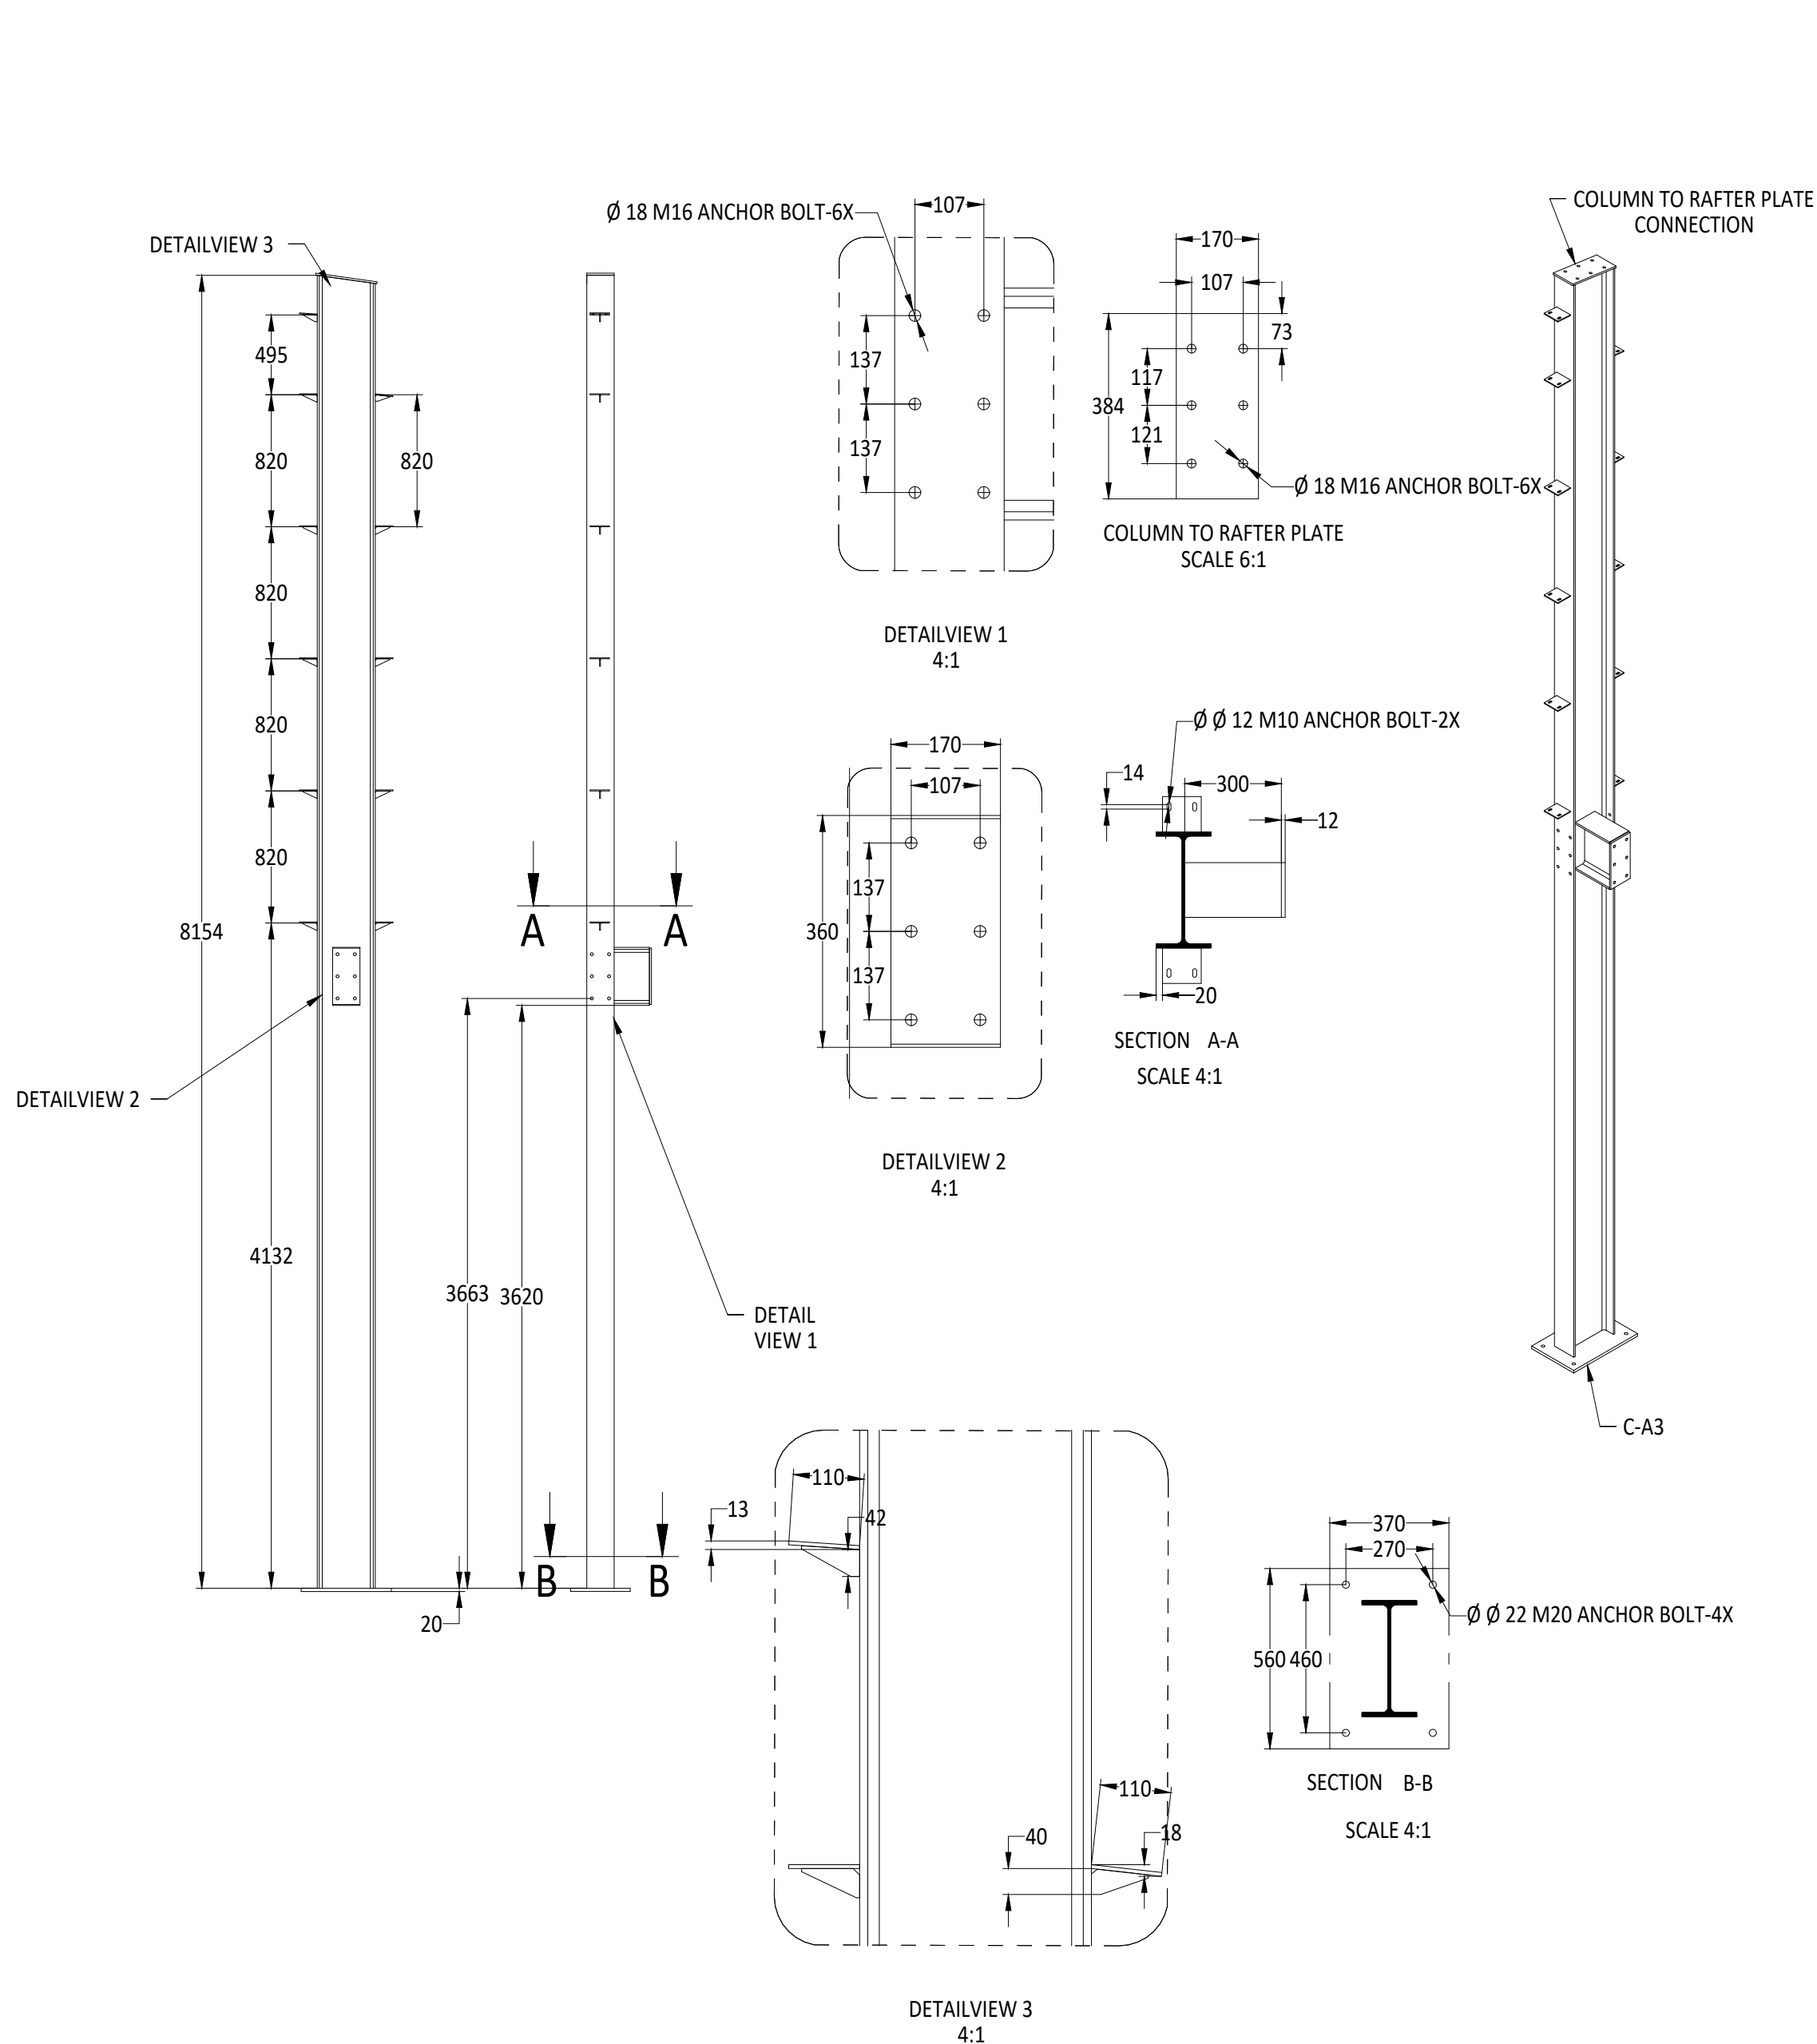


COLUMN C-A3 FABRICATION DETAILS

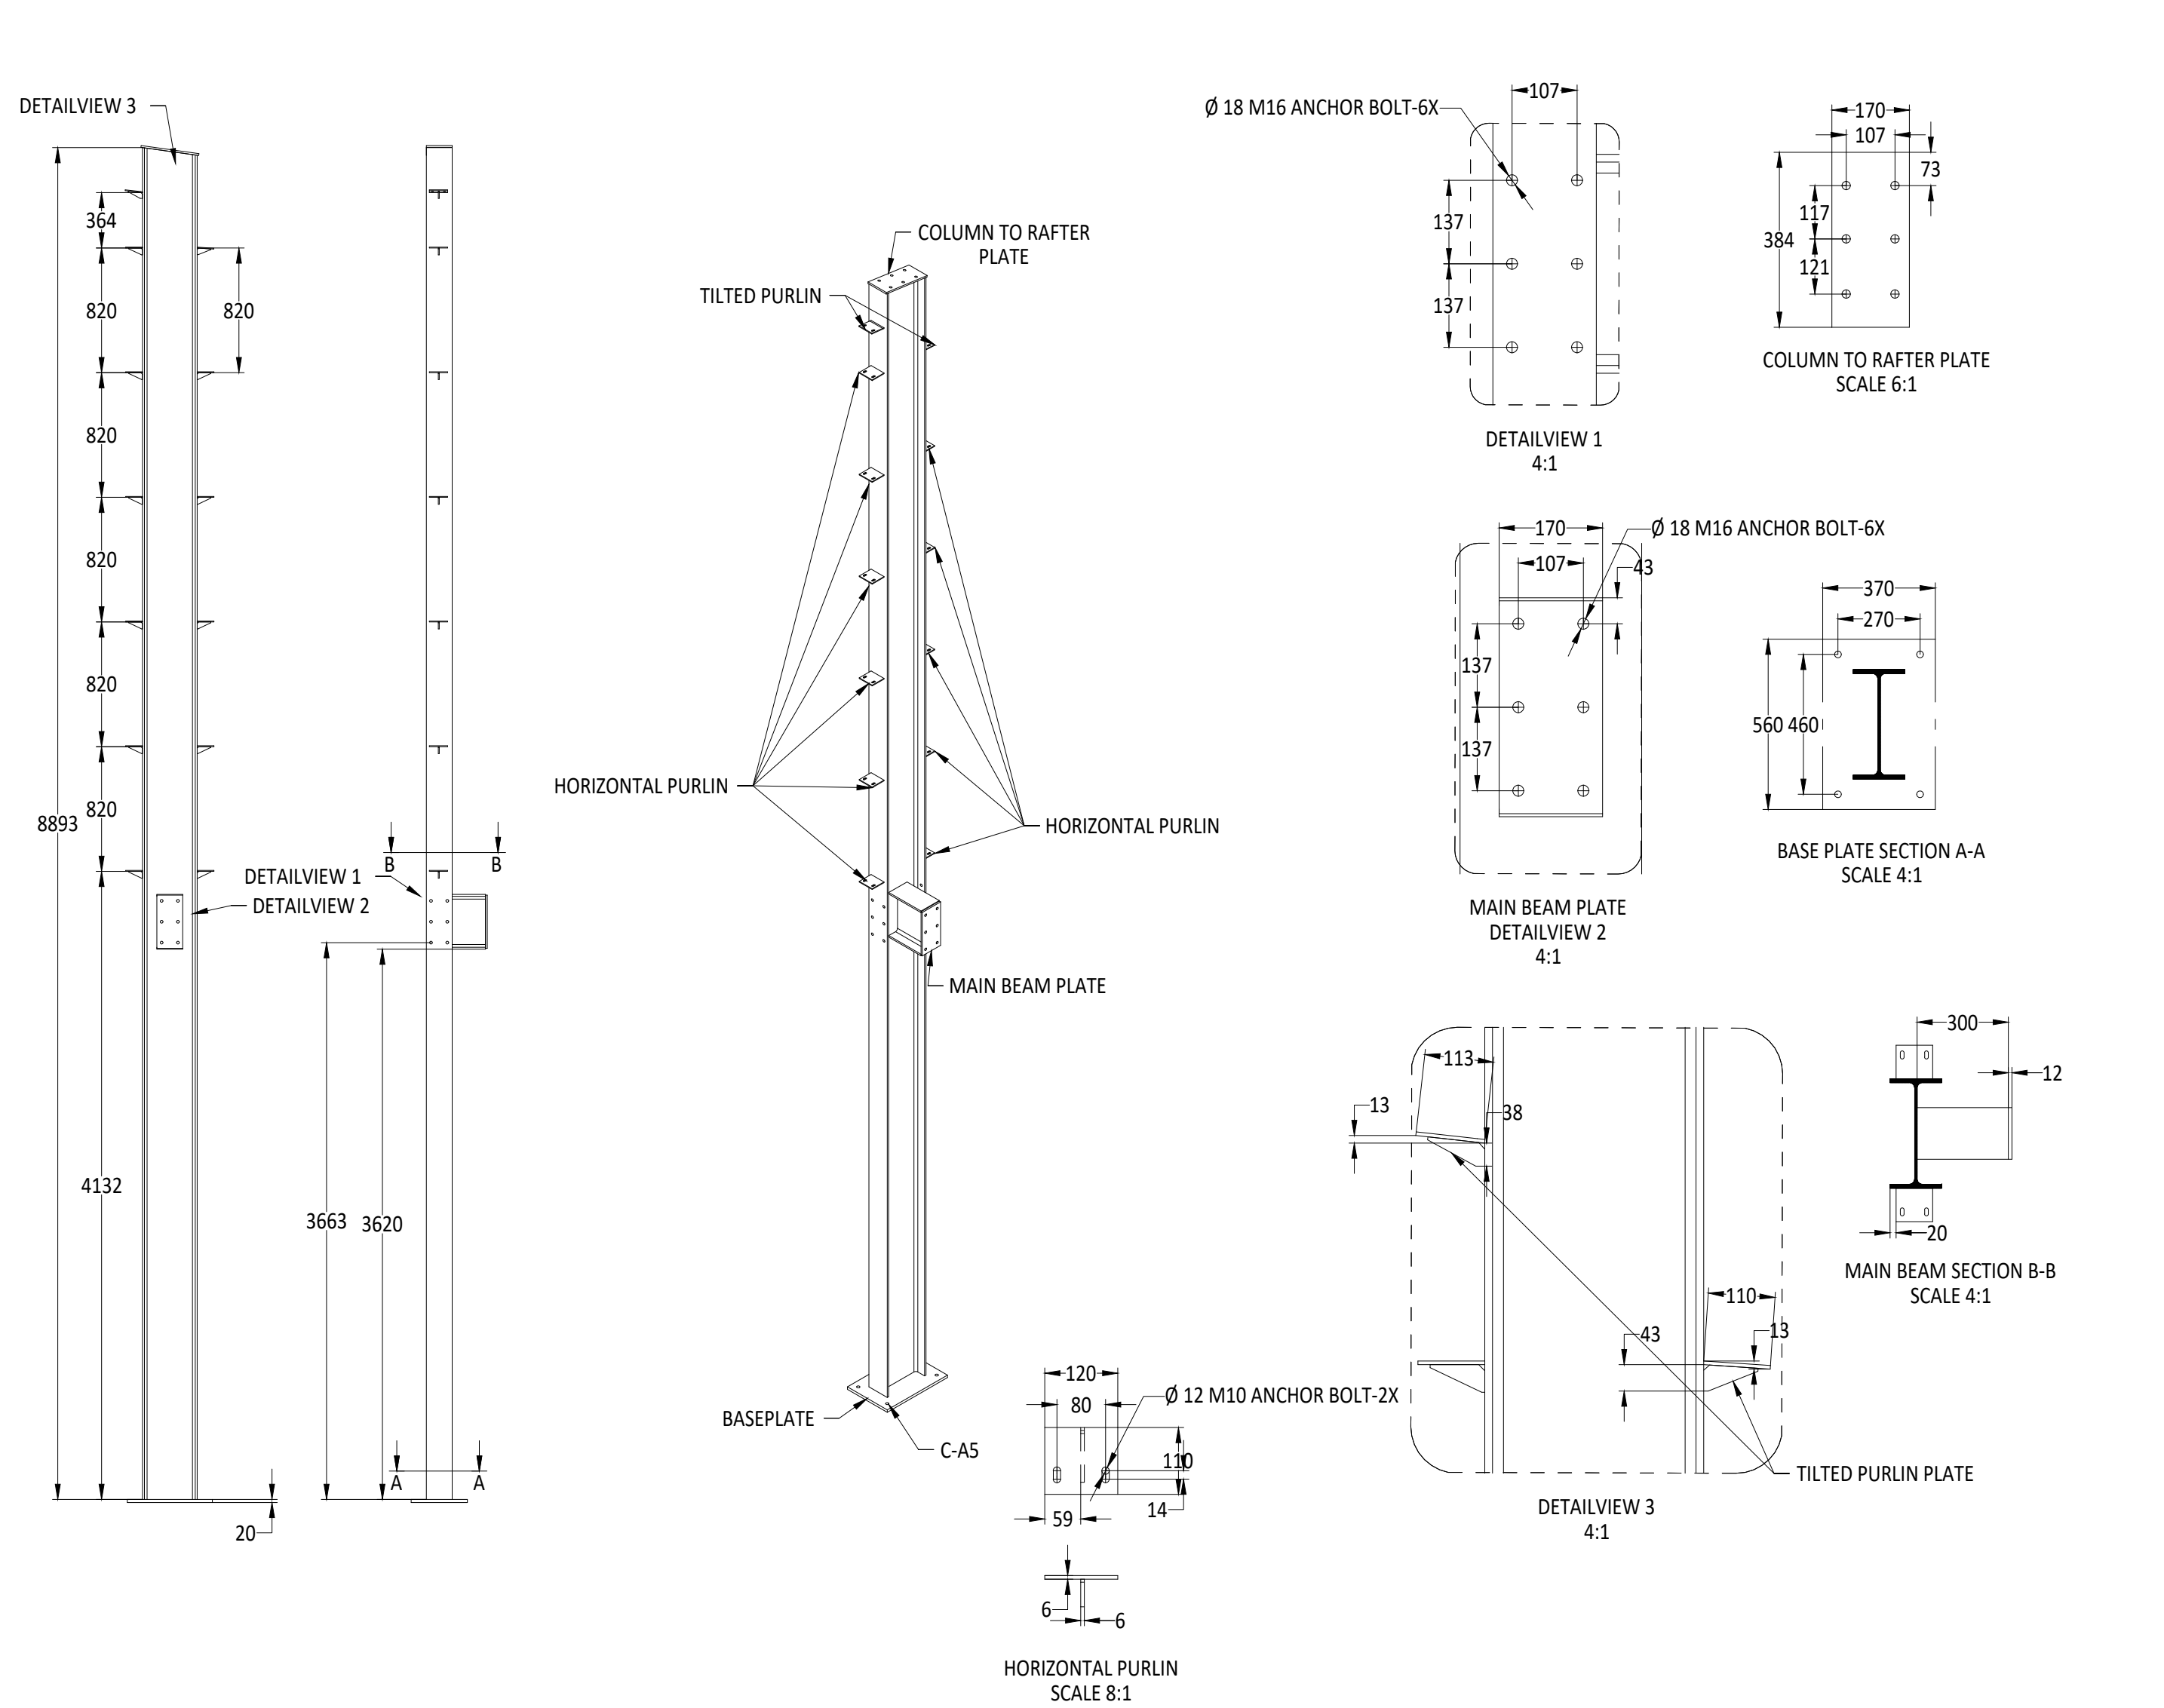


COLUMN C-A5 FABRICATION DETAILS

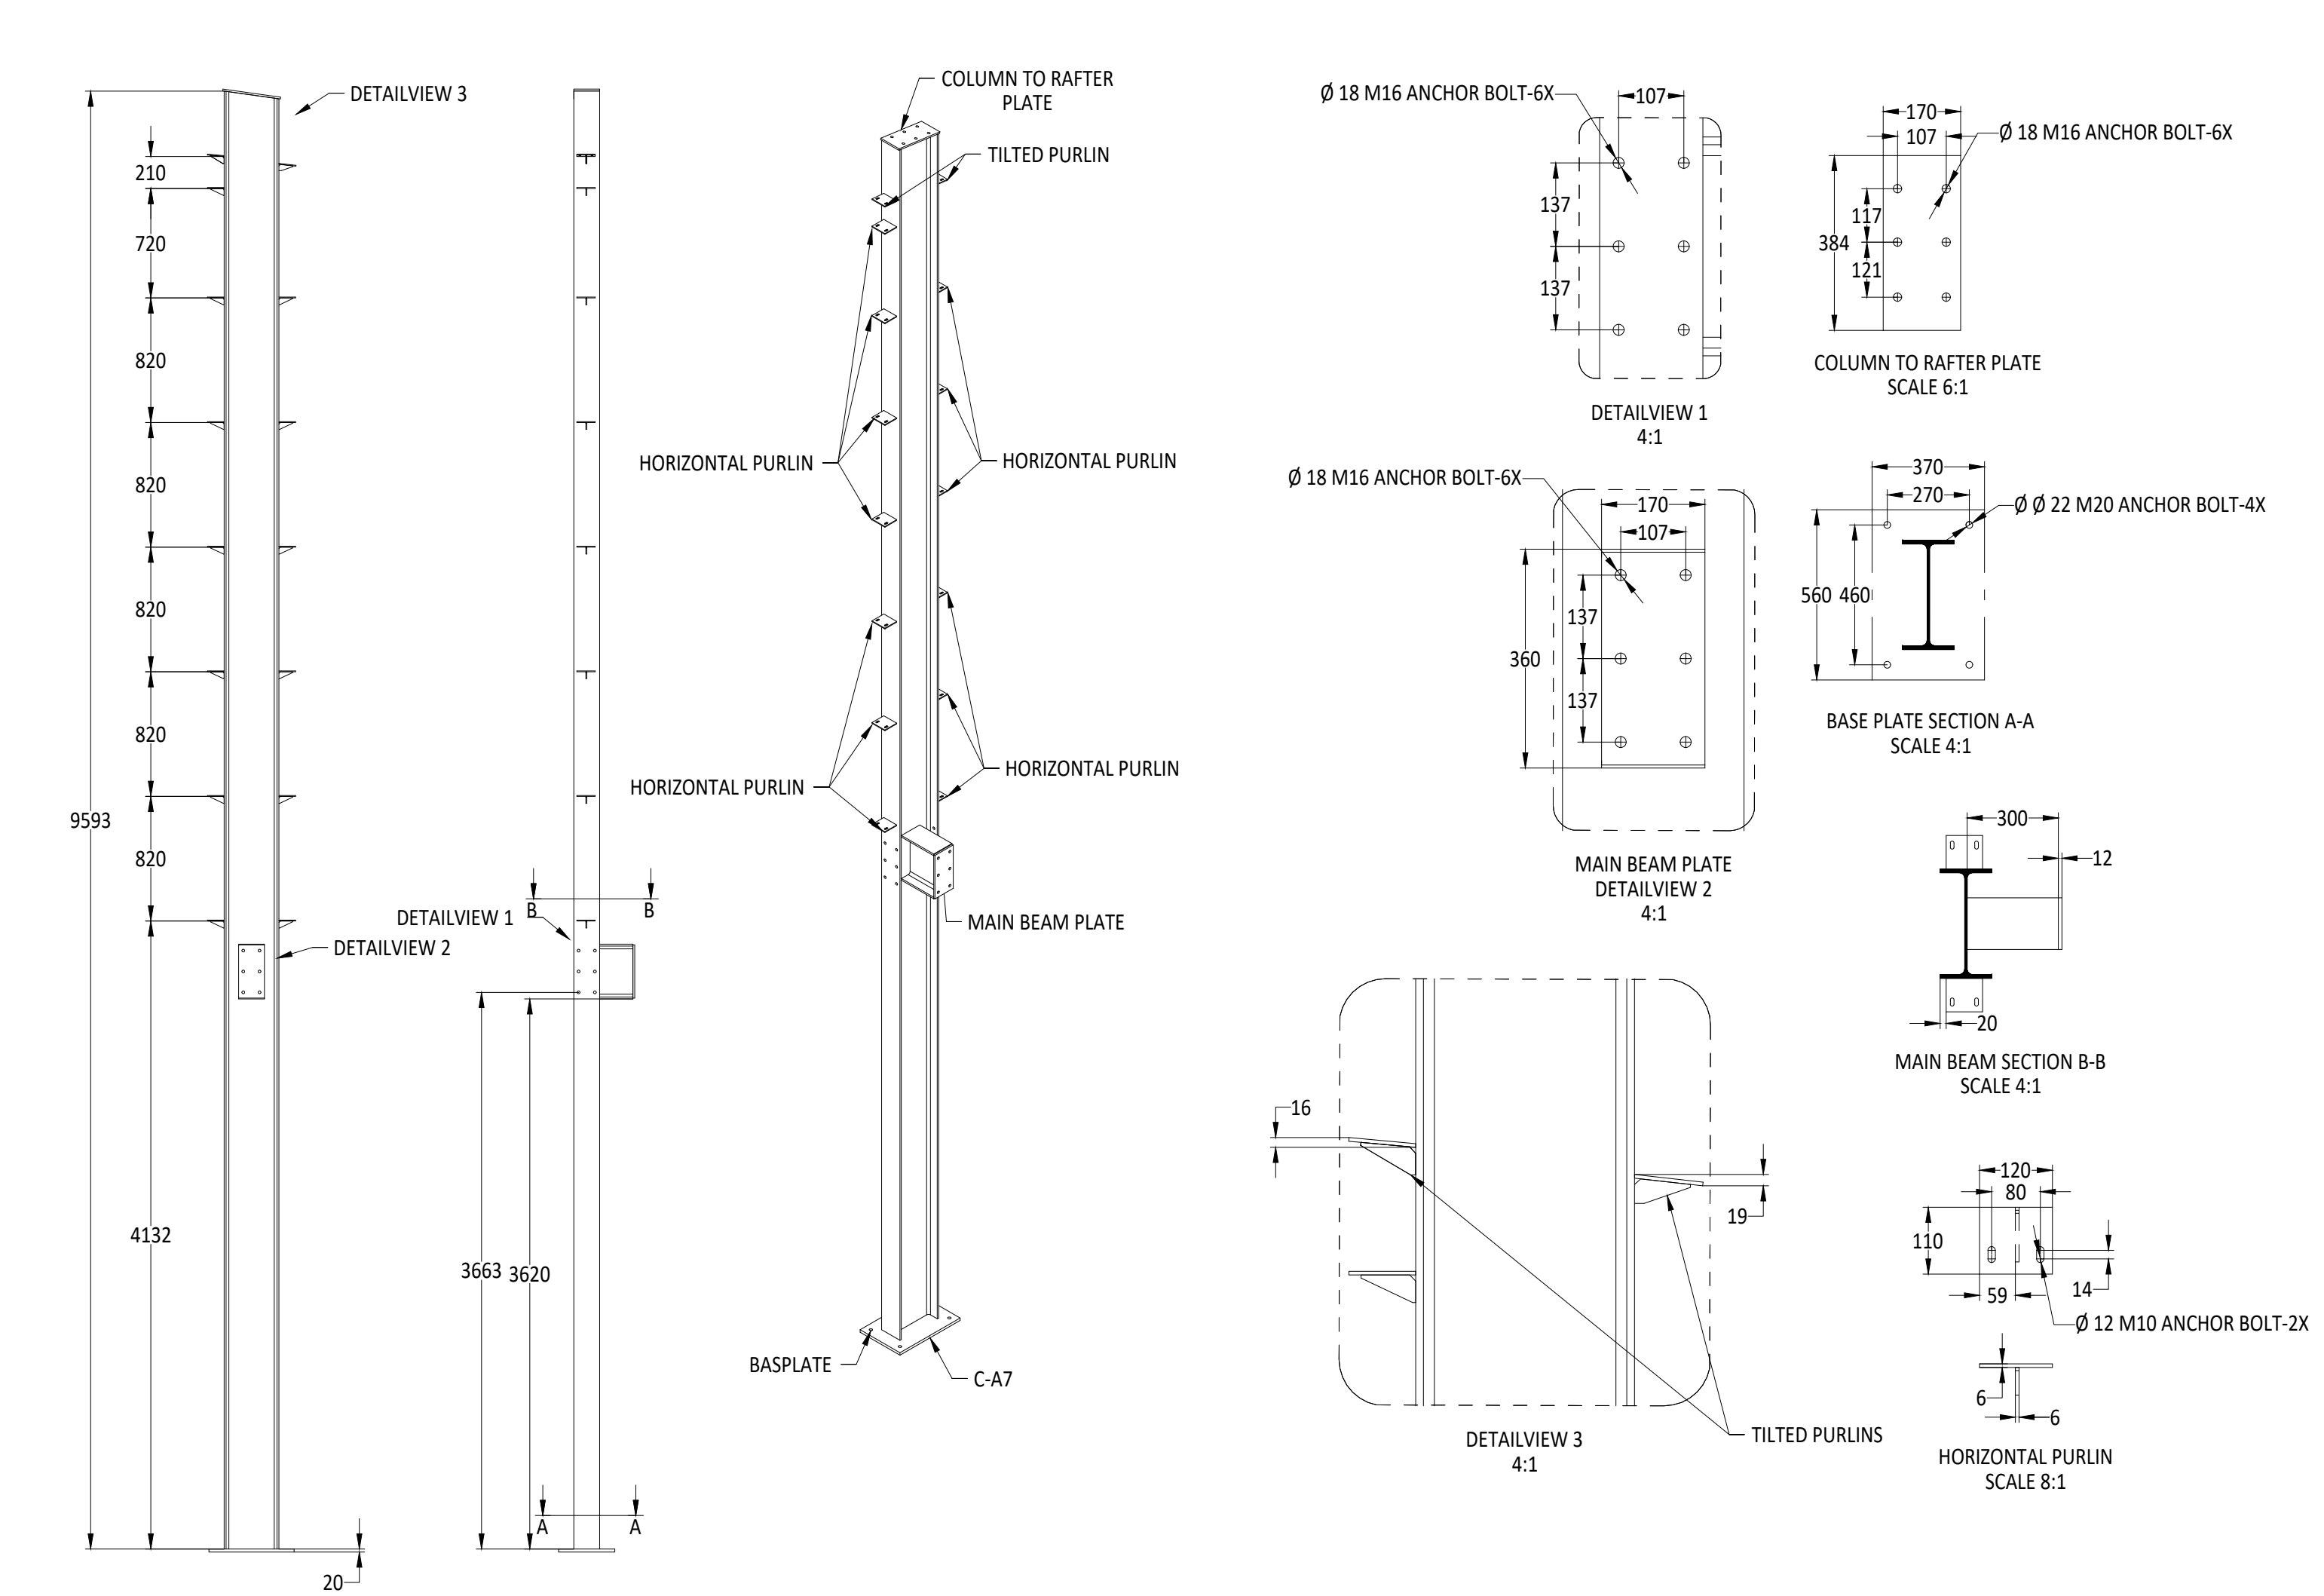

COLUMN C-A7 FABRICATION DETAILS

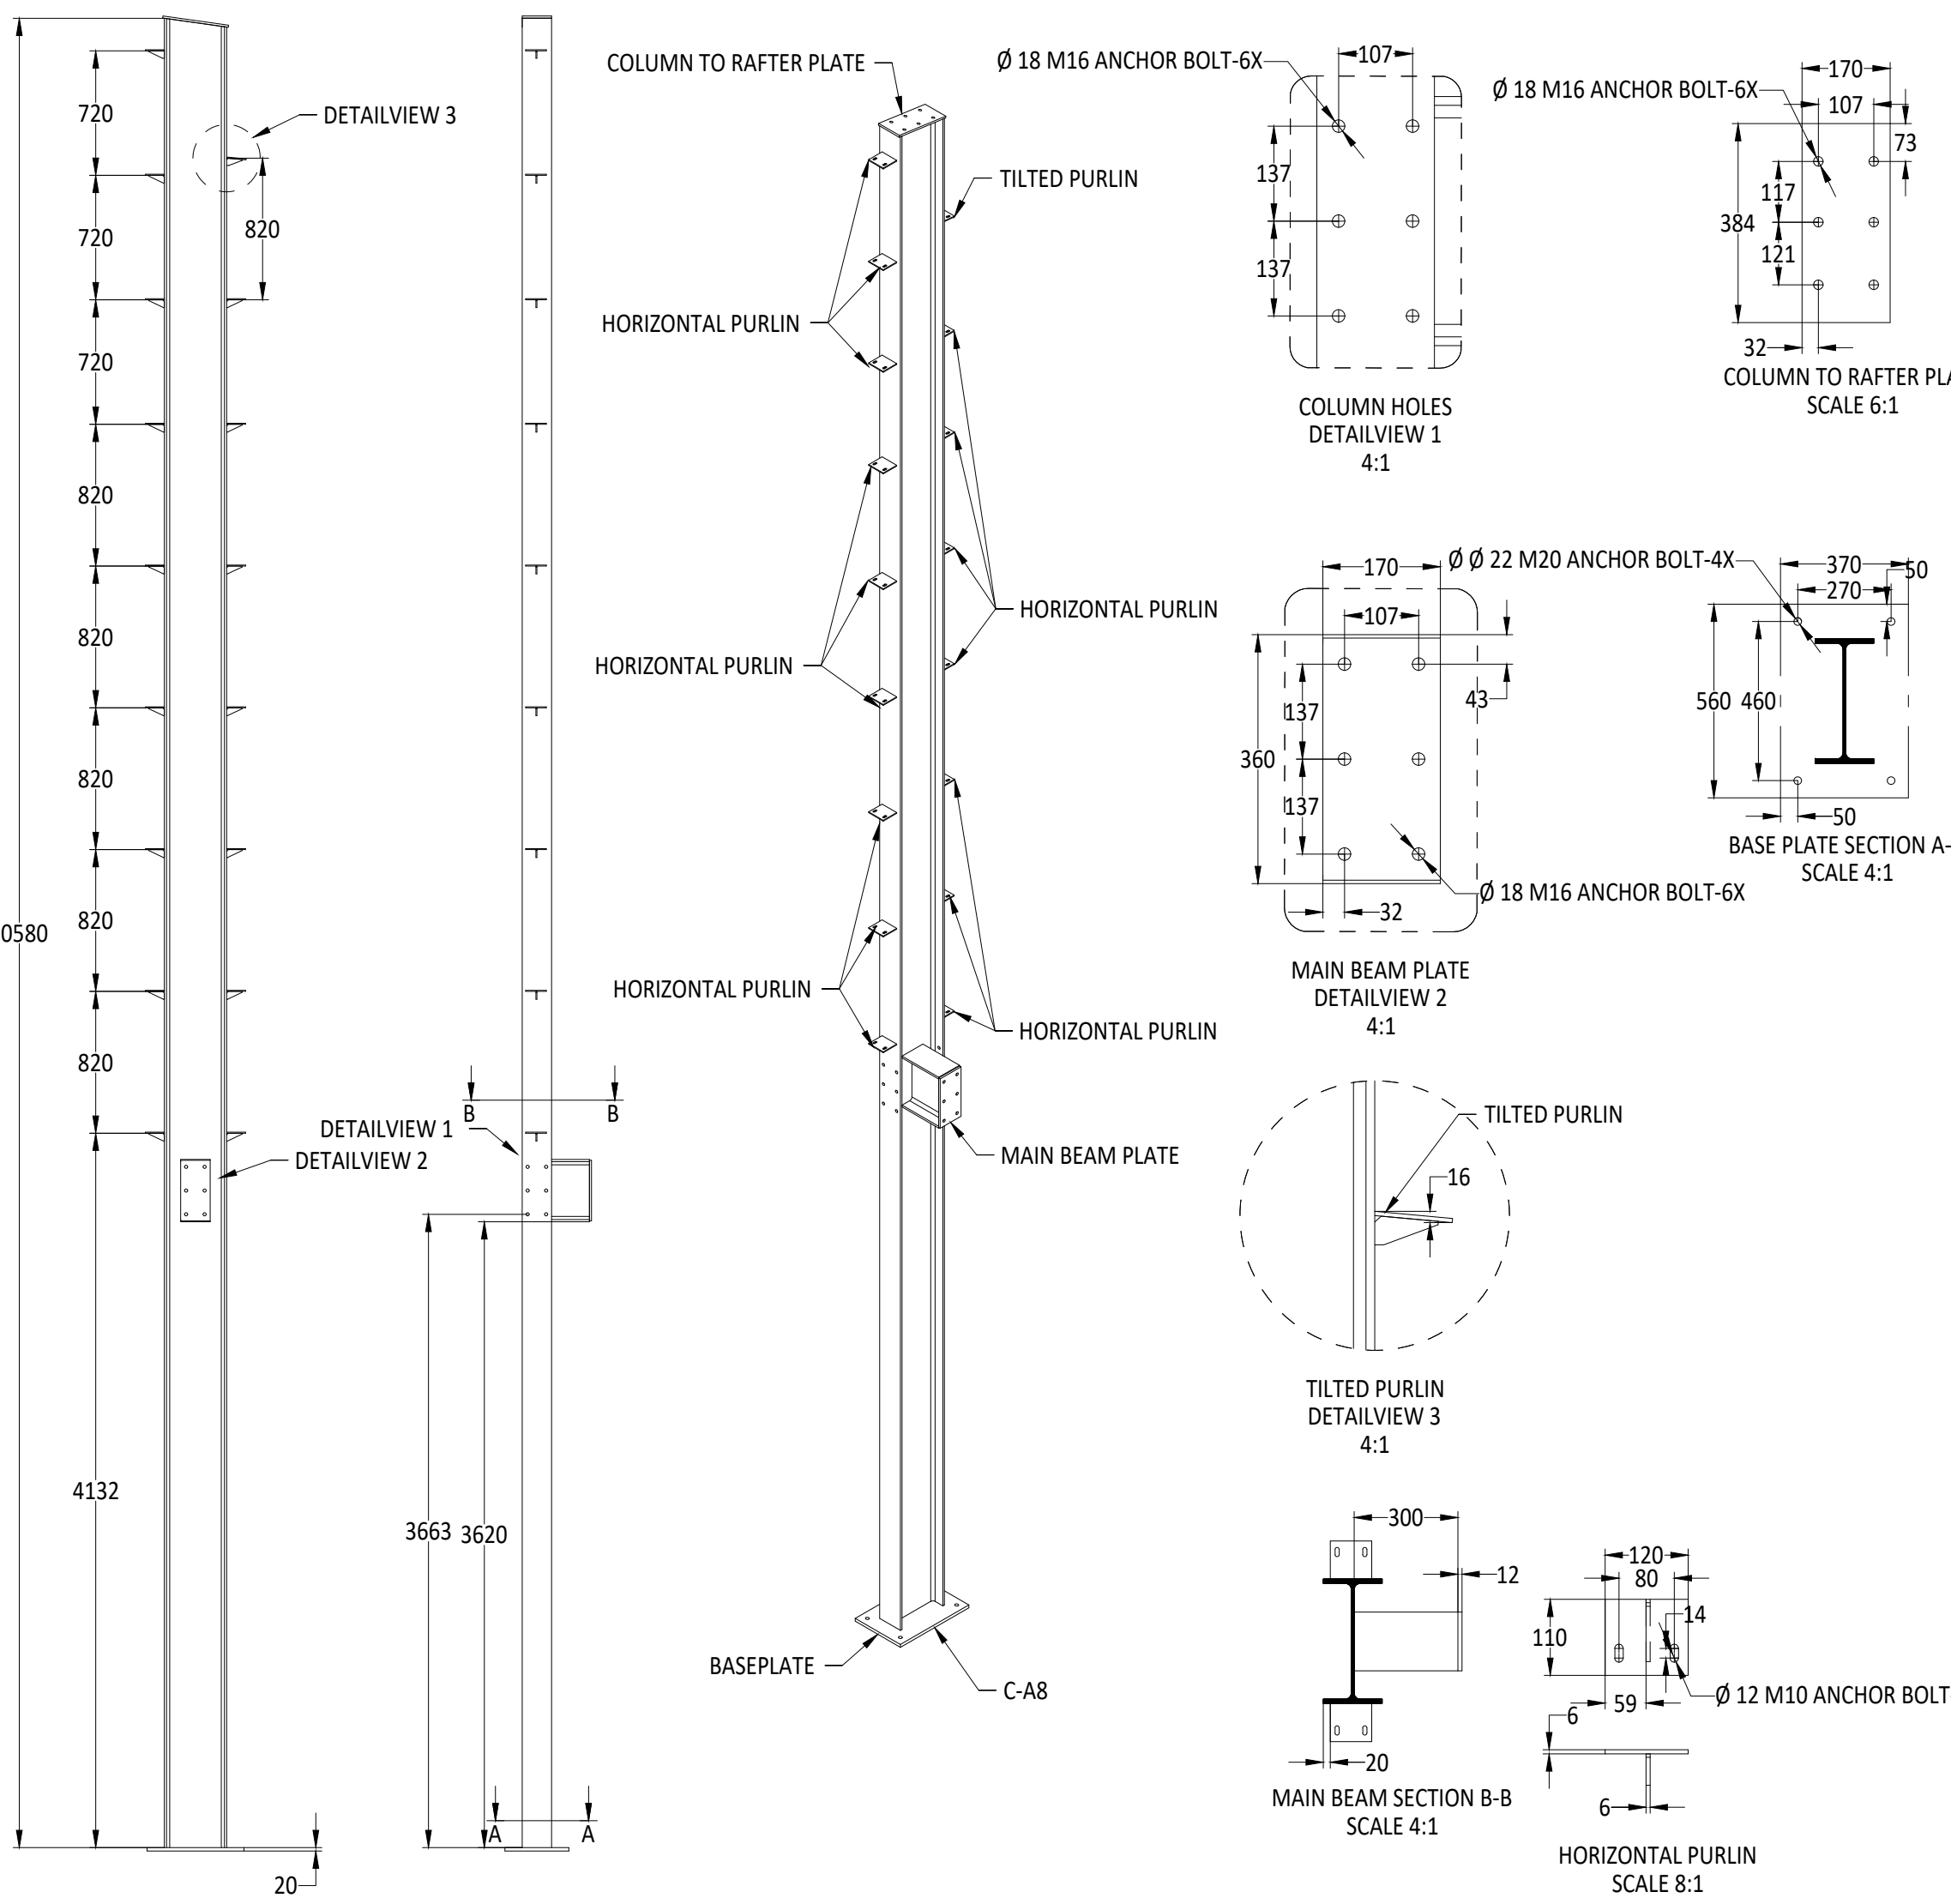


COLUMN C-A8 & C-A9 FABRICATION DETAILS
FRAME-A FABRICATION DETAILS

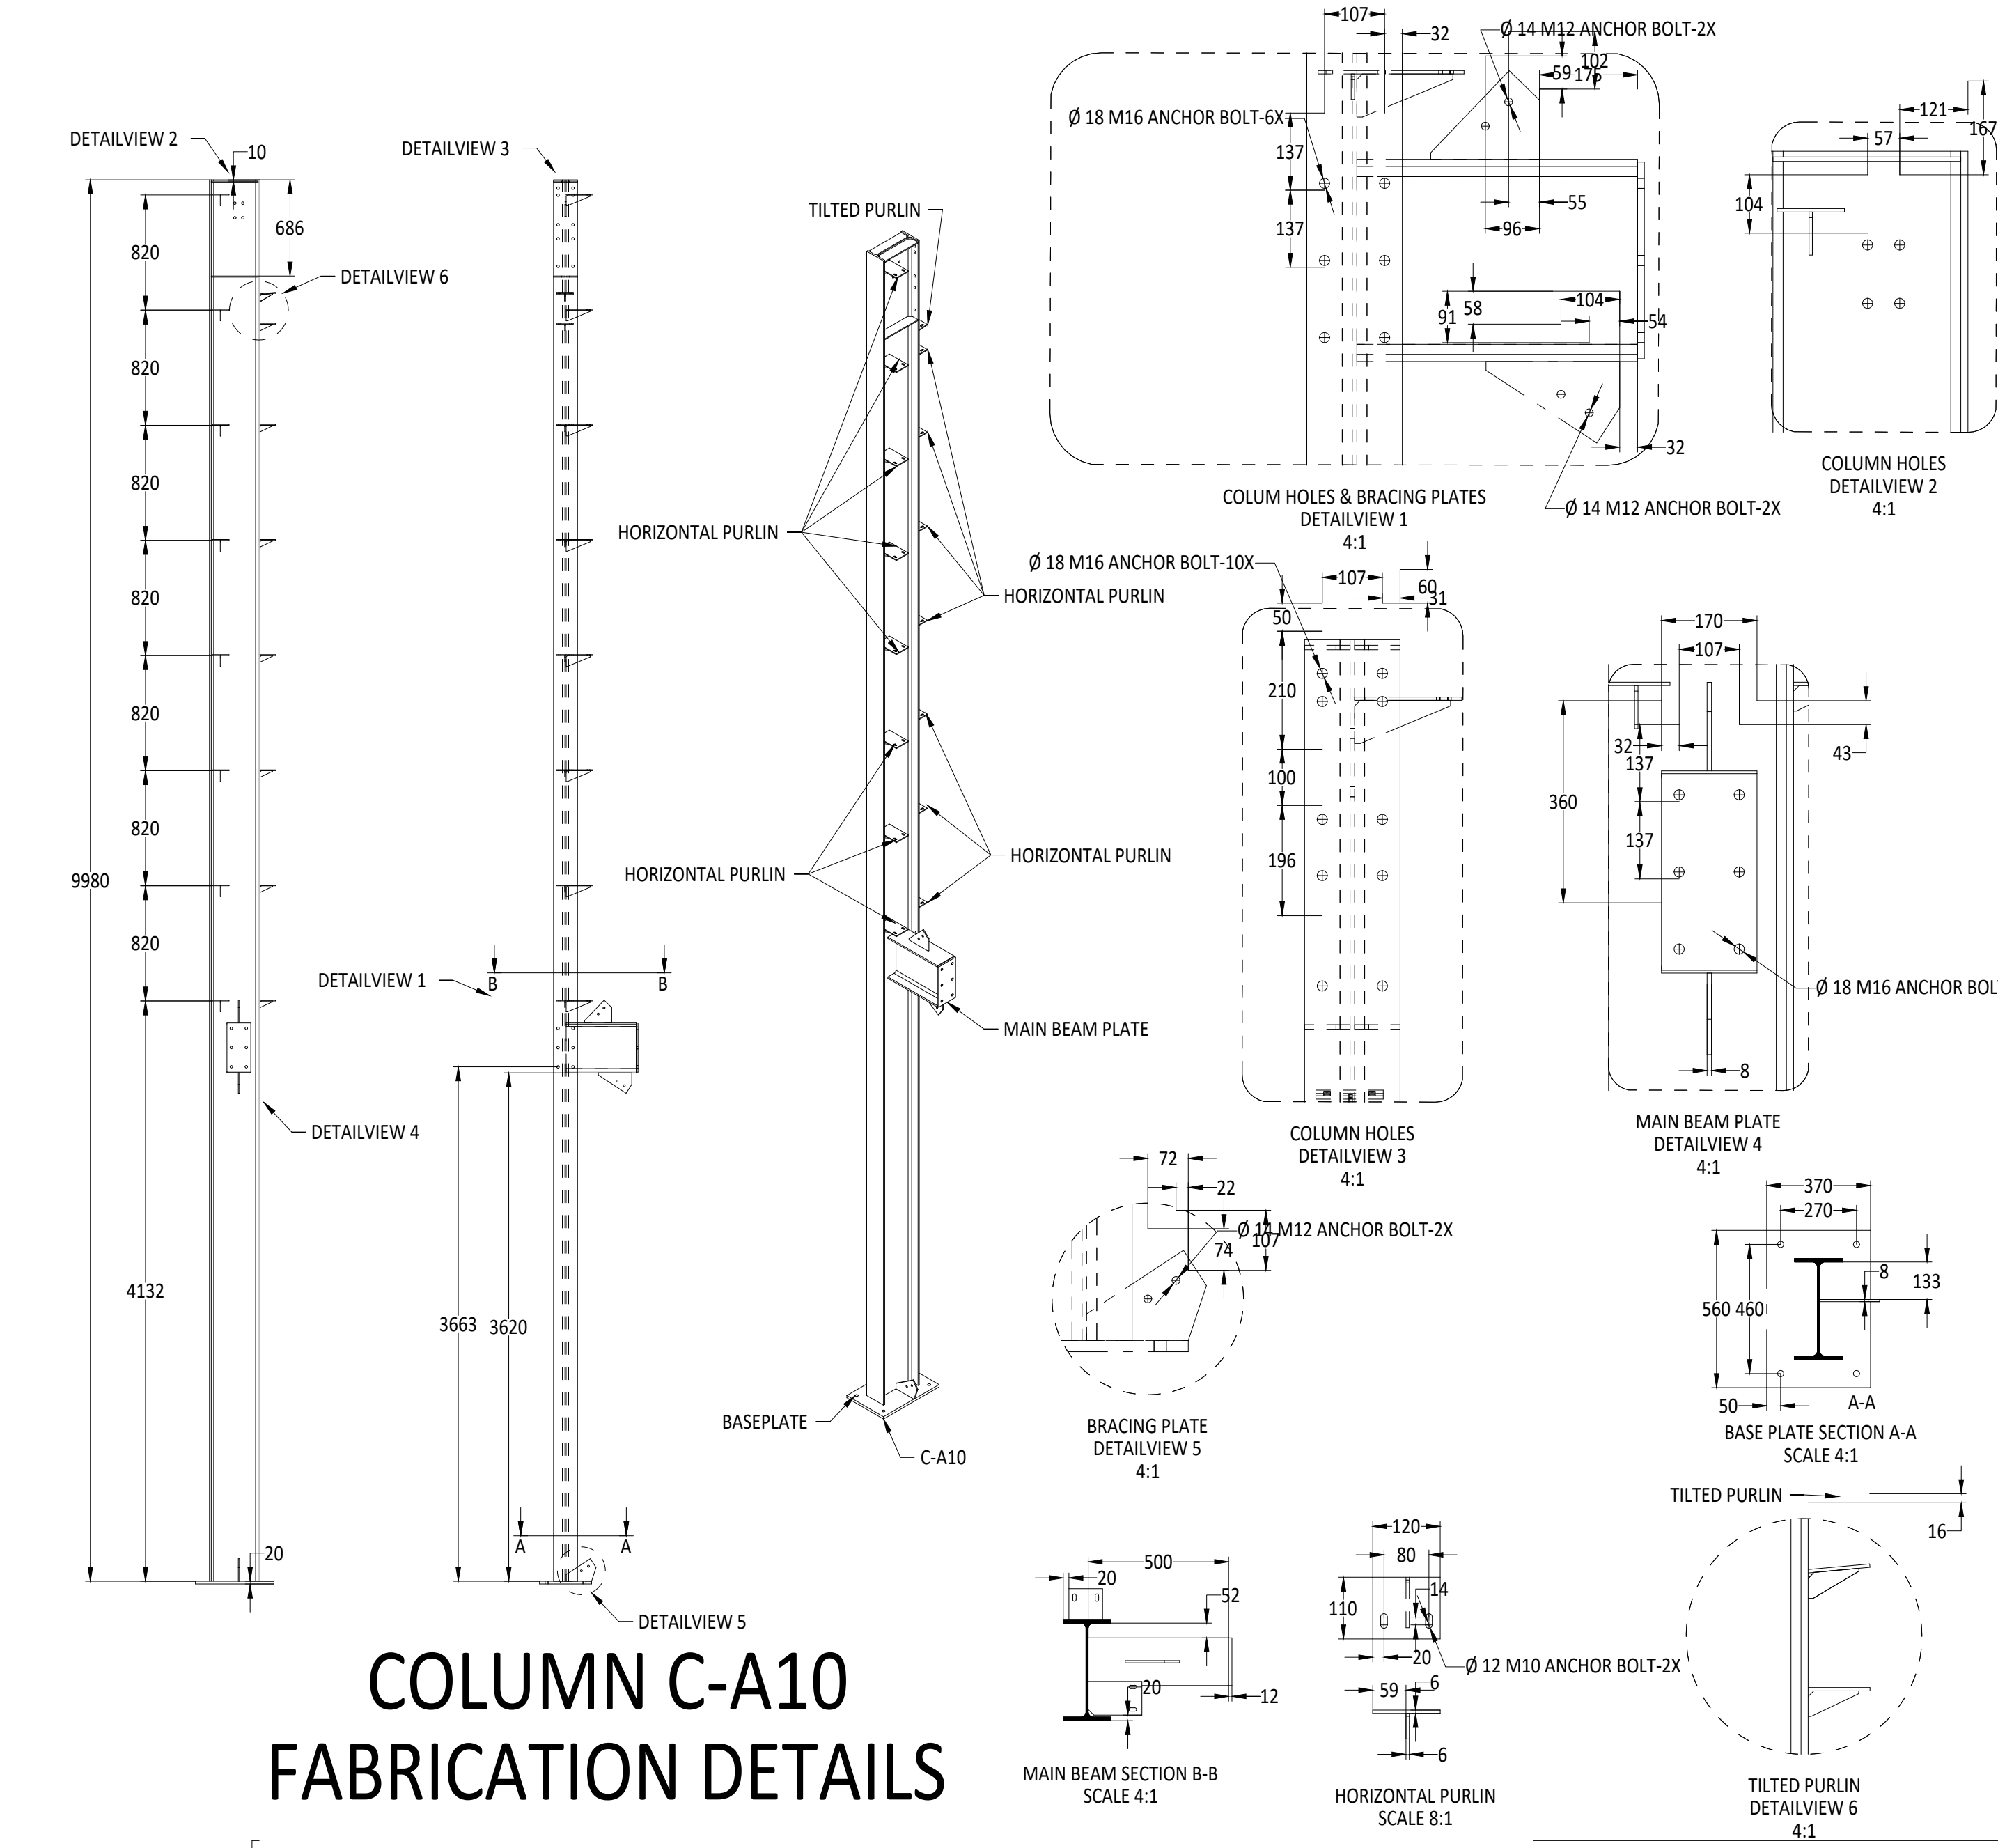


COLUMN C-A10
FABRICATION DETAILS

ASSEMBLY NO.		TITLE HANGER FRAME-A FABRICATION DETAILS			
PART NO.					
DESIGNER			SIZE A0	DWG NO	REV 00
			RELEASE DATE 21/08/2025	WEIGHT Kg.	QTY.
		APPROVED	SCALE AS SHOWN		


A
B
C
D
E
F
G
H
I
J
K
L

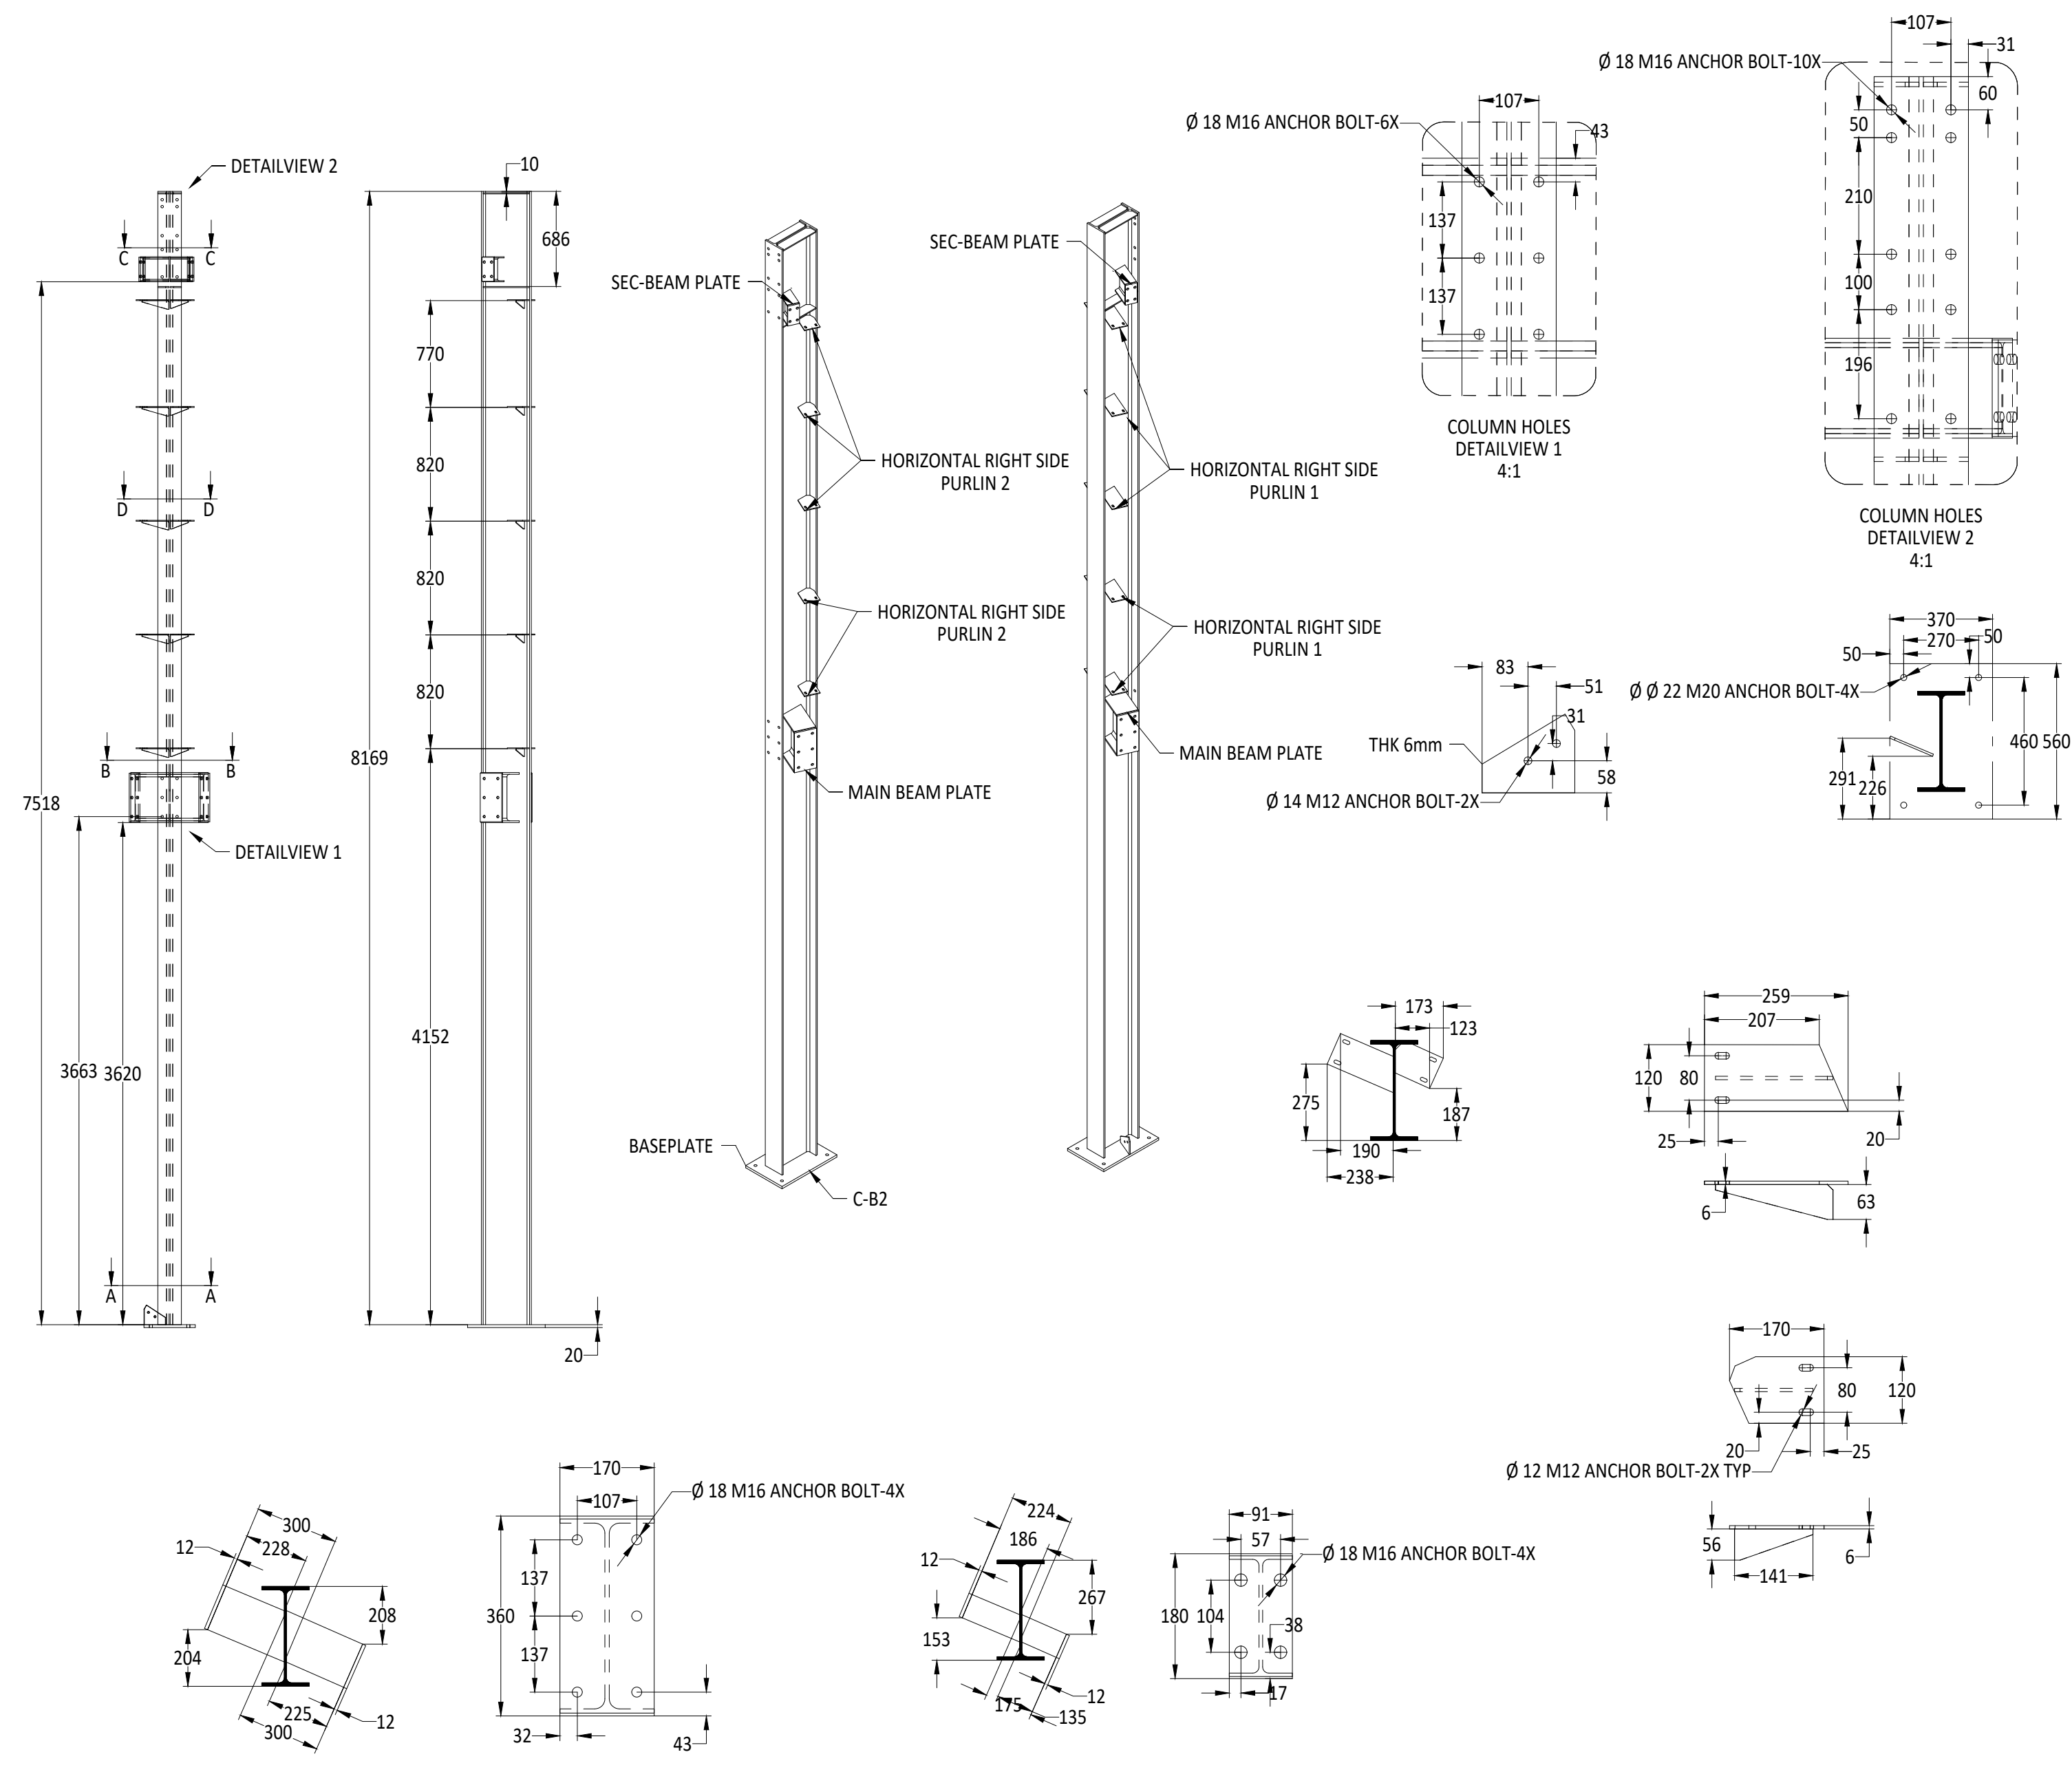


COLUMN C-B2 FABRICATION DETAILS

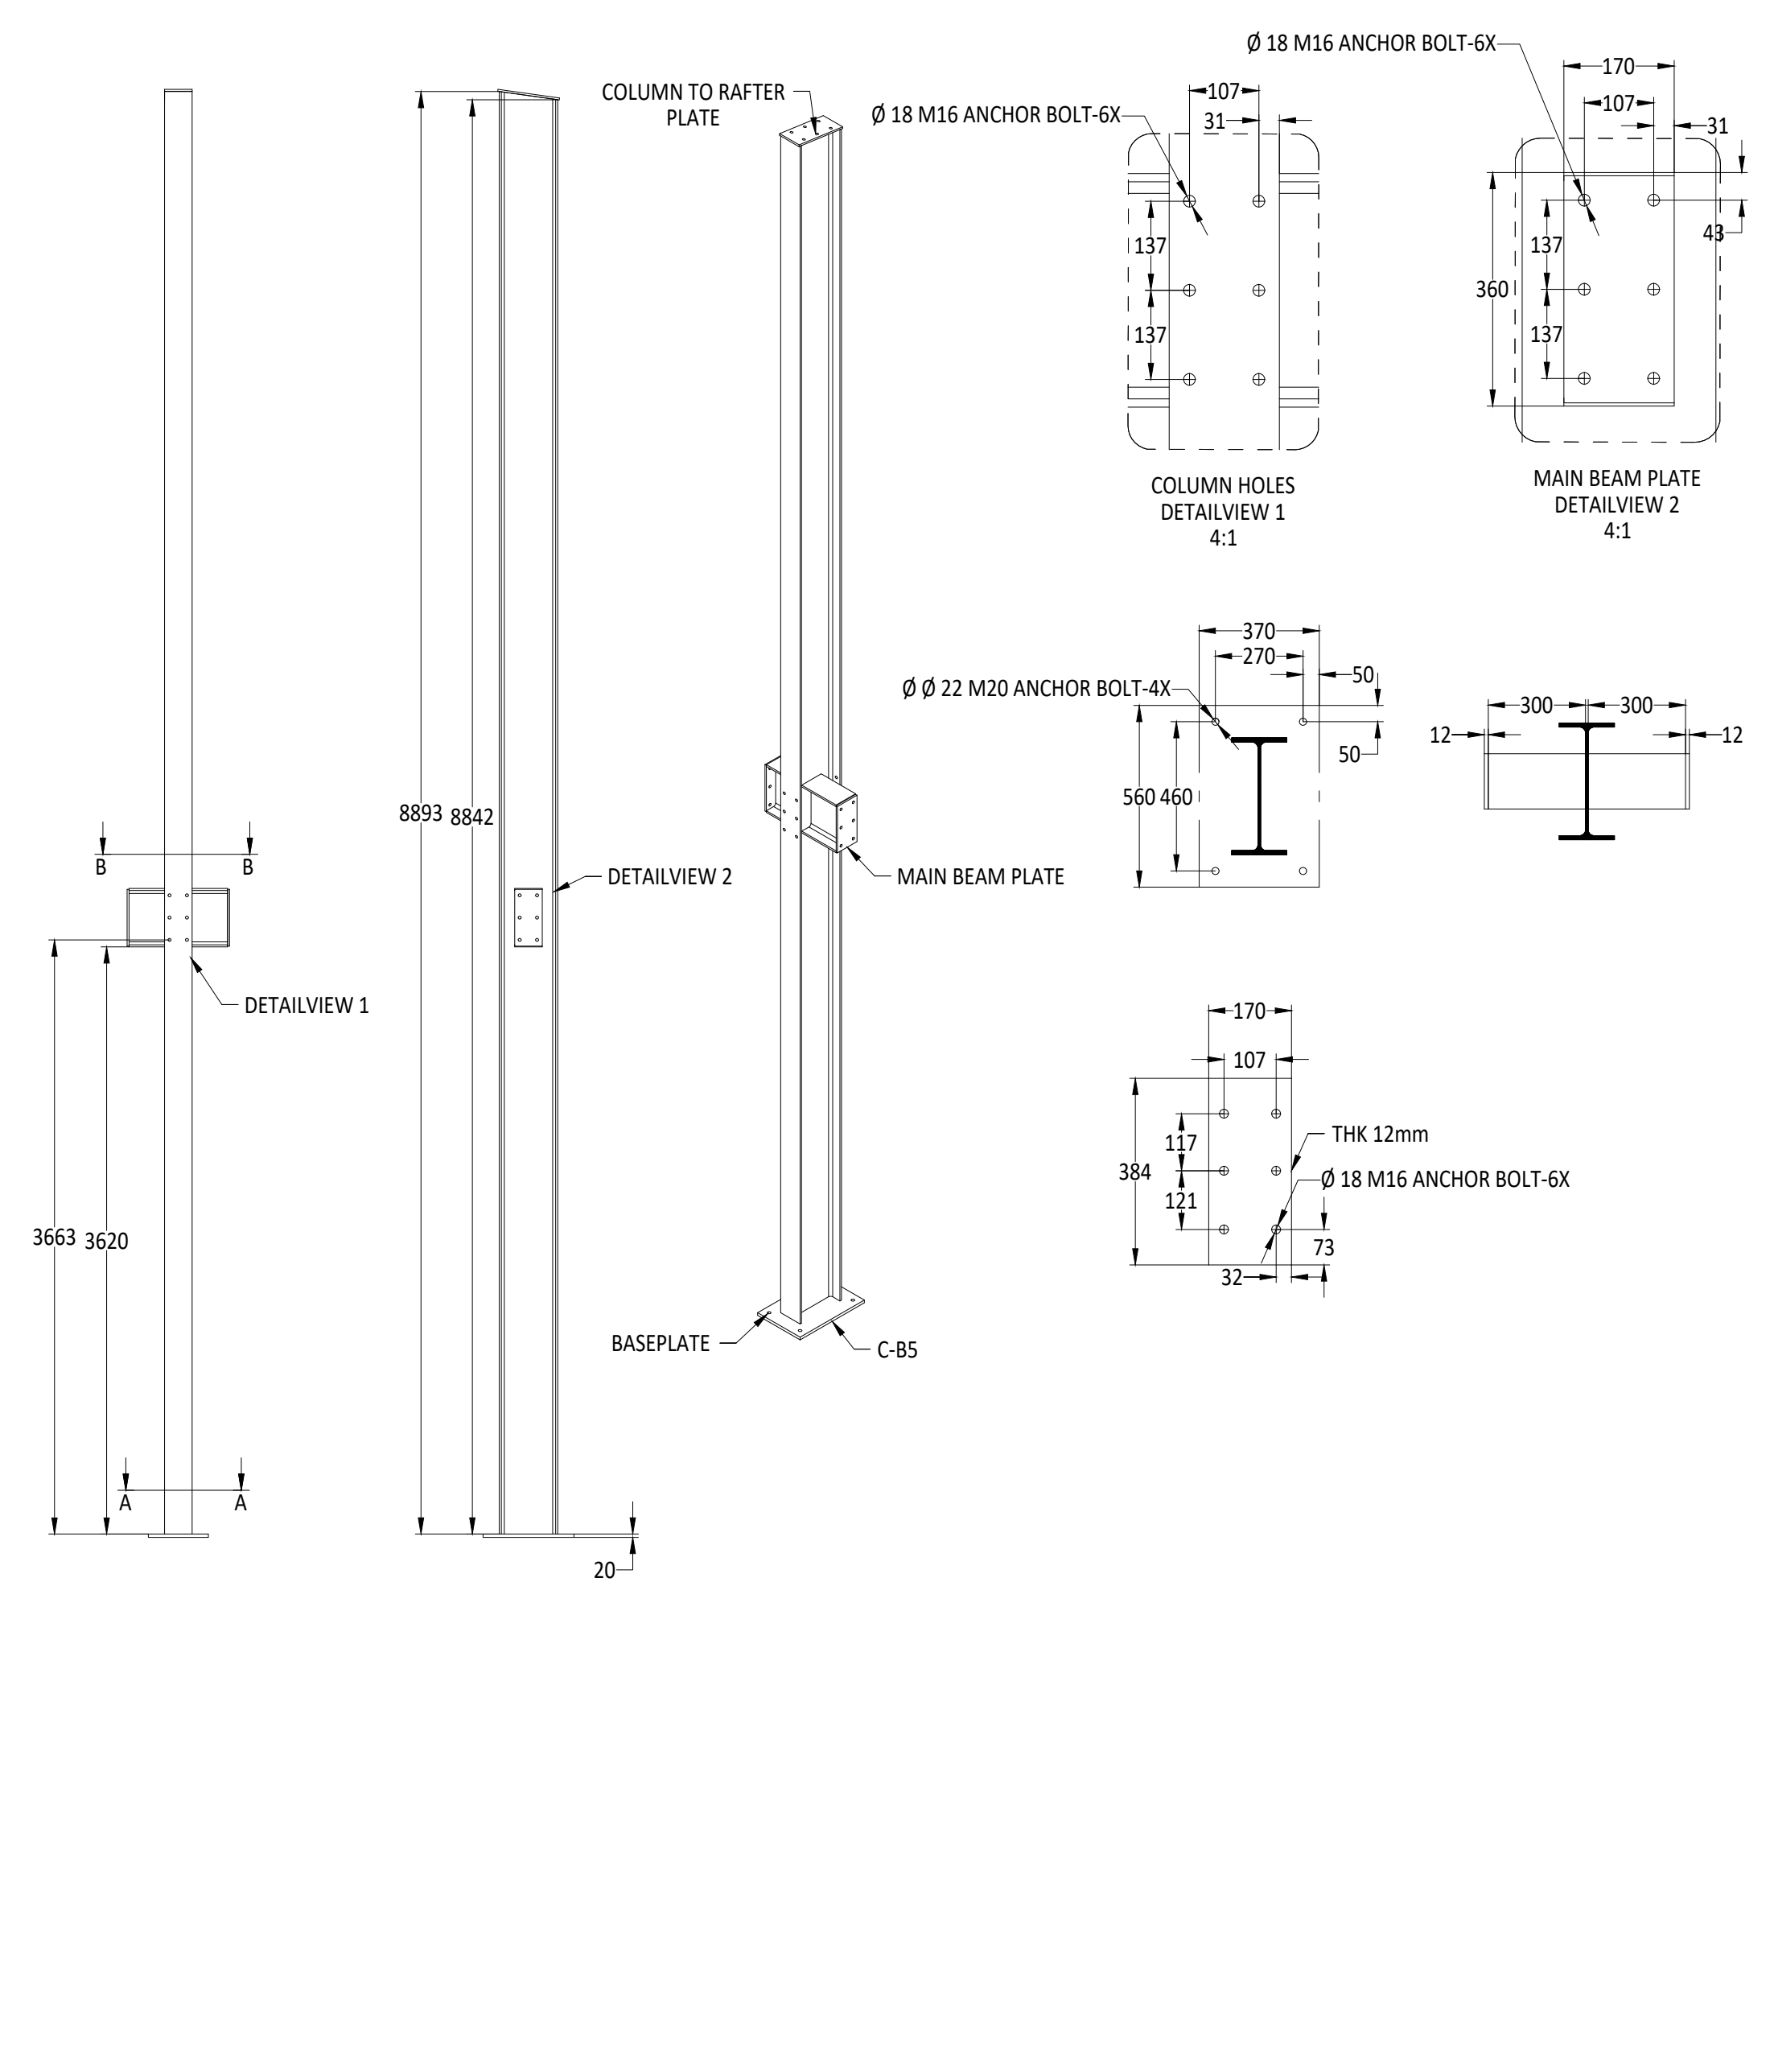


COLUMN C-B5 FABRICATION DETAILS

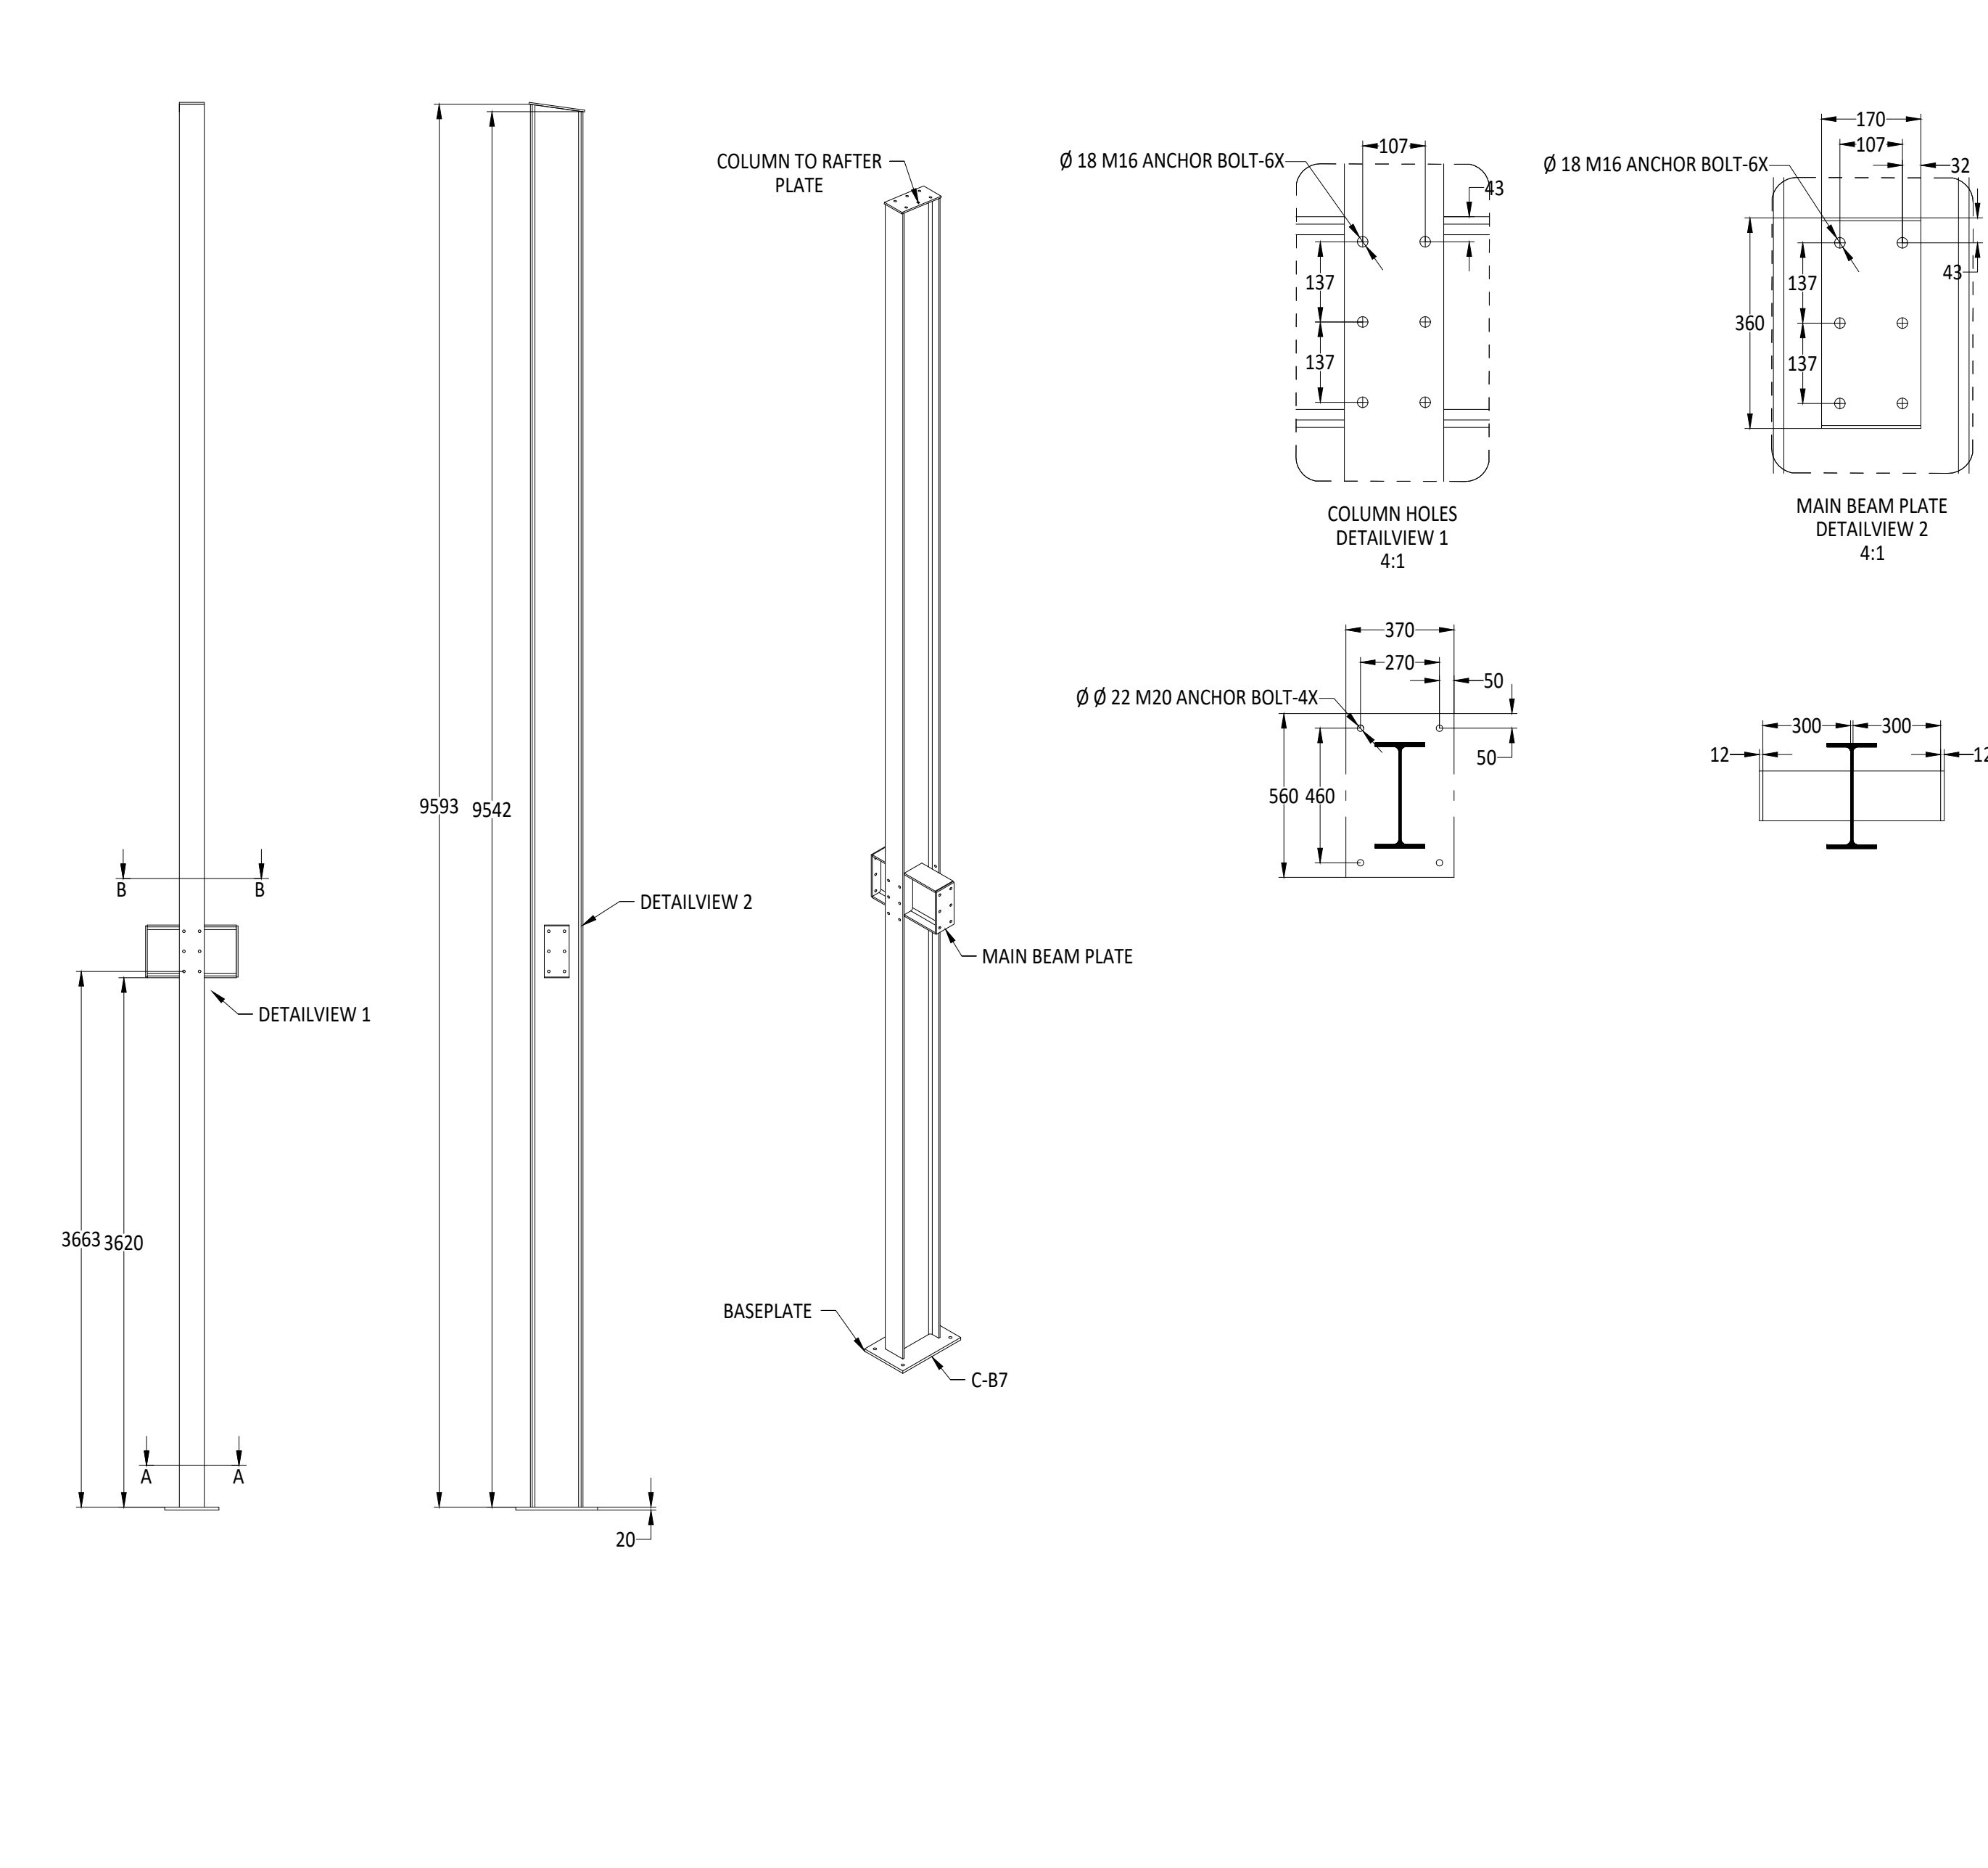


COLUMN C-B7 FABRICATION DETAILS

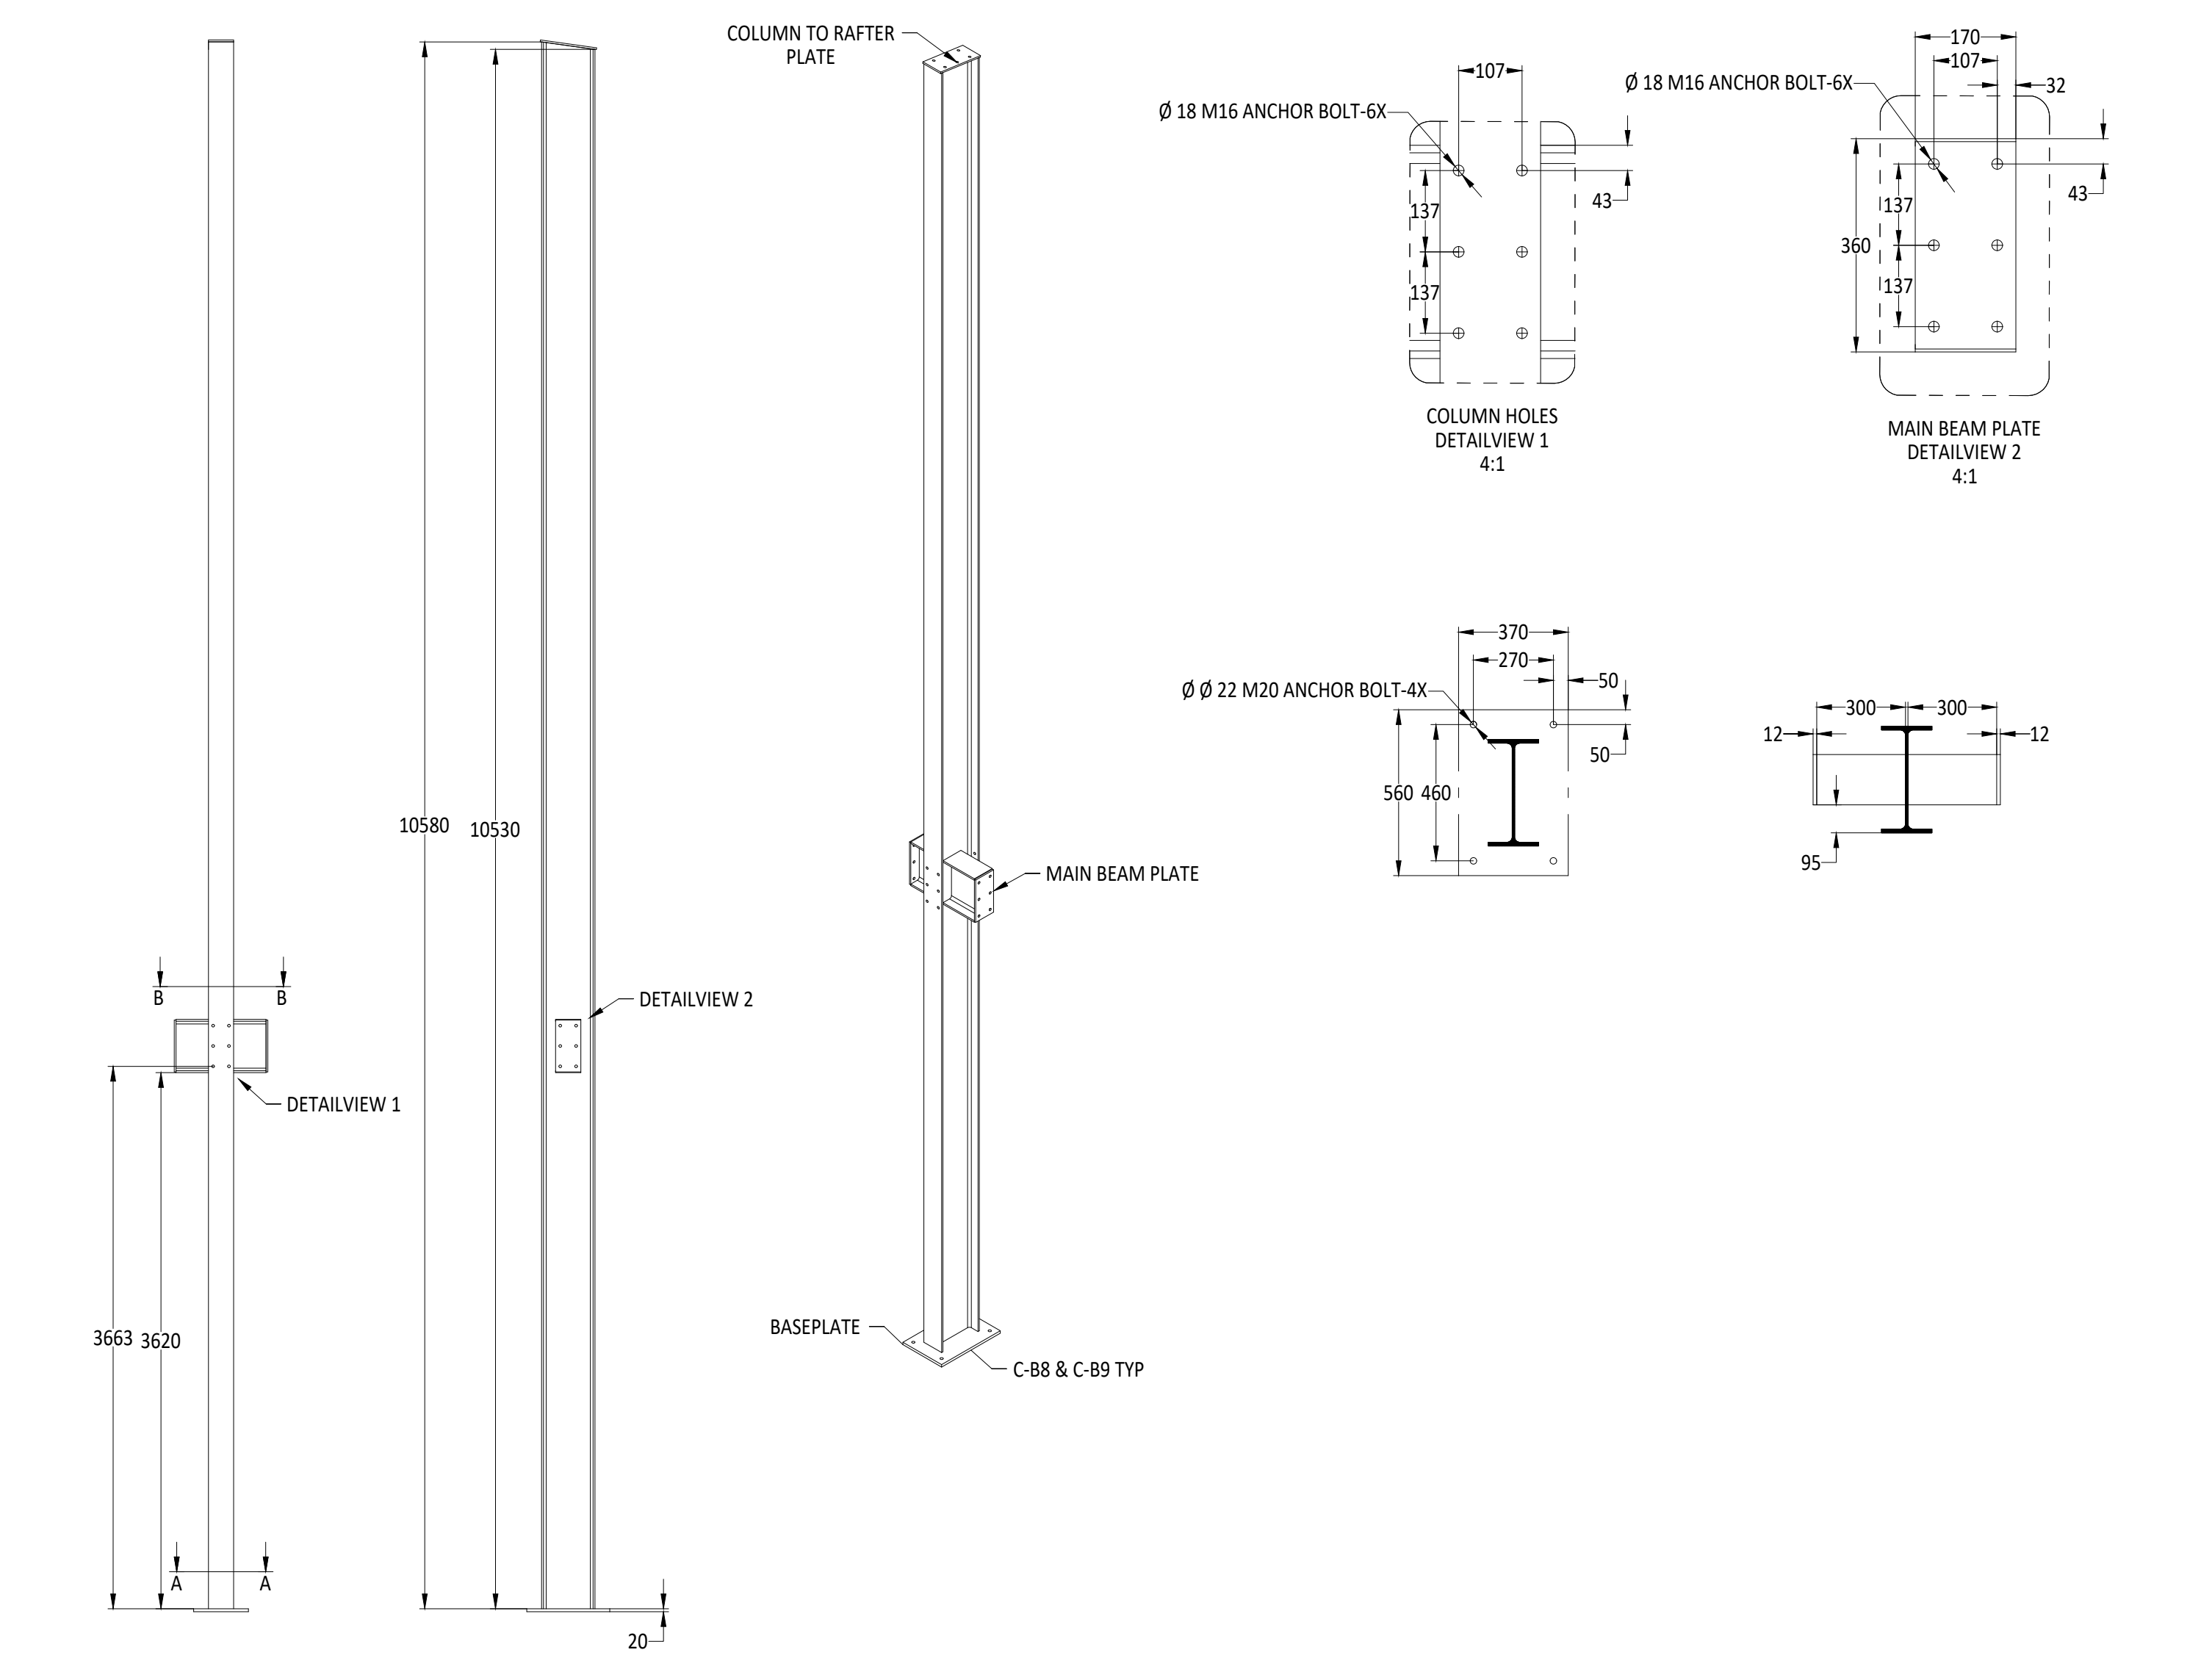

COLUMN C-B8 & C-B9 FABRICATION DETAILS

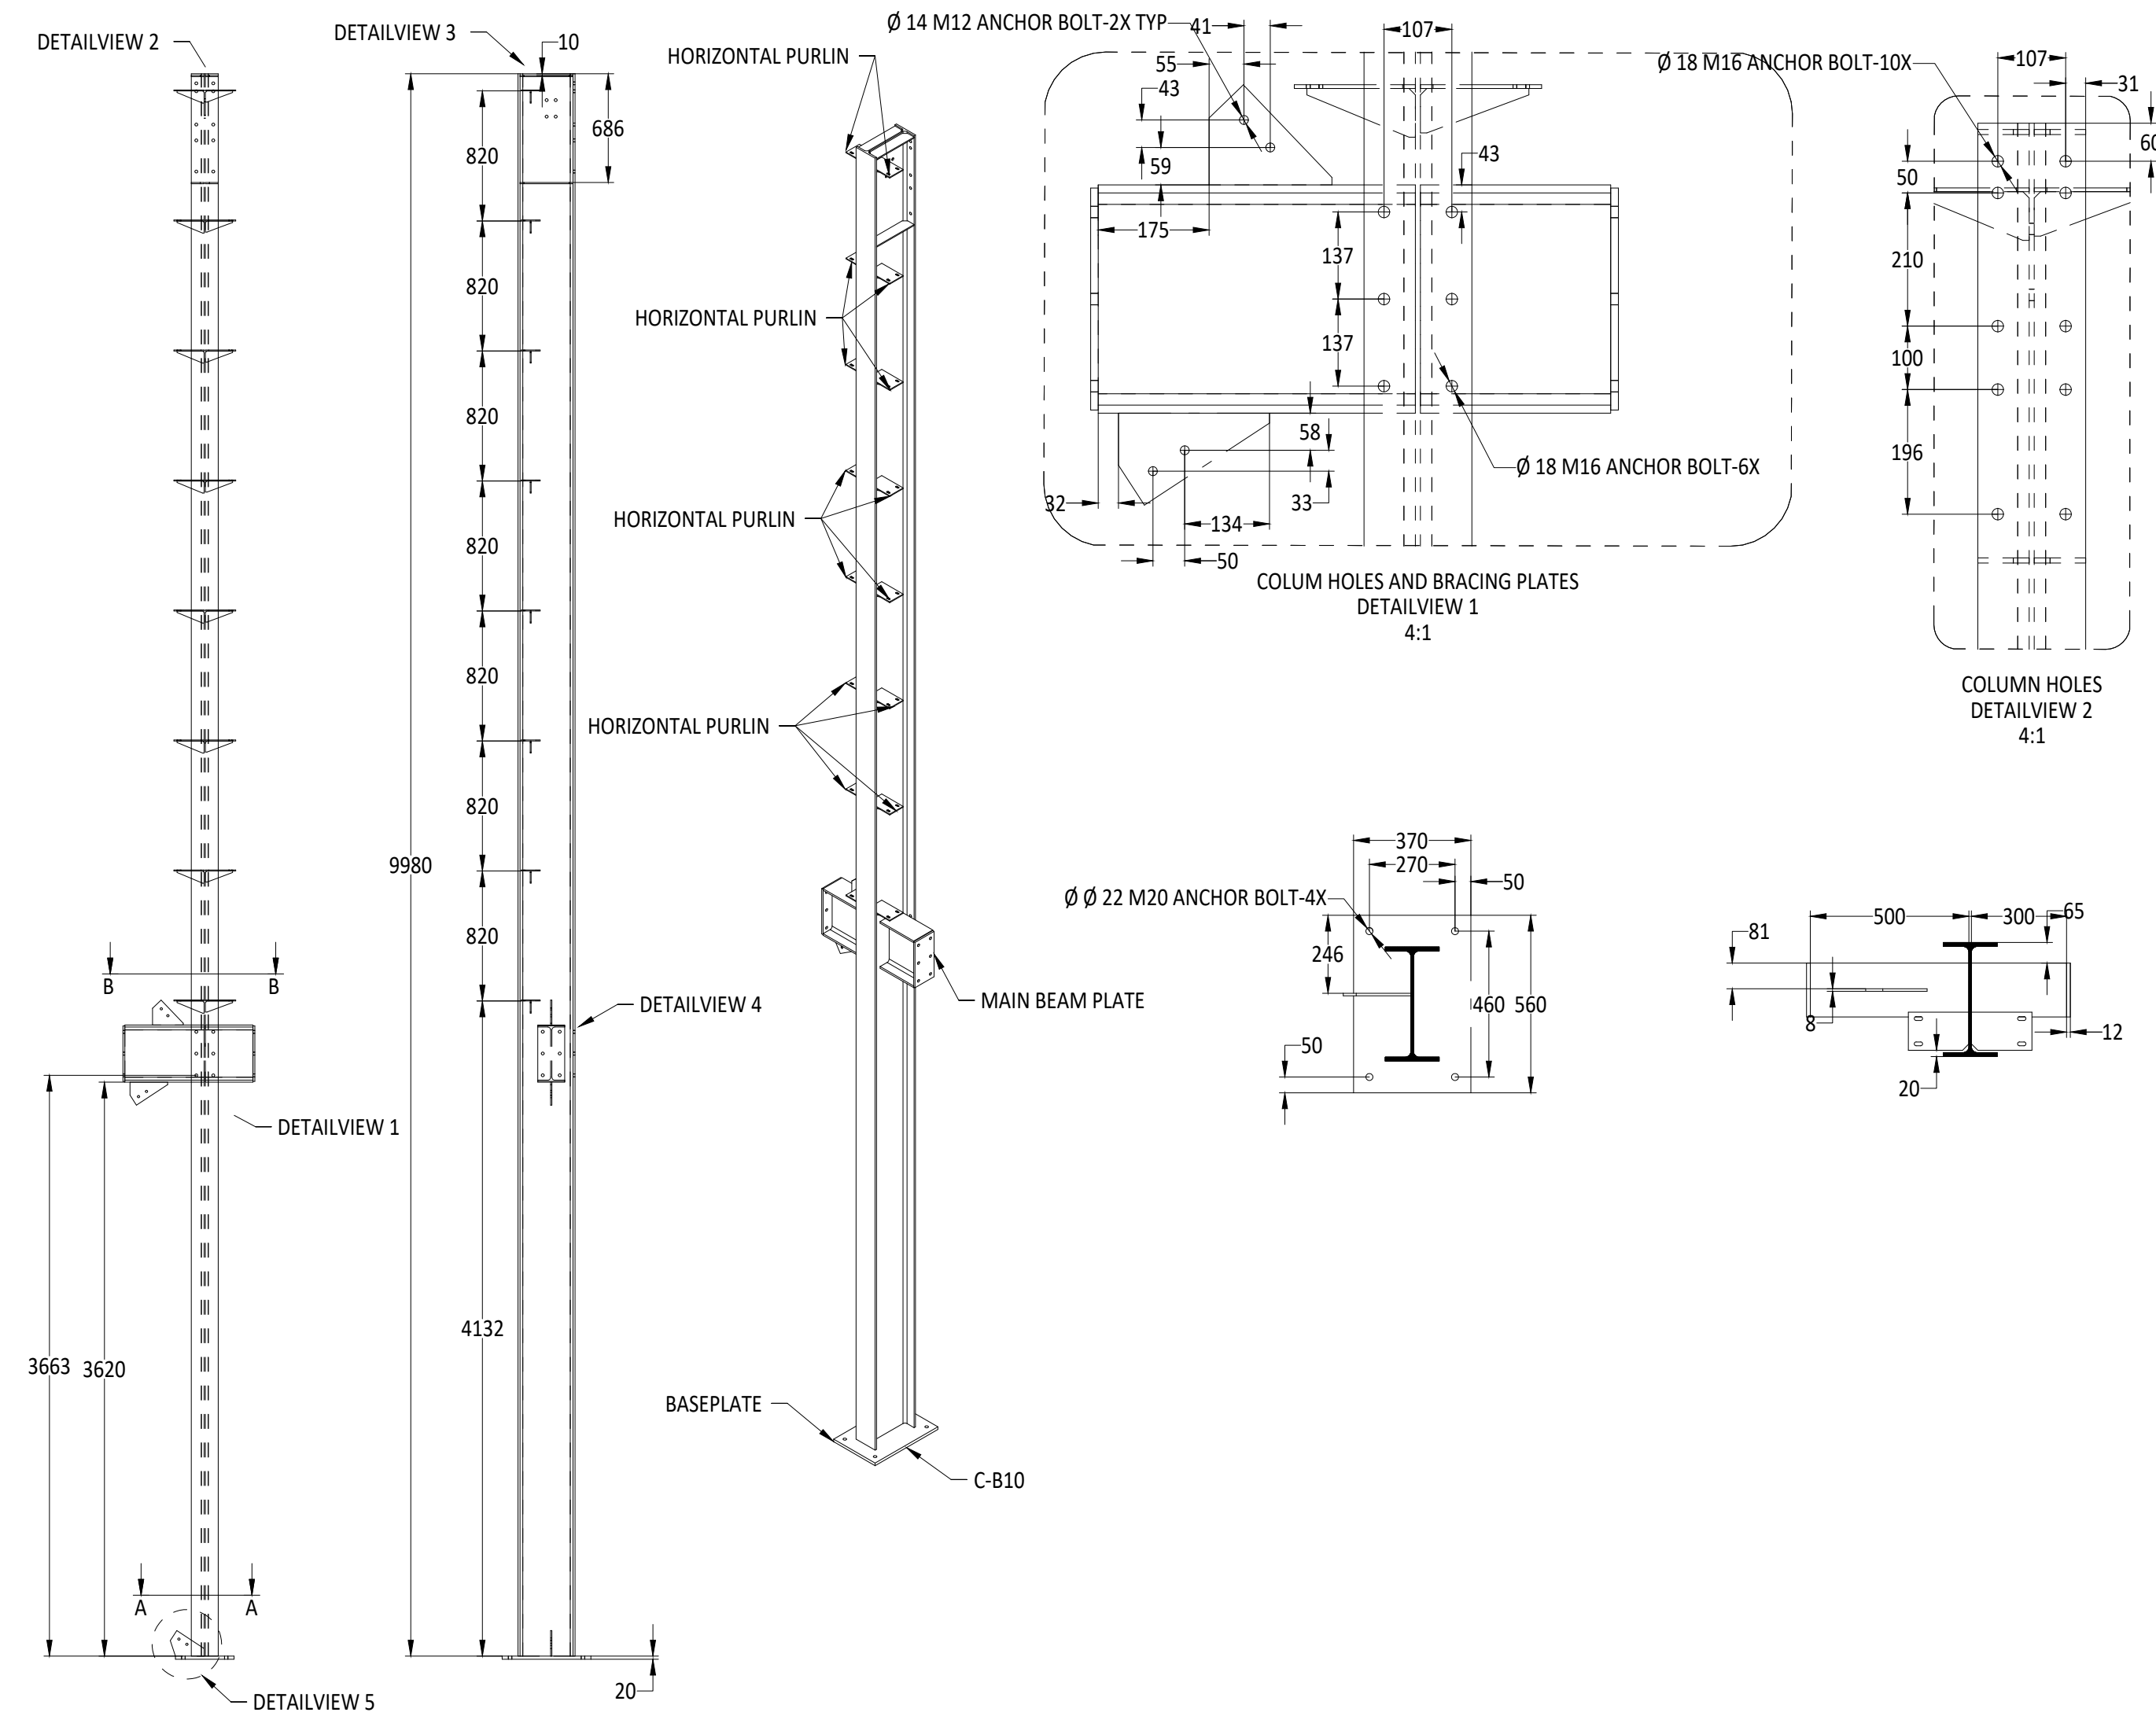

COLUMN C-B10 FABRICATION DETAILS

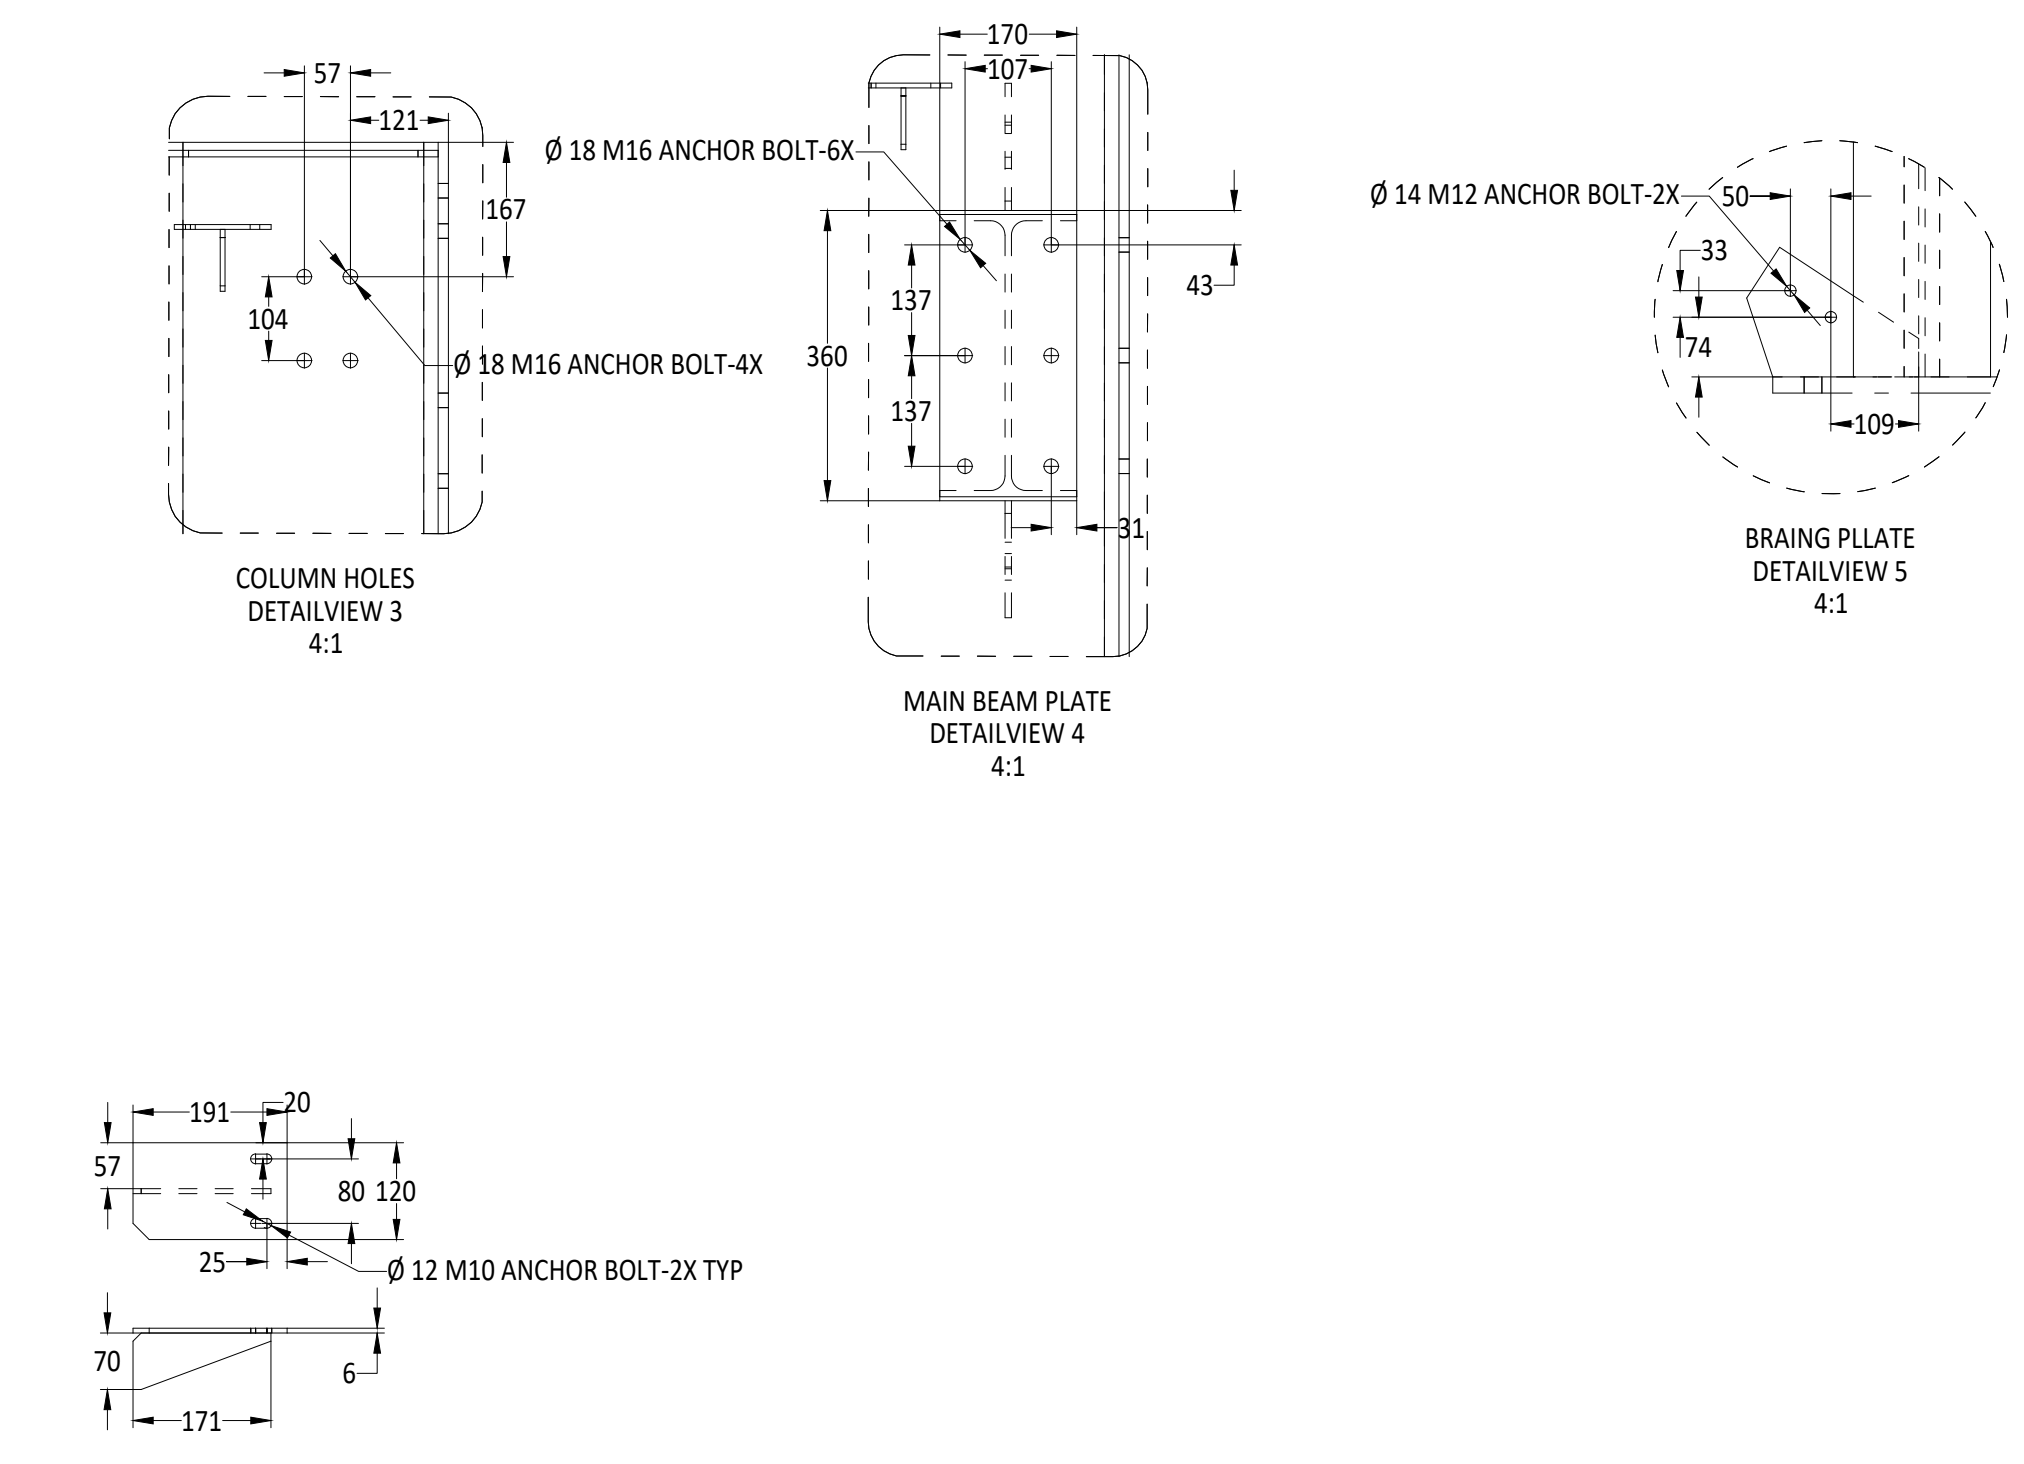

FRAME-B FABRICATION DETAILS

ASSEMBLY NO.		TITLE			
PART NO.		HANGER FRAME-B FABRICATION DETAILS			
DESIGNER		SIZE	DWG NO	REV	
APPROVED		A0		00	
		RELEASE DATE	WEIGHT Kg.	QTY.	
		21/08/2025			
		SCALE AS SHOWN			

A

B

C

D

E

F

G

H

I

J

K

L

A

B

C

D

E

F

G


H

I


J

K


L

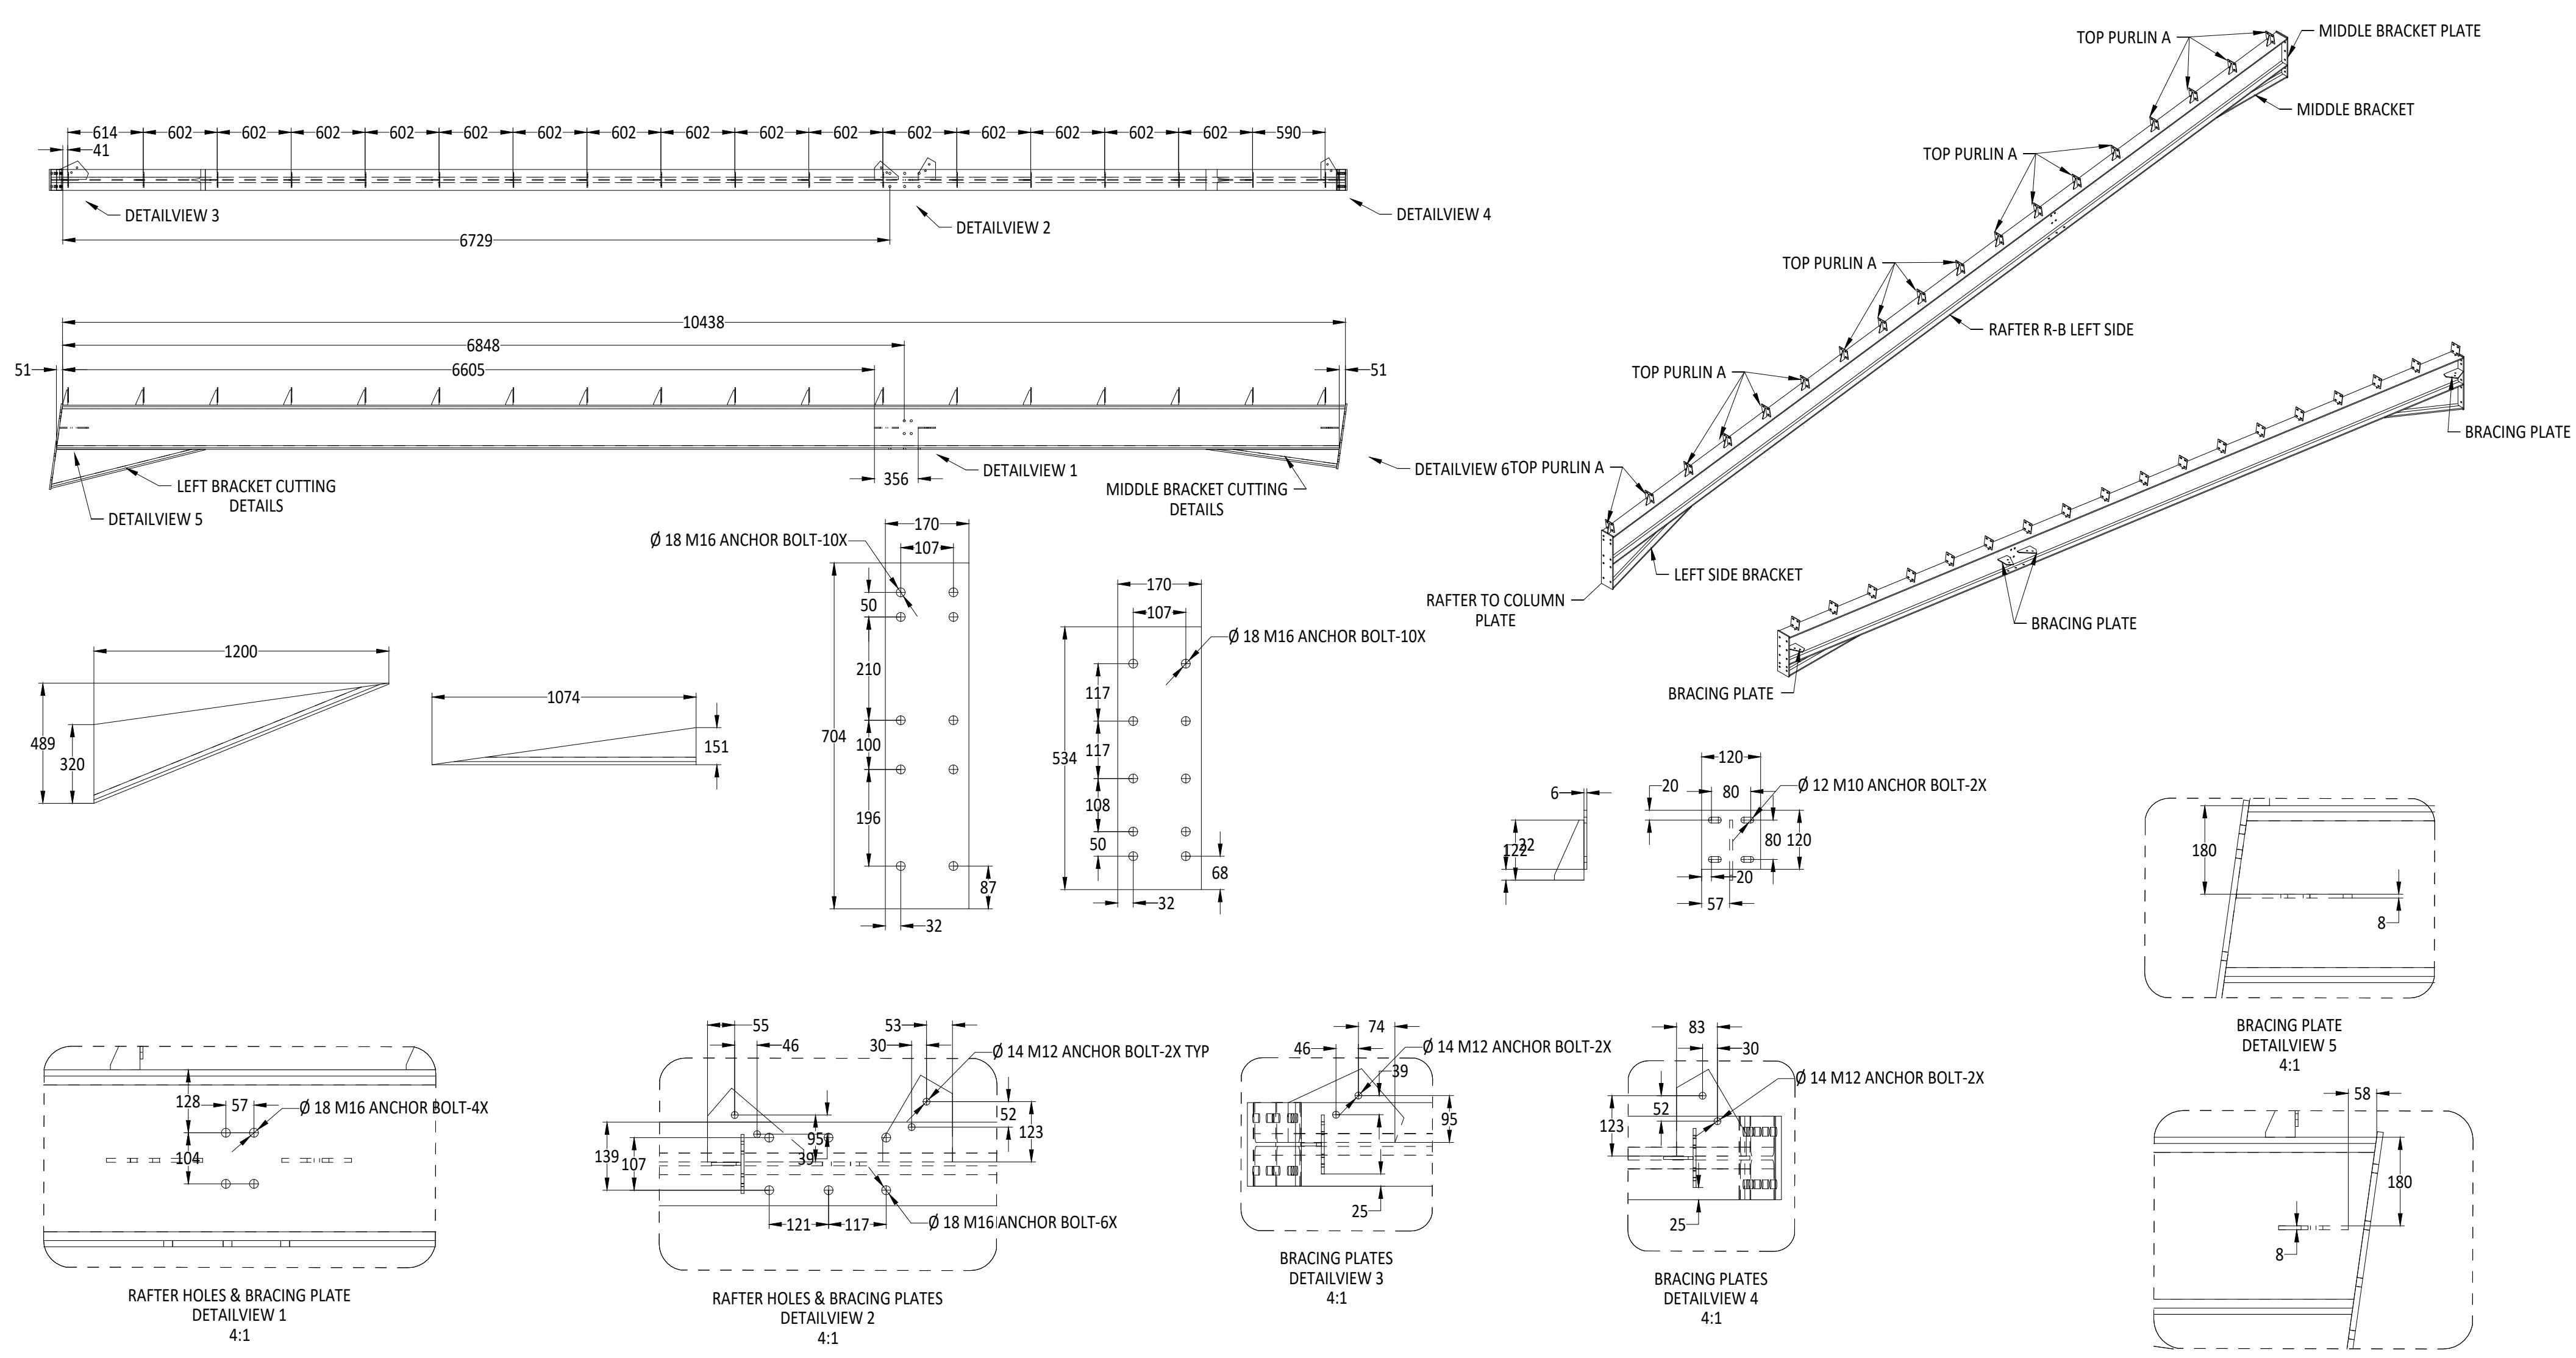


RAFTER R-B LEFT SIDE FABRICATION DETAILS

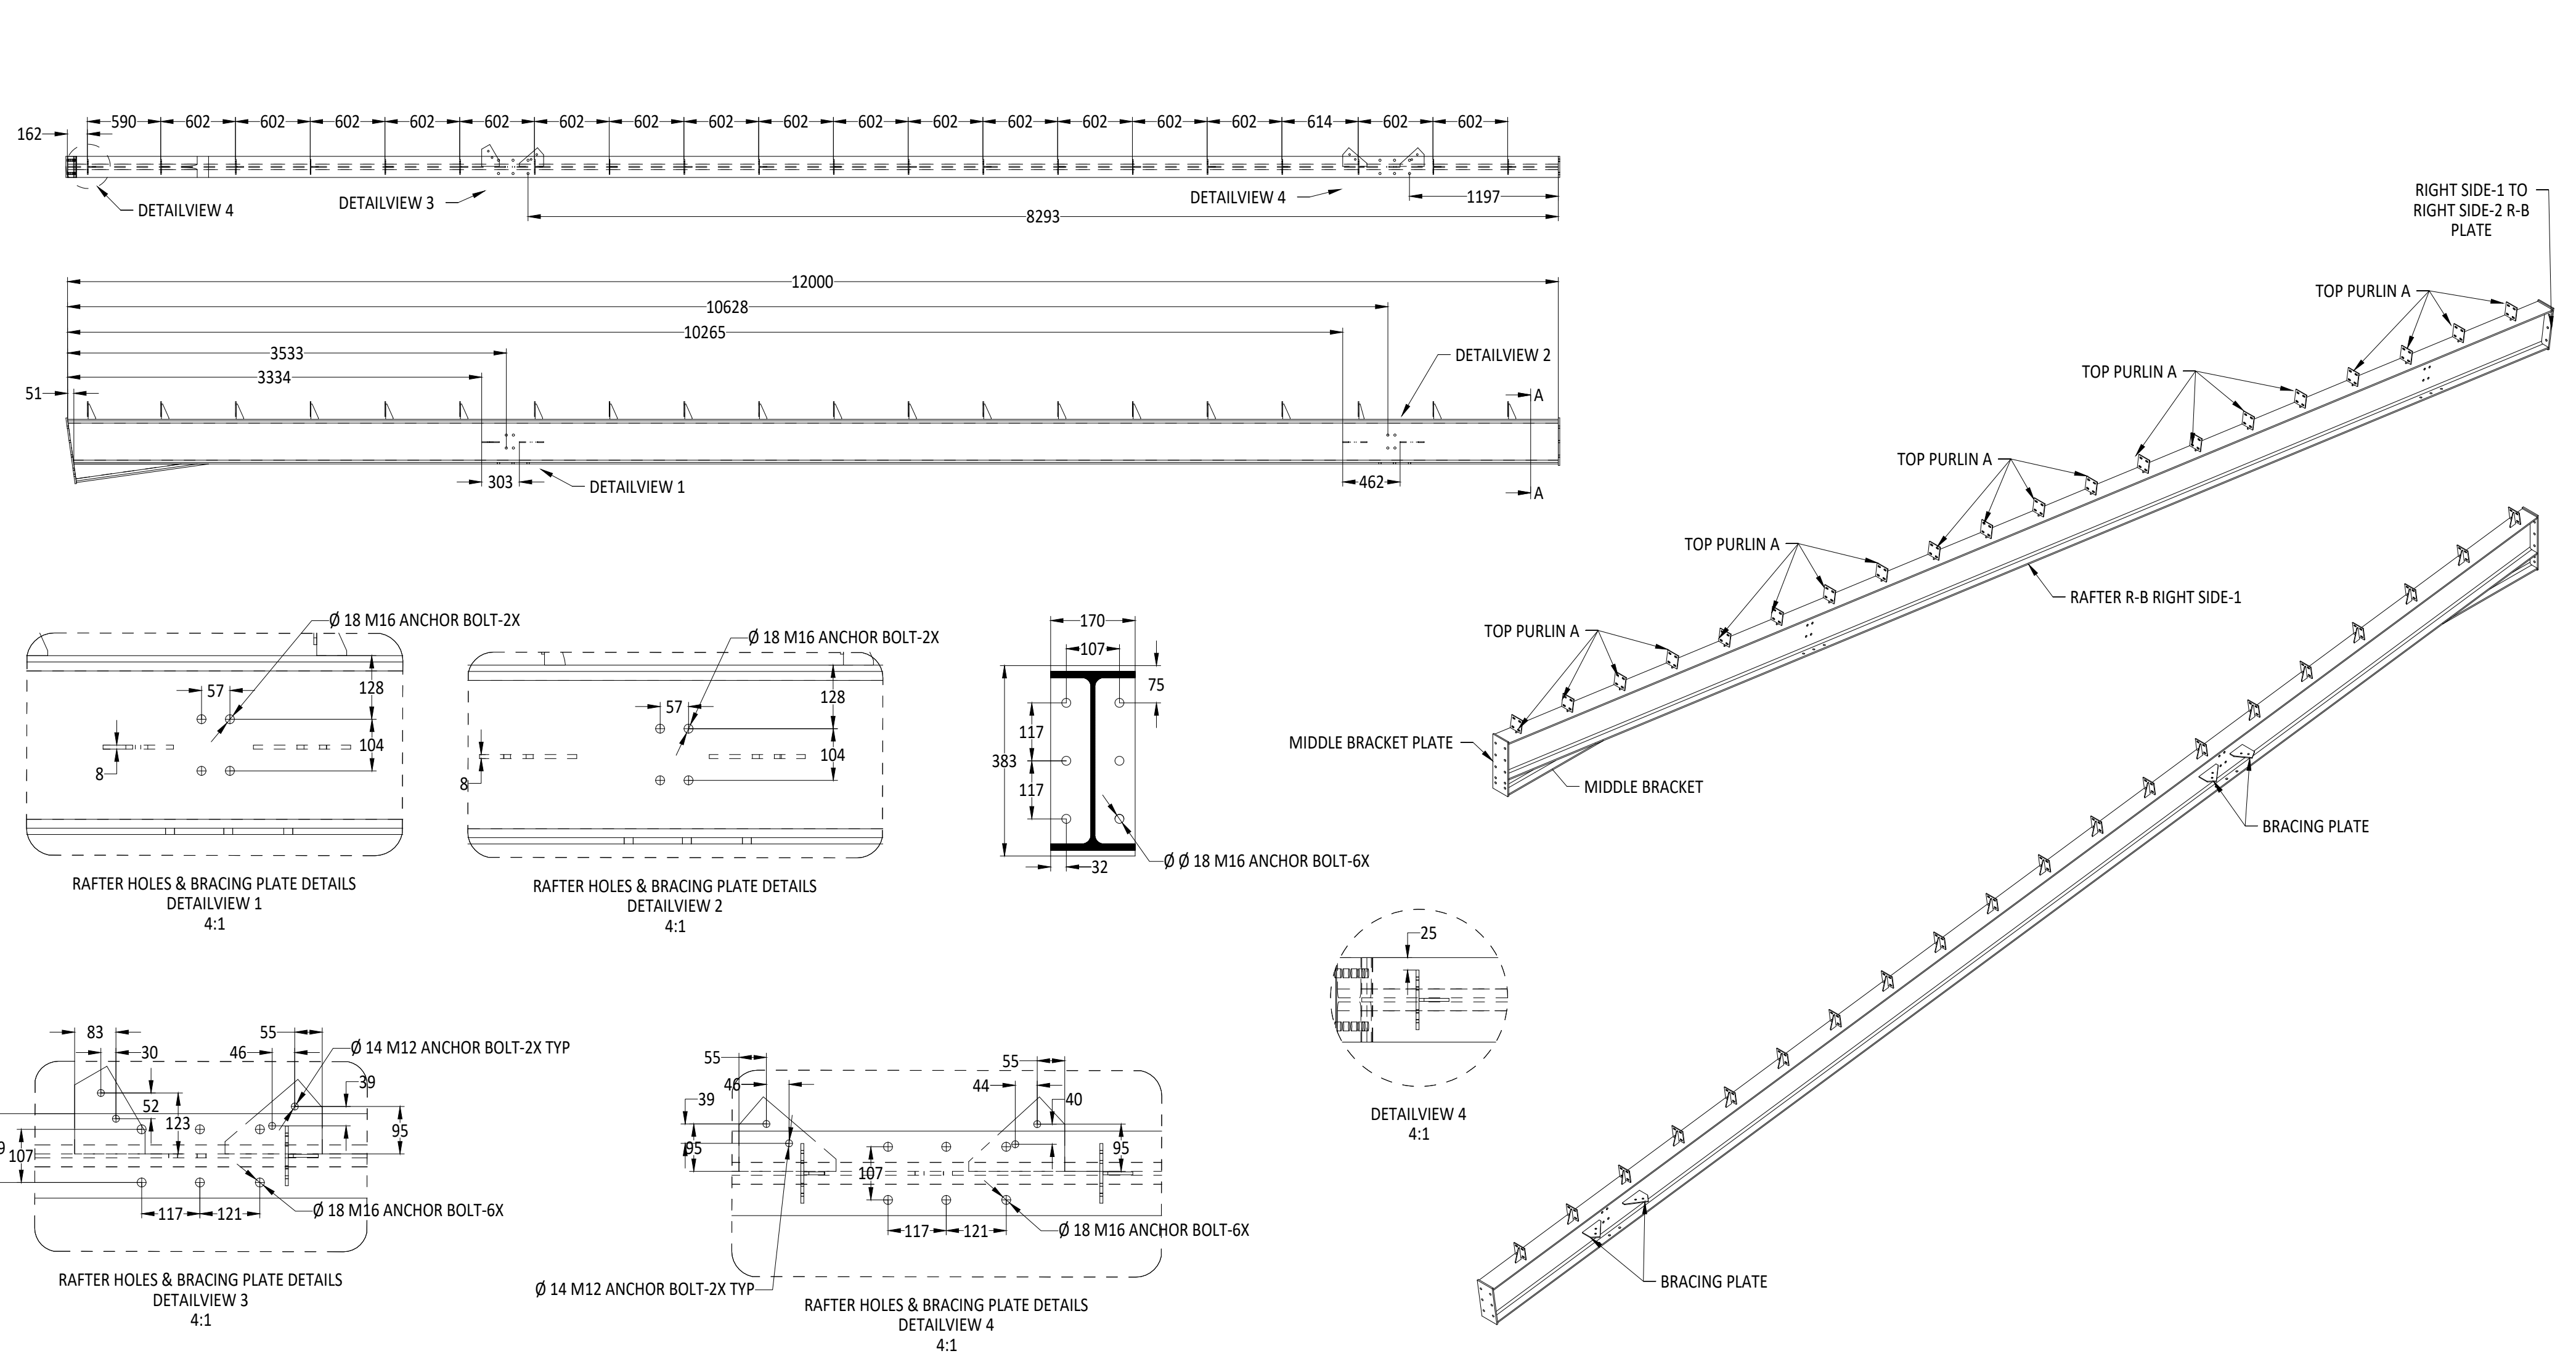


RAFTER R-B RIGHT SIDE-1 FABRICATION DETAILS

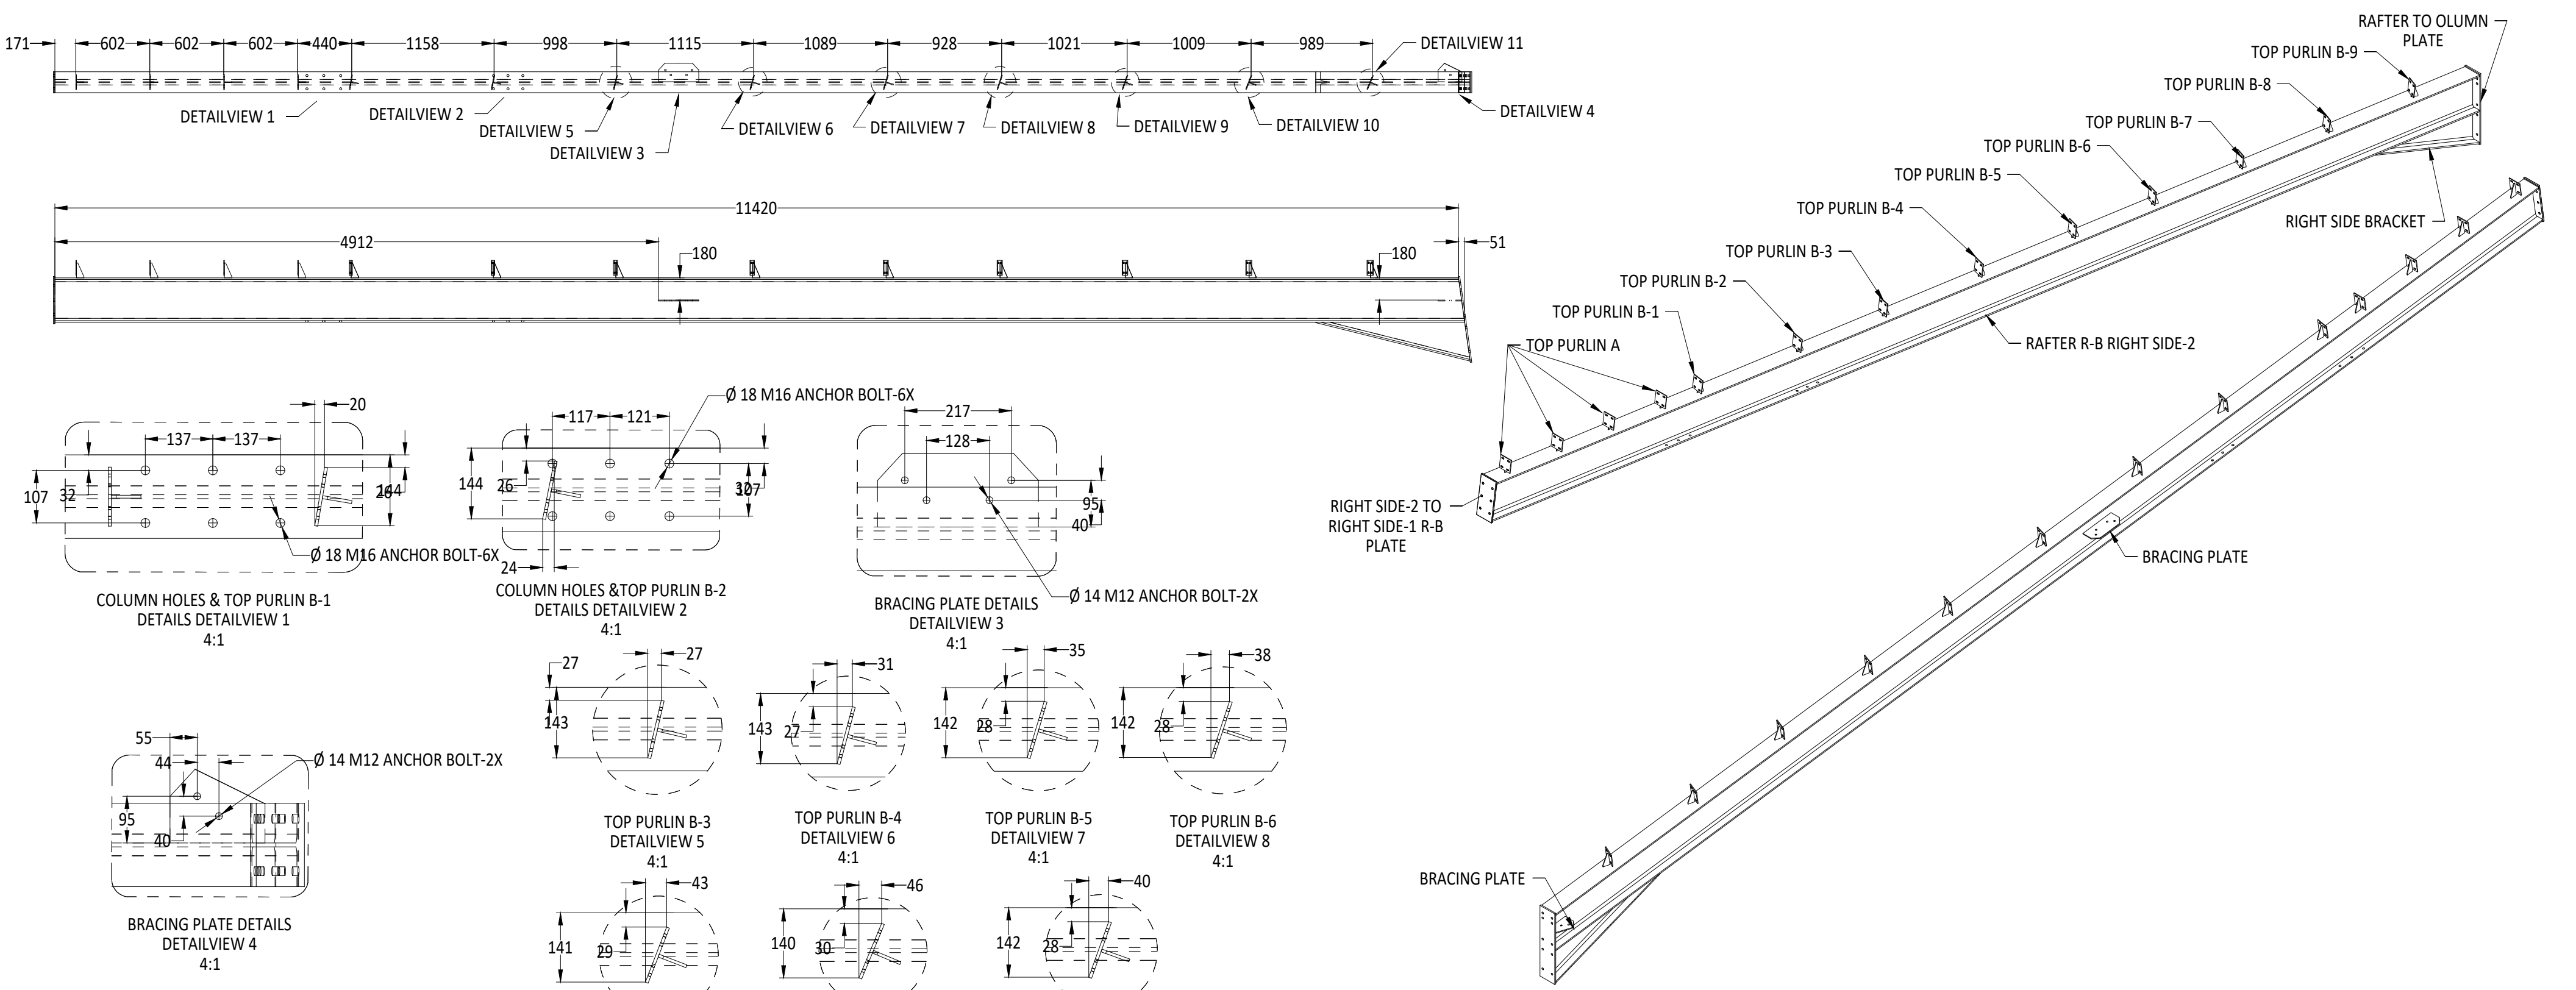

RAFTER R-B RIGHT SIDE-2 FABRICATION DETAILS

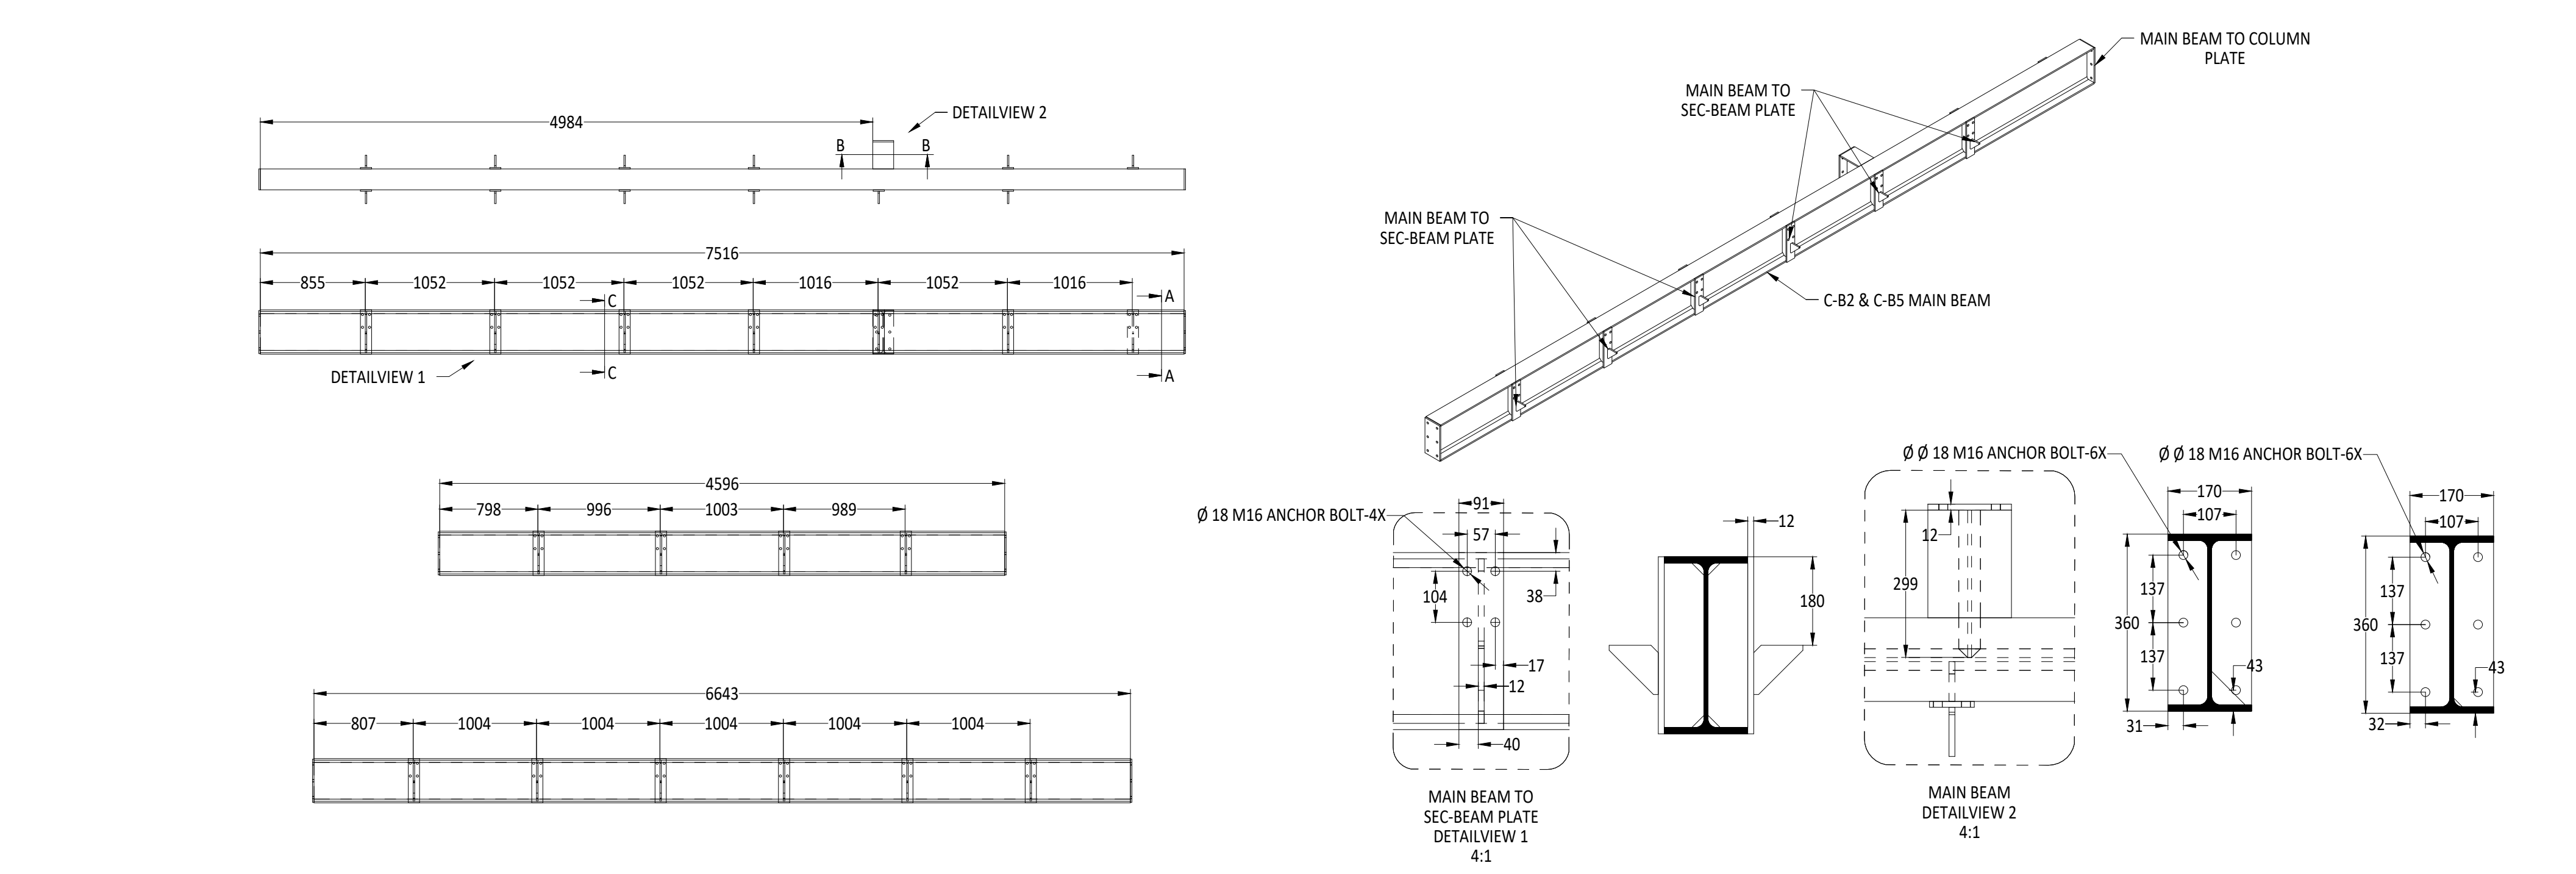


ASSEMBLY NO.		TITLE			
PART NO.		HANGER FRAME-B FABRICATION DETAILS			
DESIGNER		SCALE AS SHOWN	SIZE A0	DWG NO	REV 00
APPROVED		RELEASE DATE 21/08/2025	WEIGHT Kg.	QTY.	

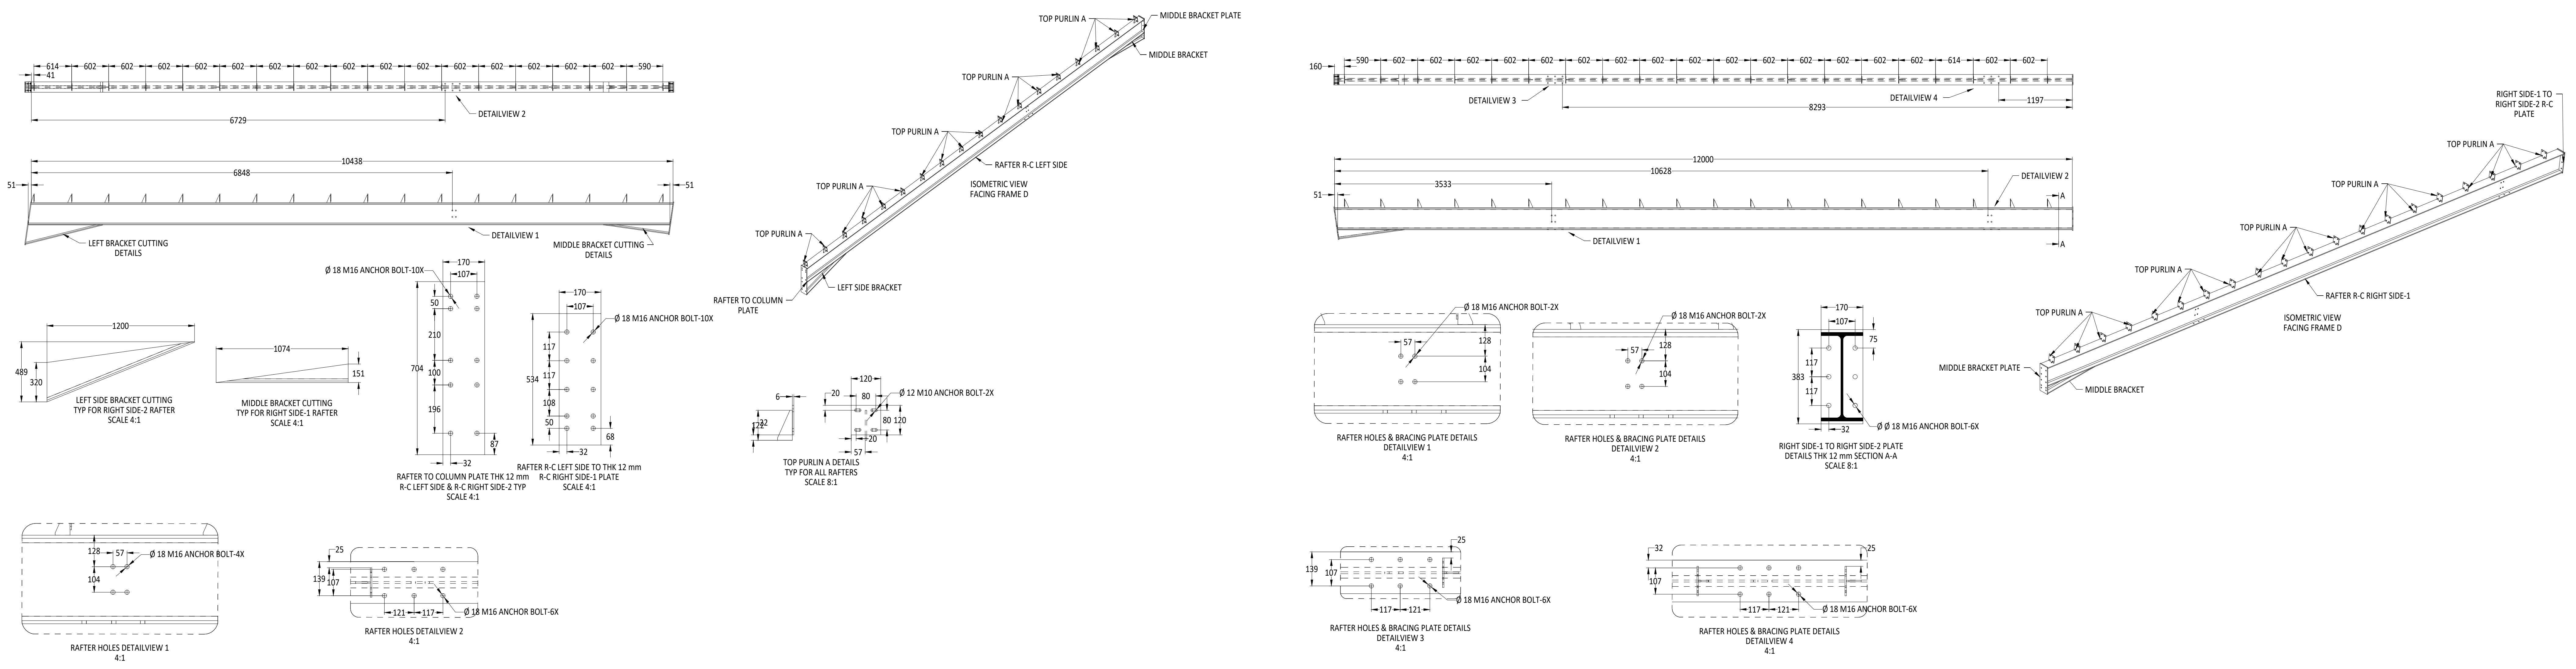


RAFTER R-C LEFT SIDE FABRICATION DETAILS

RAFTER R-C RIGHT SIDE-1 FABRICATION DETAILS

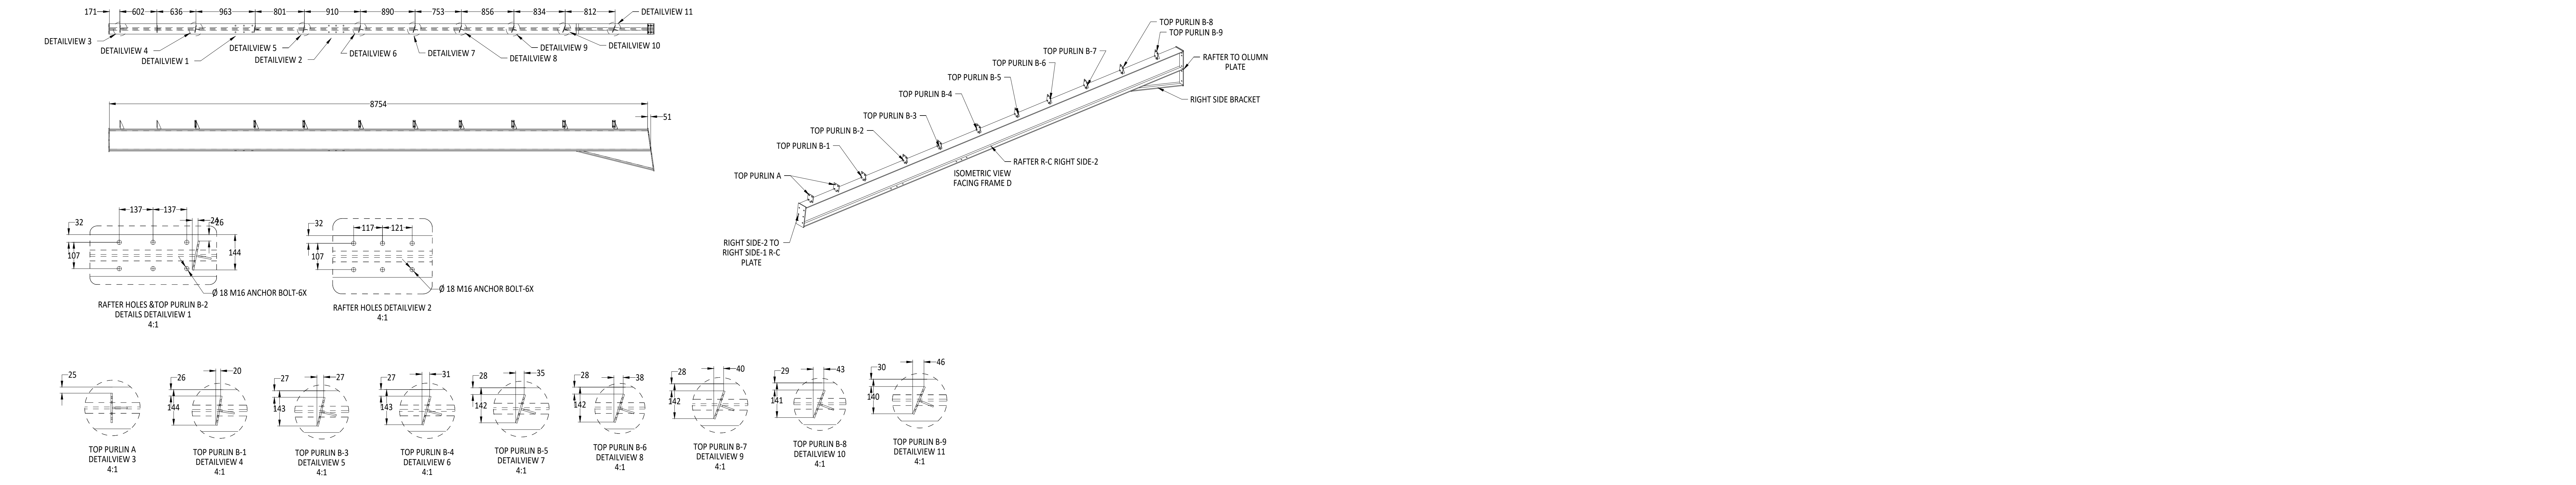

RAFTER R-C RIGHT SIDE-2 FABRICATION DETAILS

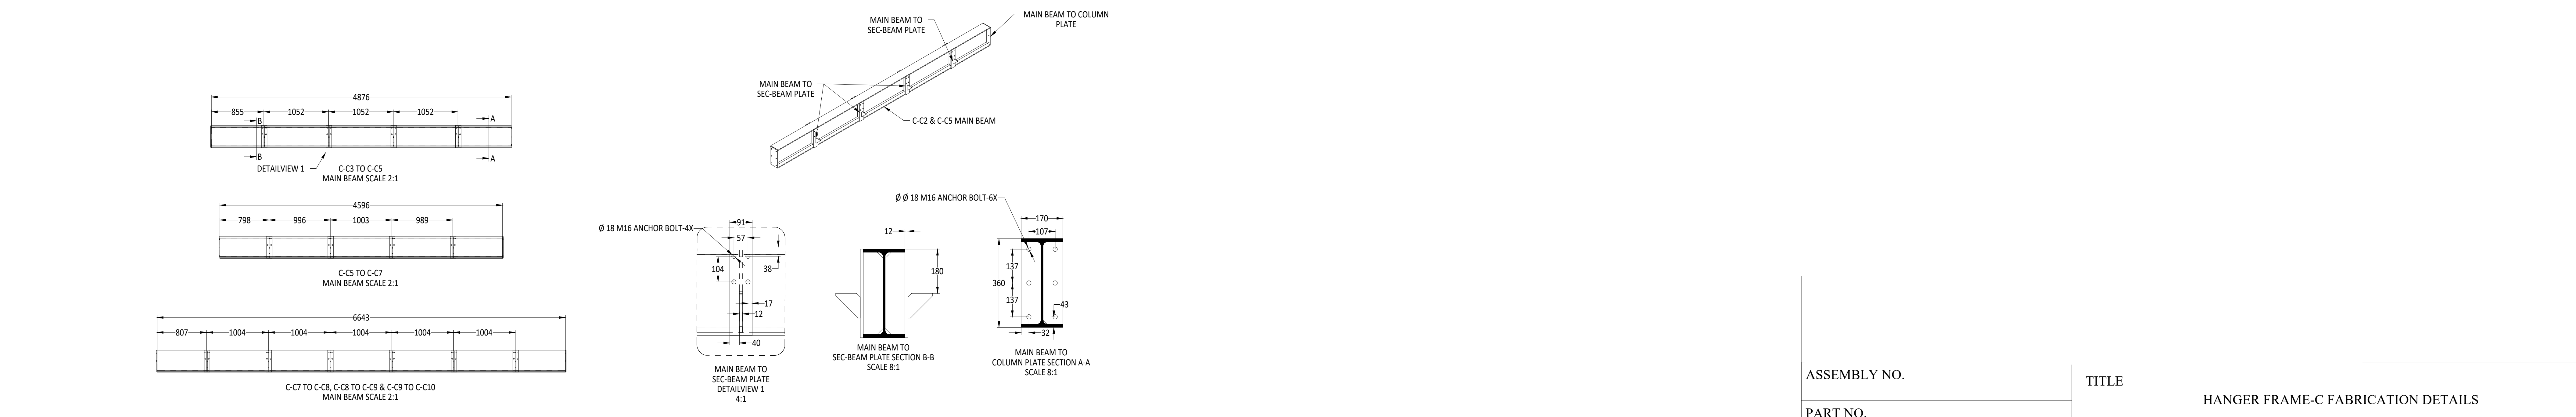

MAIN BEAMS FABRICATION DETAILS

ASSEMBLY NO.		TITLE			
PART NO.		HANGER FRAME-C FABRICATION DETAILS			
DESIGNER		SIZE	DWG NO	REV	
APPROVED		A0		00	
SCALE AS SHOWN		RELEASE DATE		WEIGHT Kg.	QTY.
		21/08/2025			

A

B

C

D

E

F

G


H

I

J

K

L

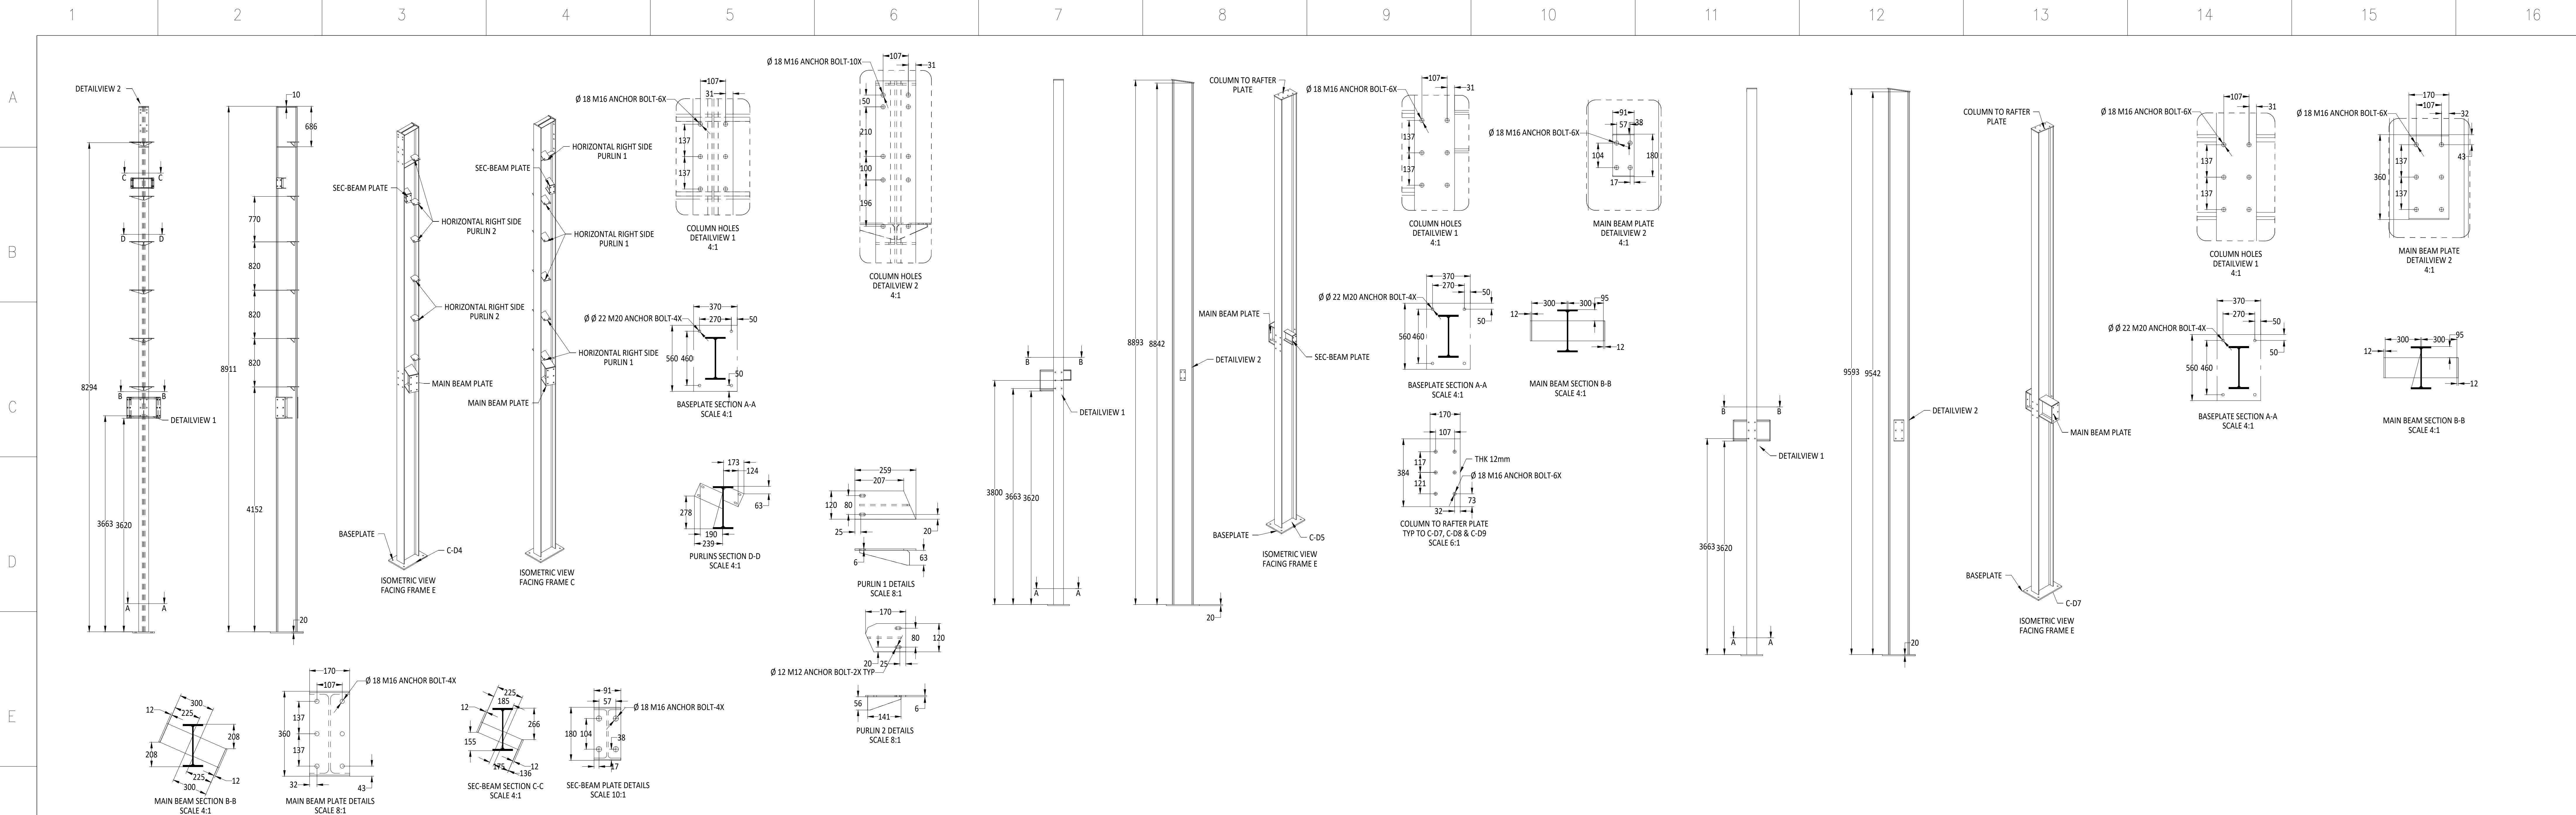

COLUMN C-D4 FABRICATION DETAILS

COLUMN C-D5 FABRICATION DETAILS

COLUMN C-D7 FABRICATION DETAILS

A

B


C

D

E

F

G

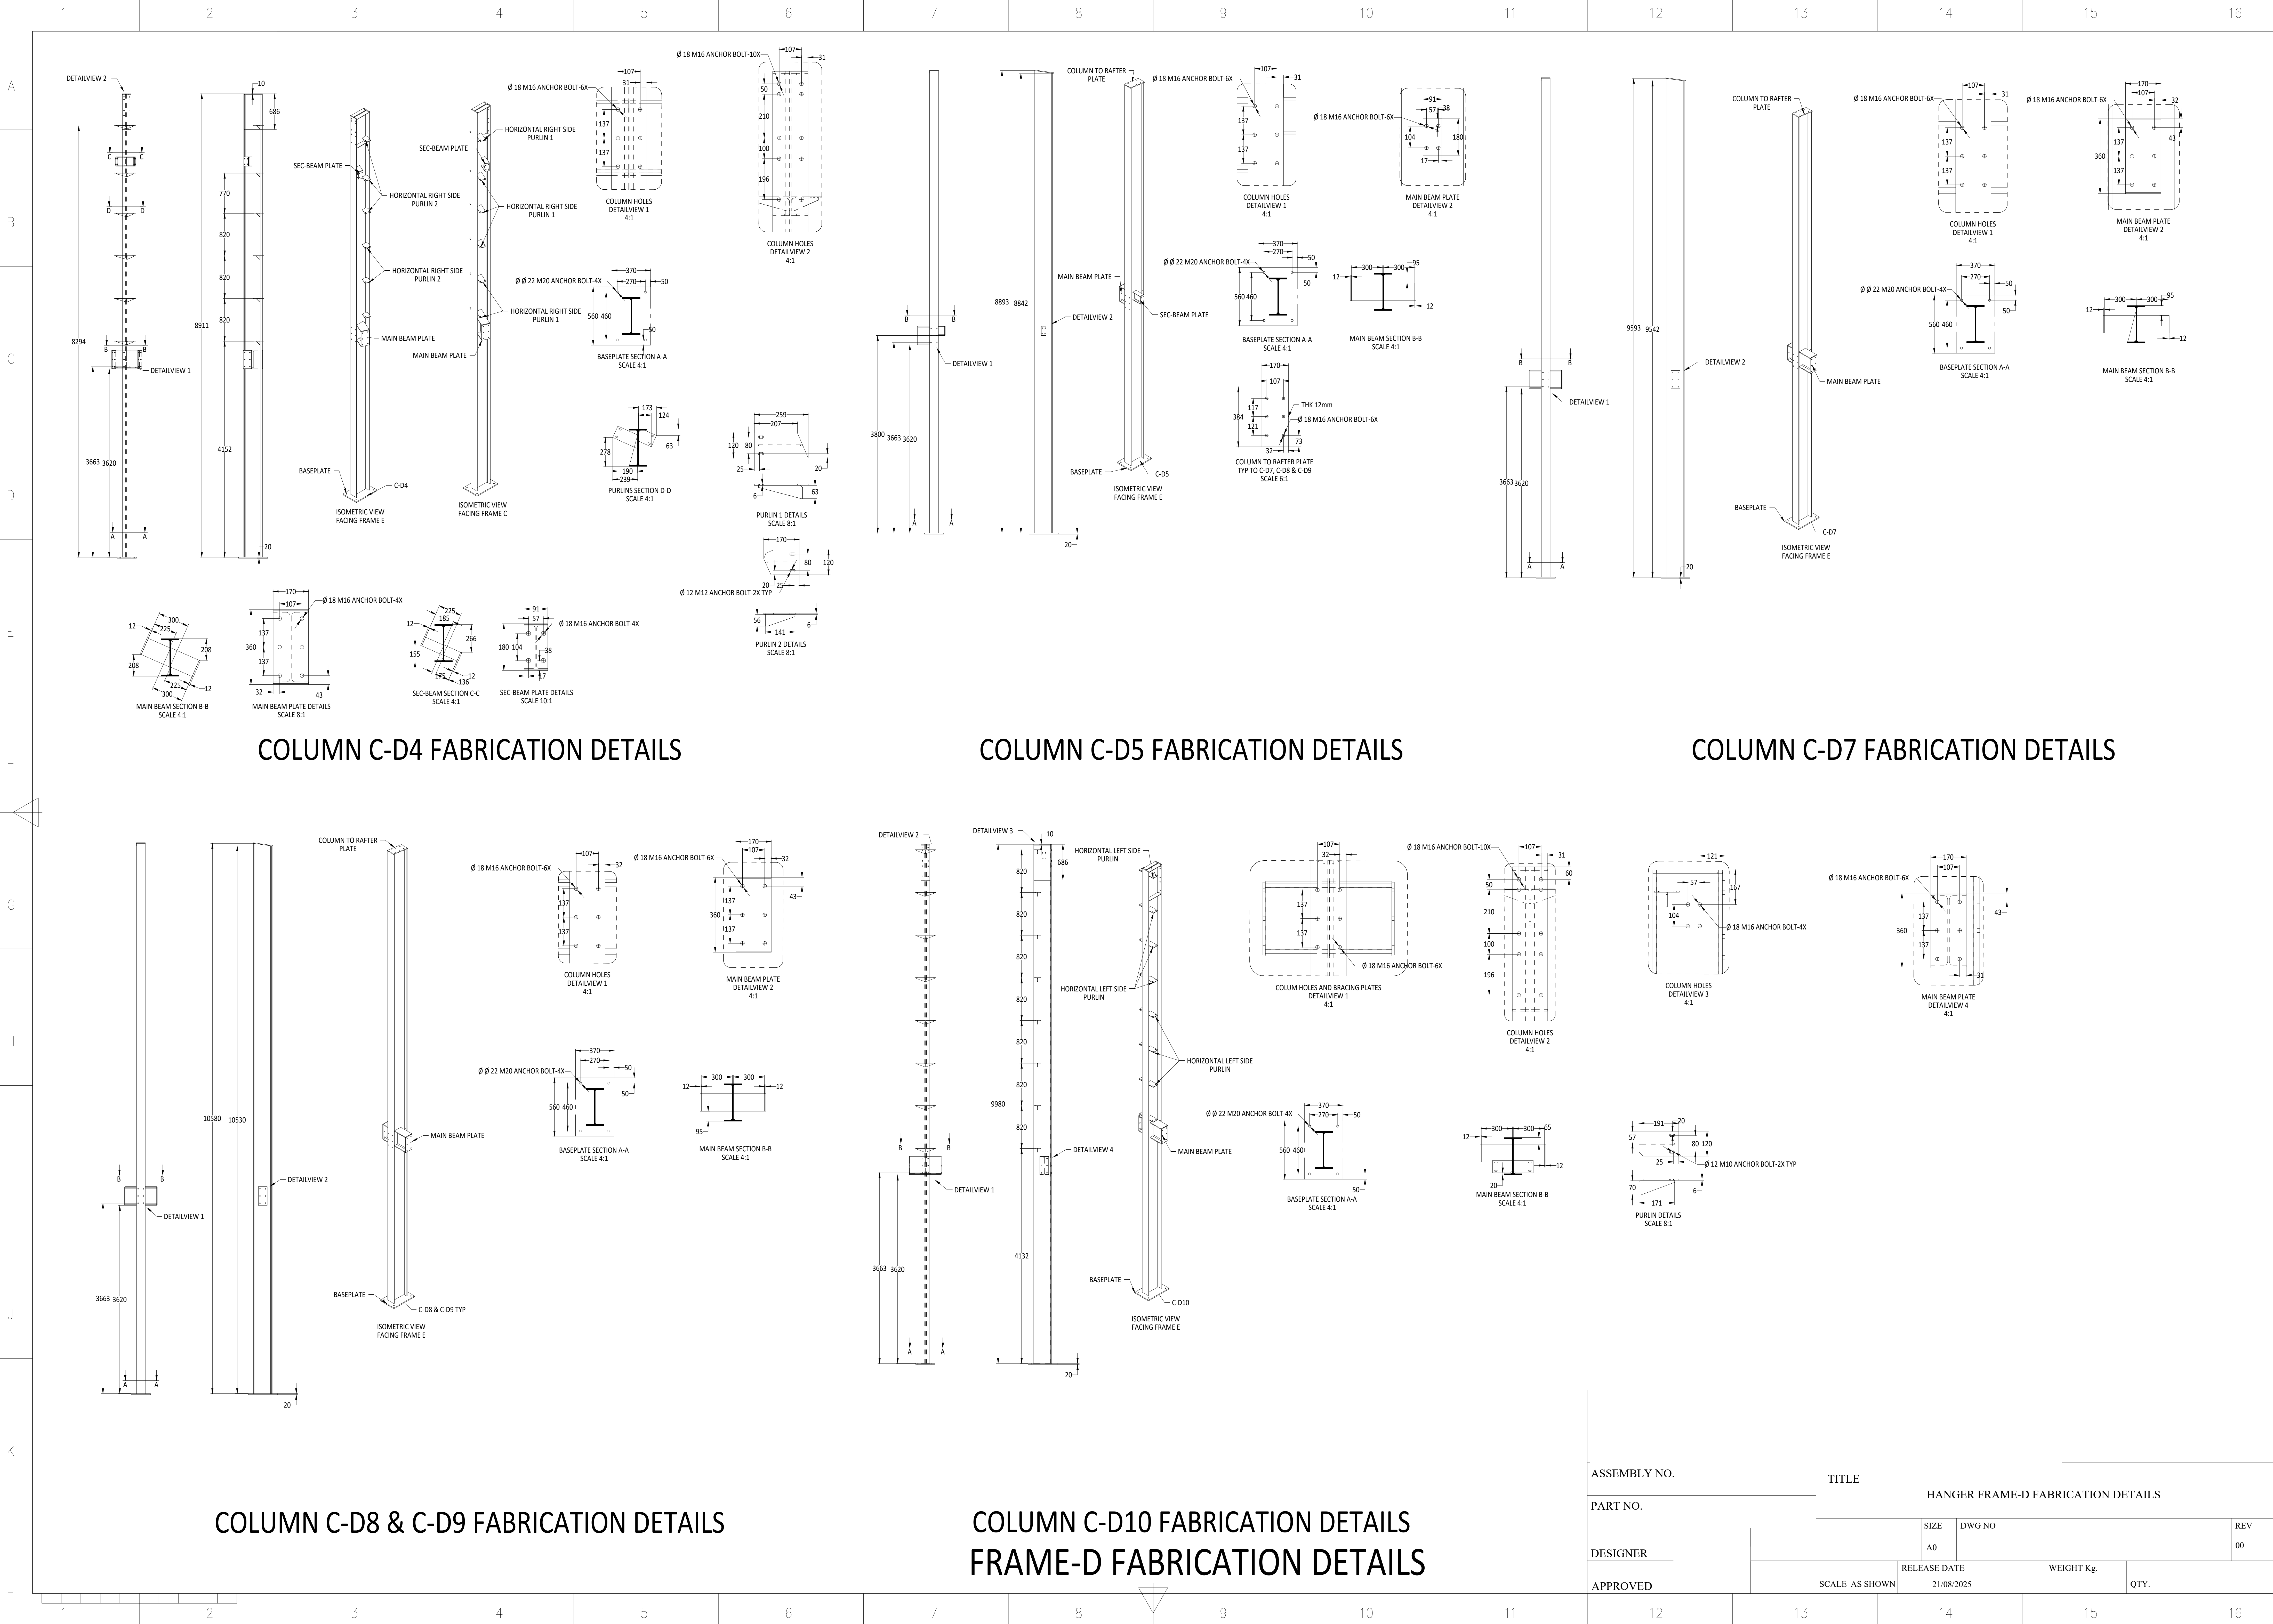

COLUMN C-D8 & C-D9 FABRICATION DETAILS

COLUMN C-D10 FABRICATION DETAILS
FRAME-D FABRICATION DETAILS

ASSEMBLY NO.

PART NO.

DESIGNER

APPROVED

TITLE

HANGER FRAME-D FABRICATION DETAILS

SIZE

A0

DWG NO

RELEASE DATE

21/08/2025

WEIGHT Kg.

QTY.

G


H

I


J

K


L

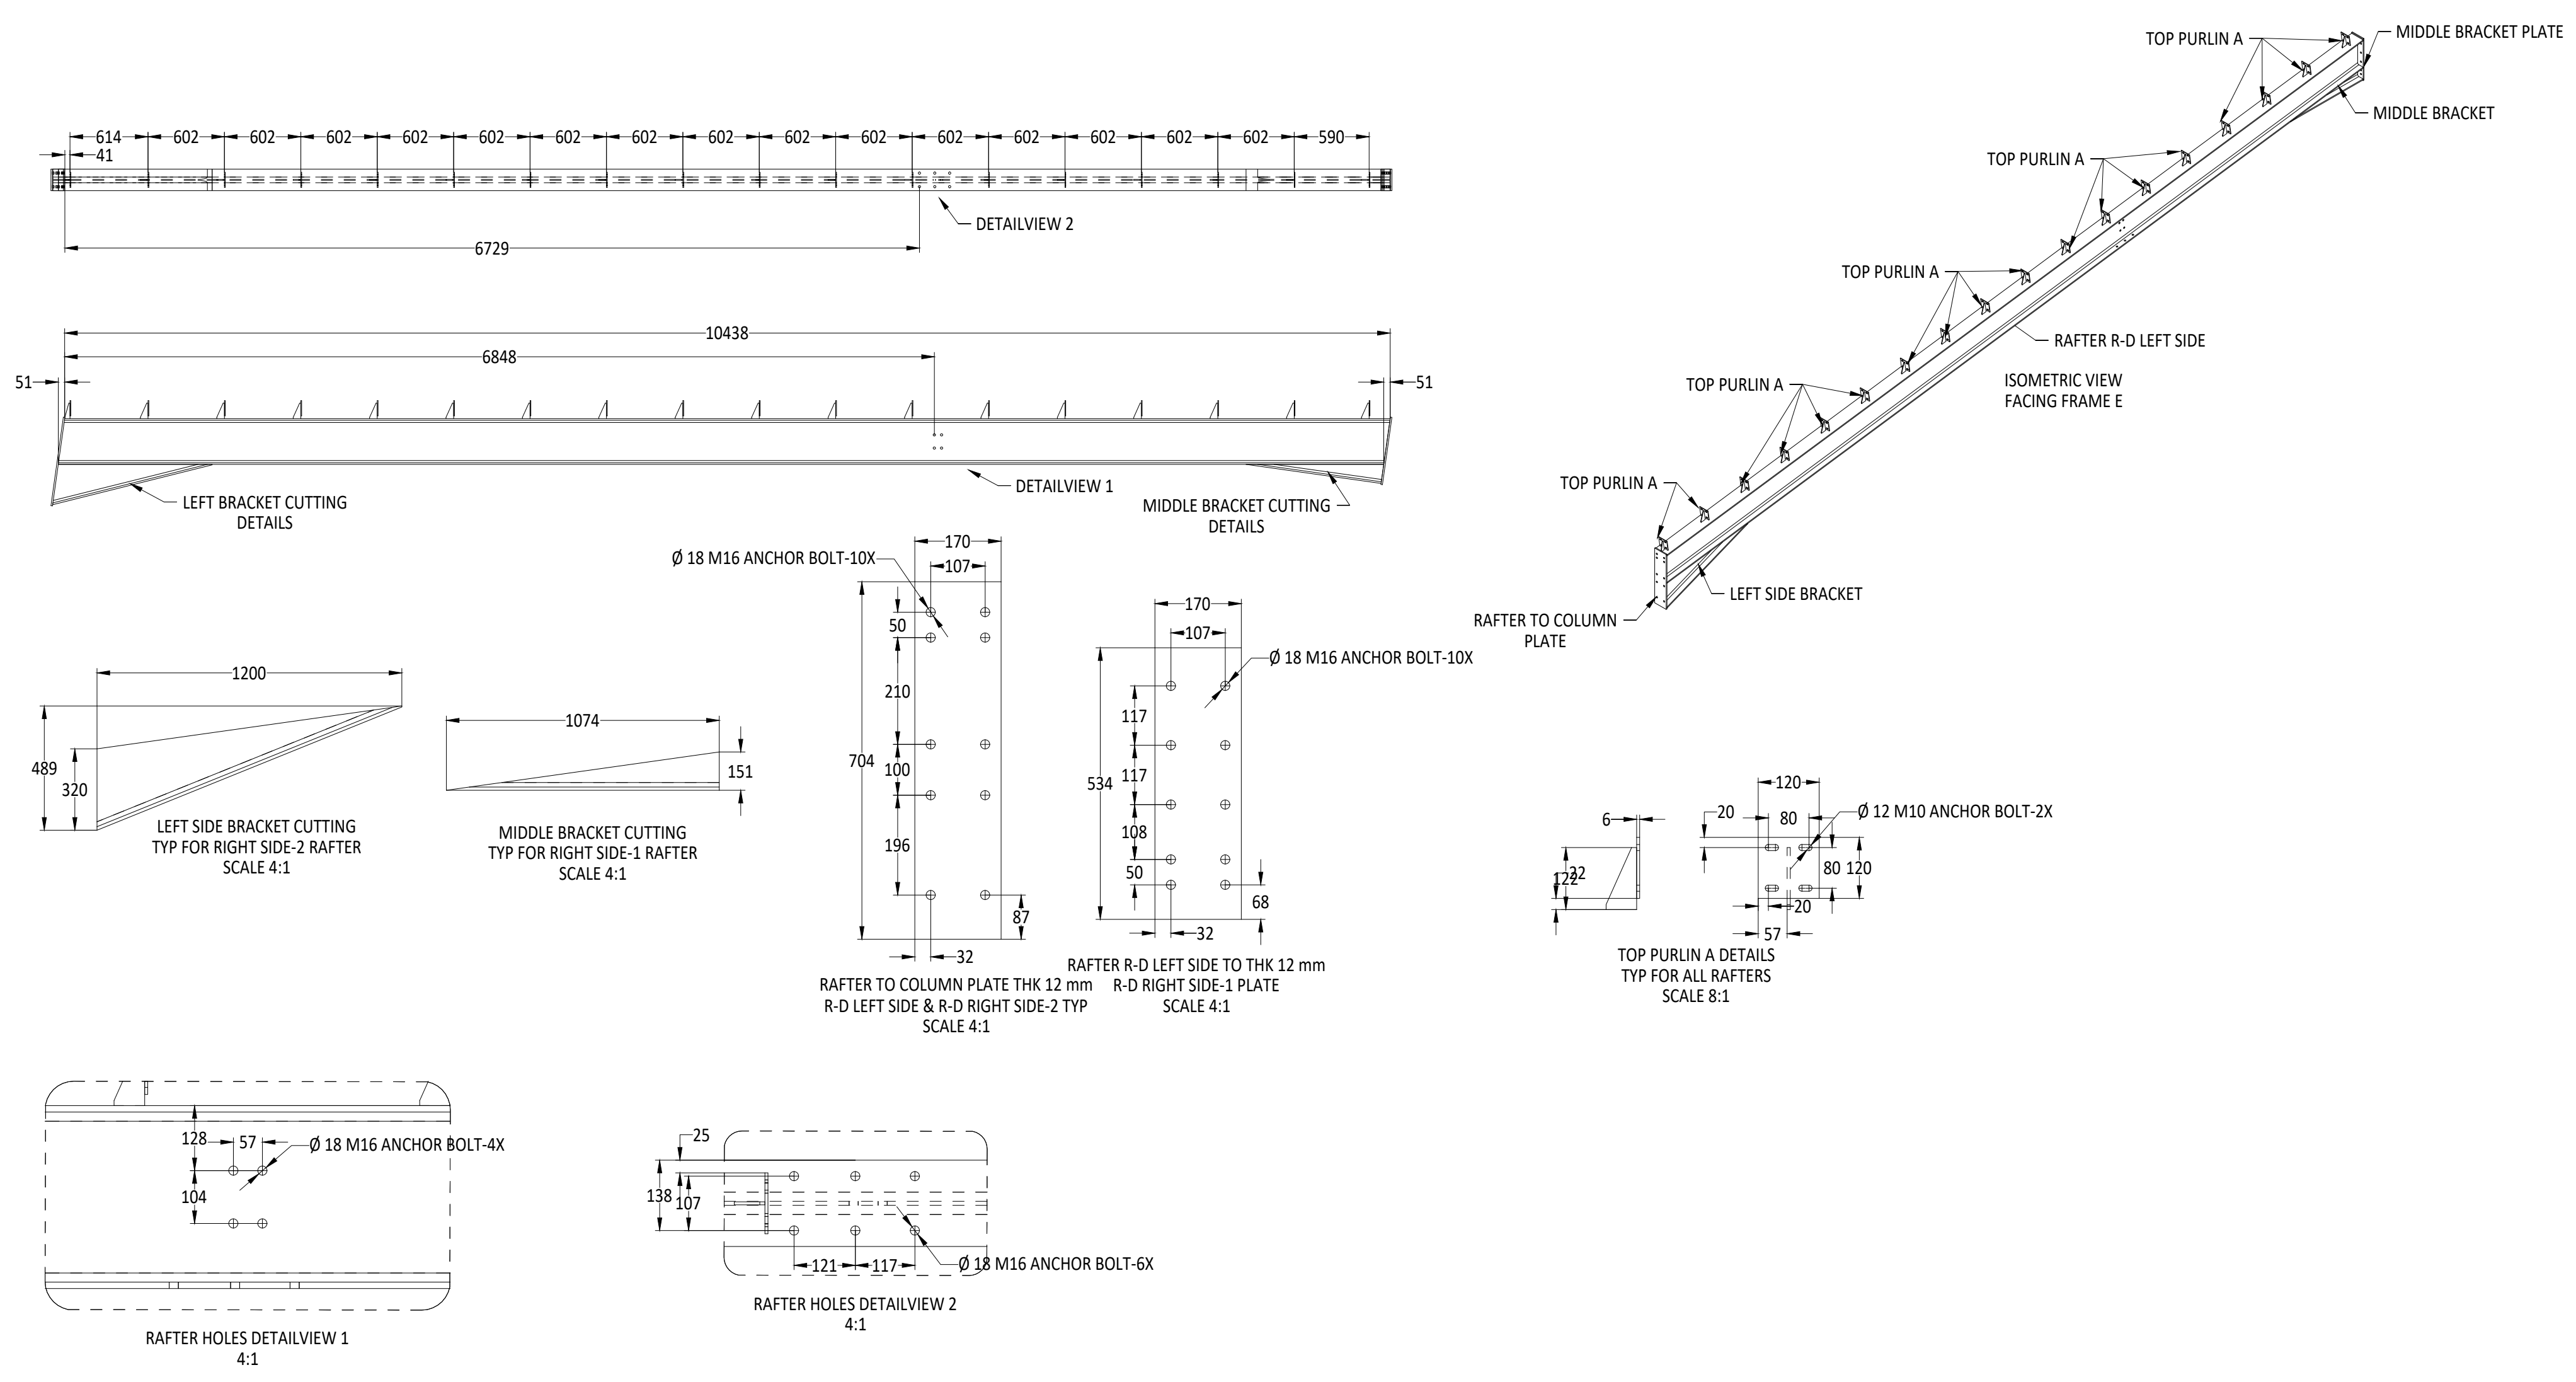


RAFTER R-D LEFT SIDE FABRICATION DETAILS

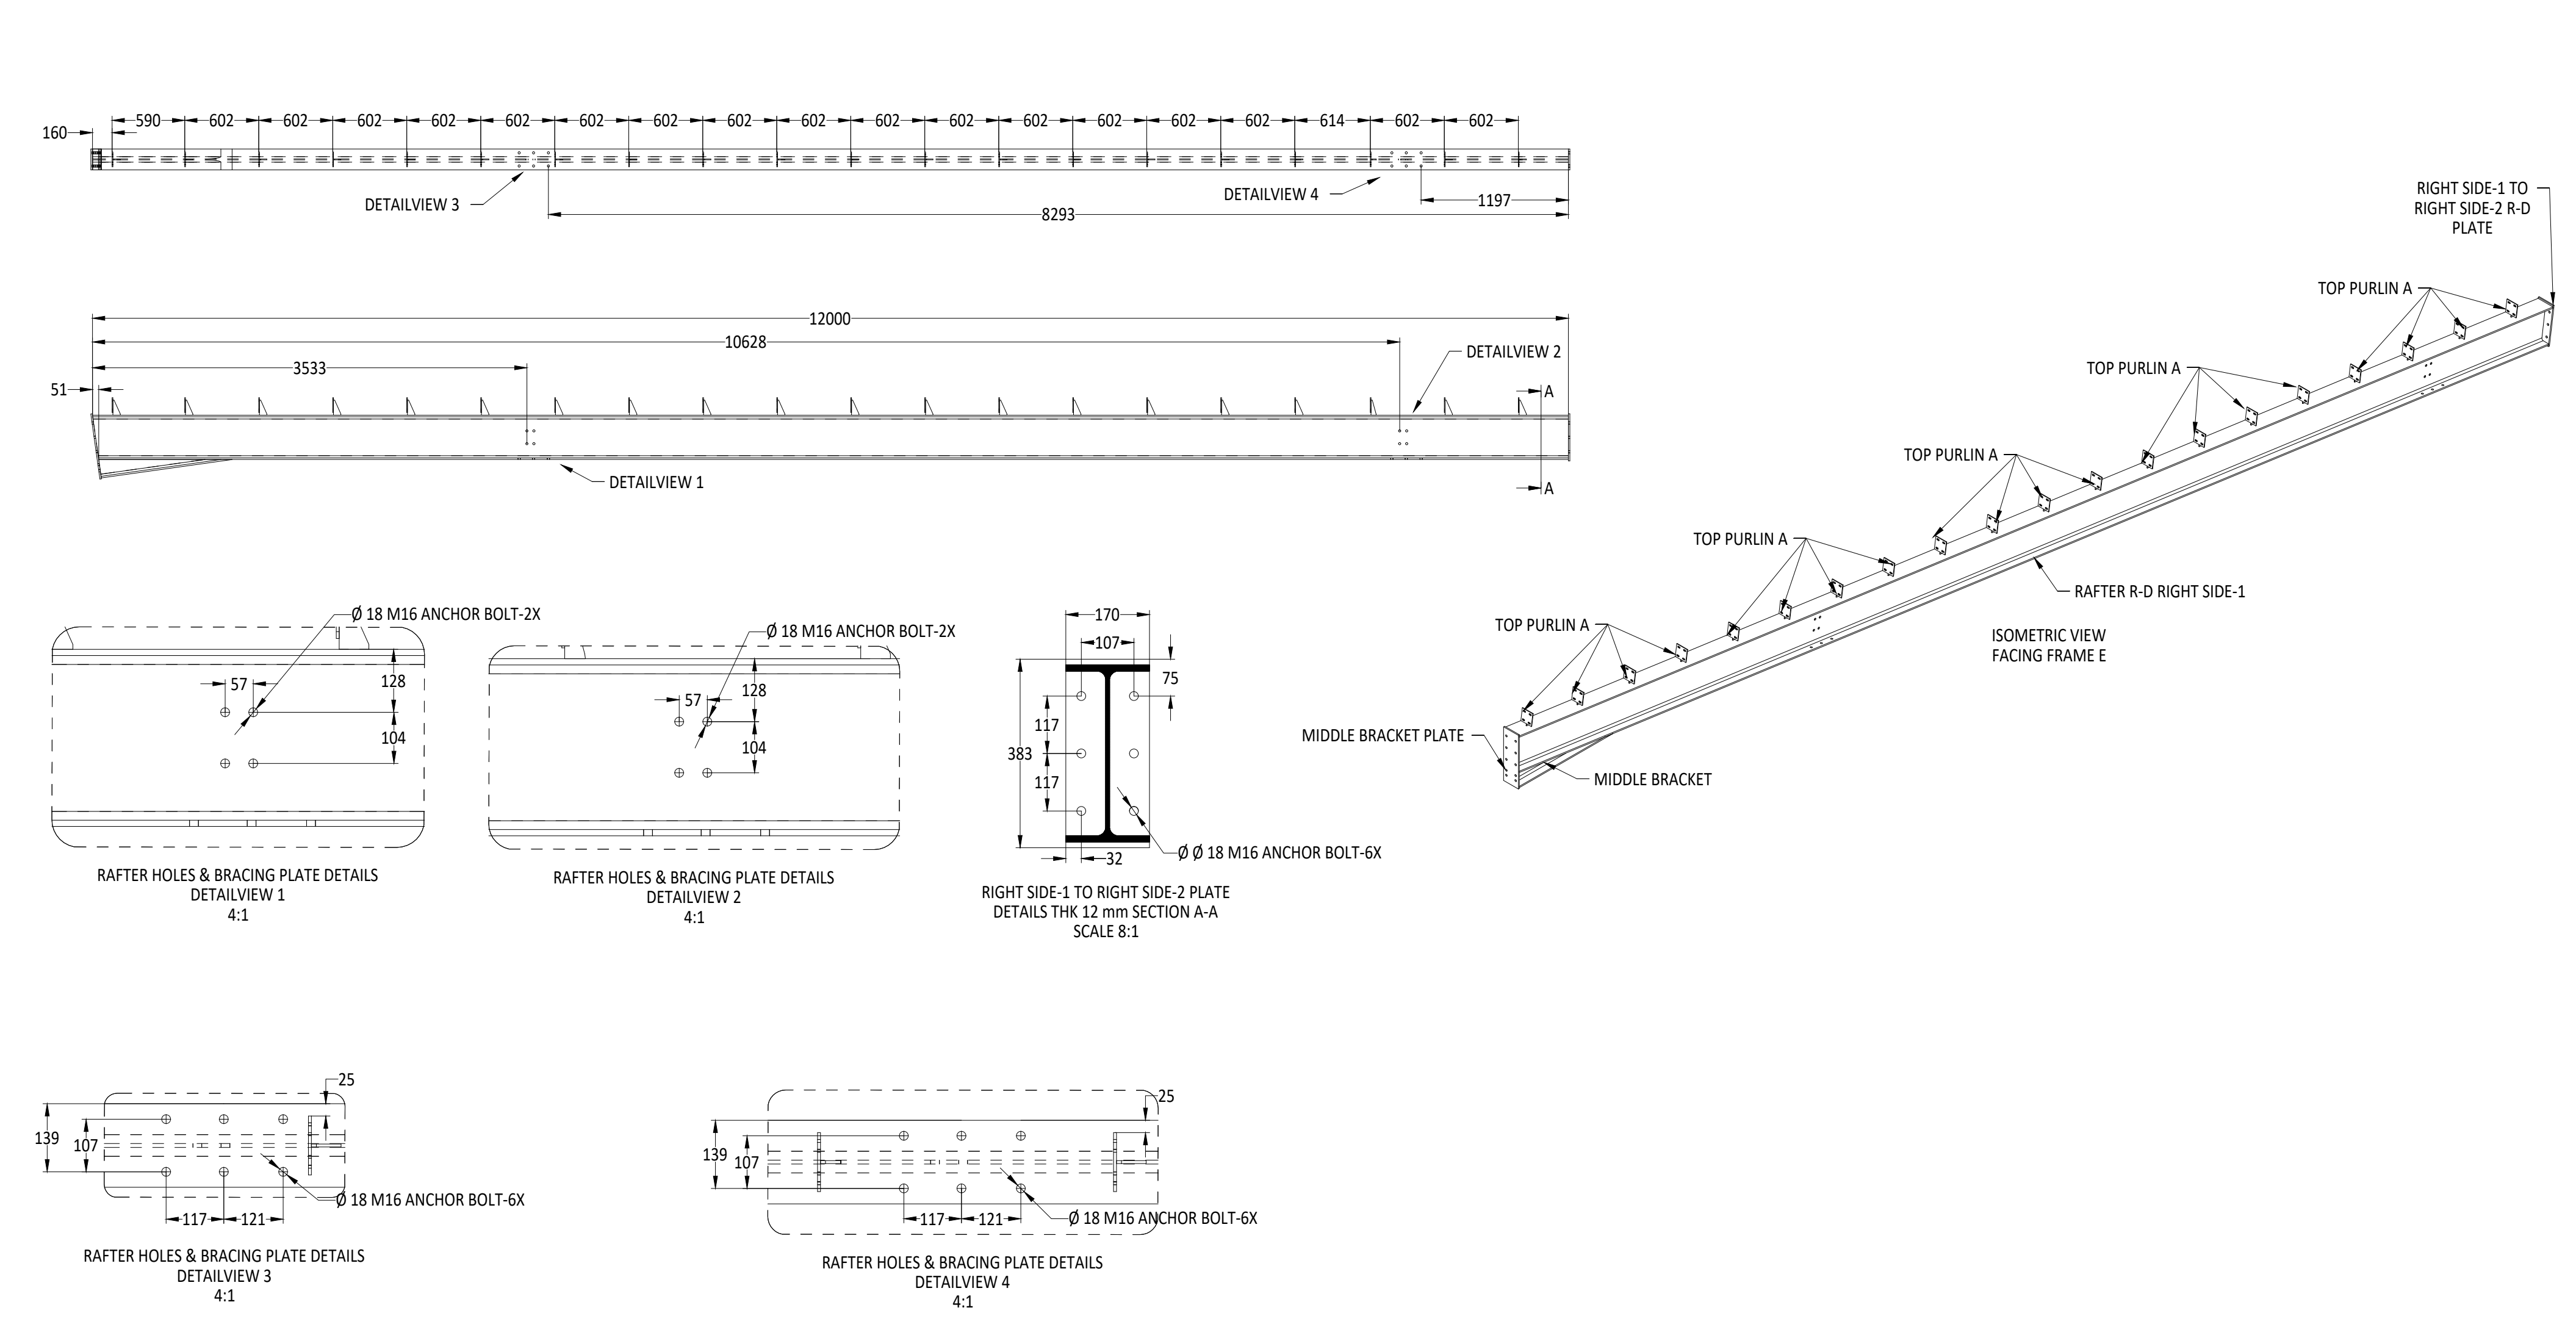

RAFTER R-D RIGHT SIDE-1 FABRICATION DETAILS

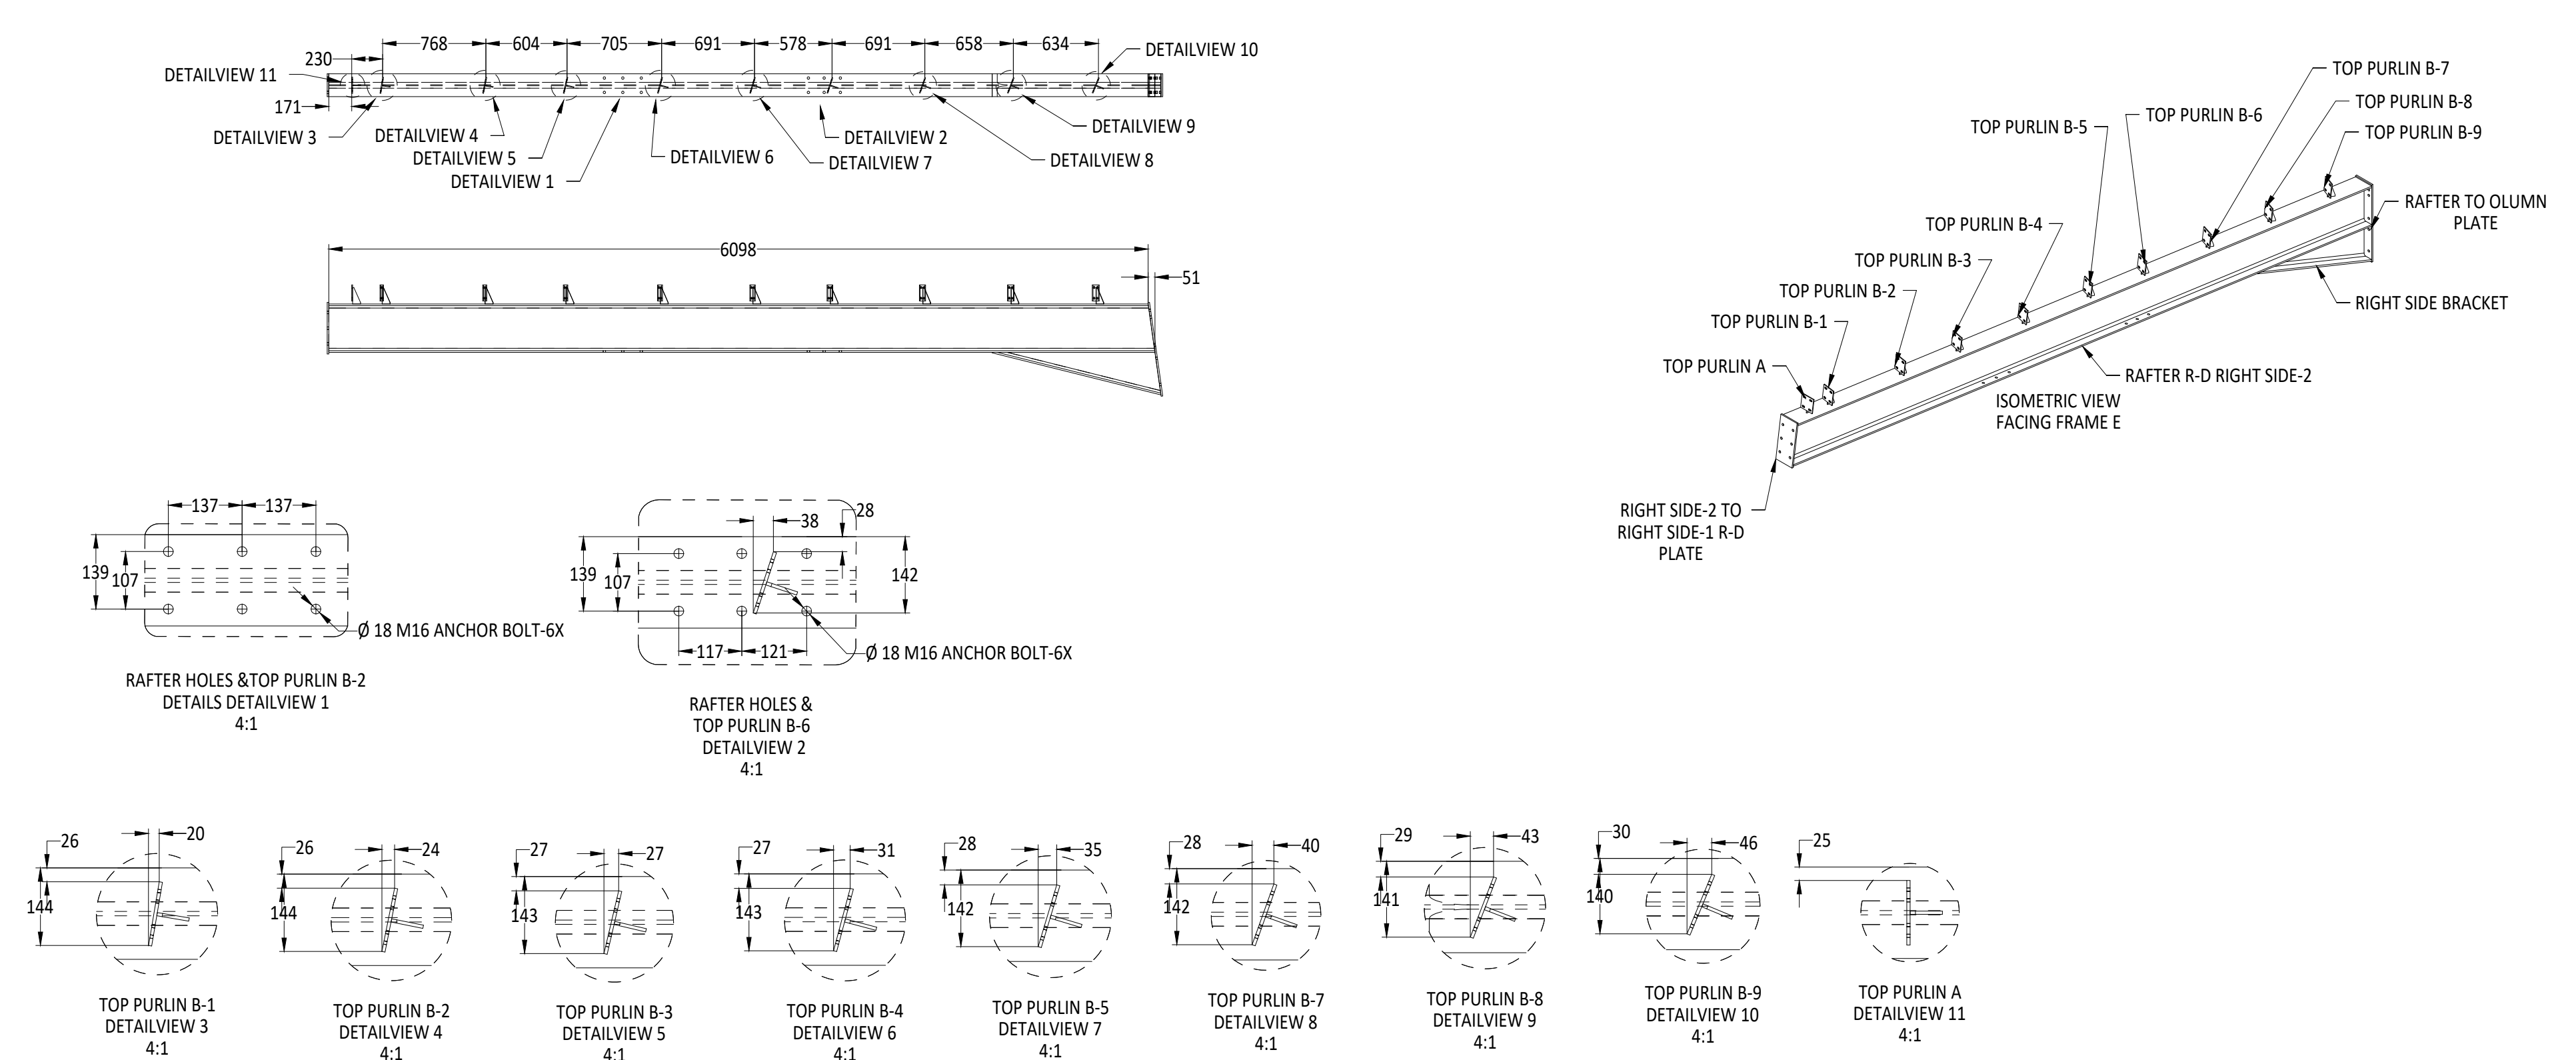


RAFTER R-D RIGHT SIDE-2 FABRICATION DETAILS

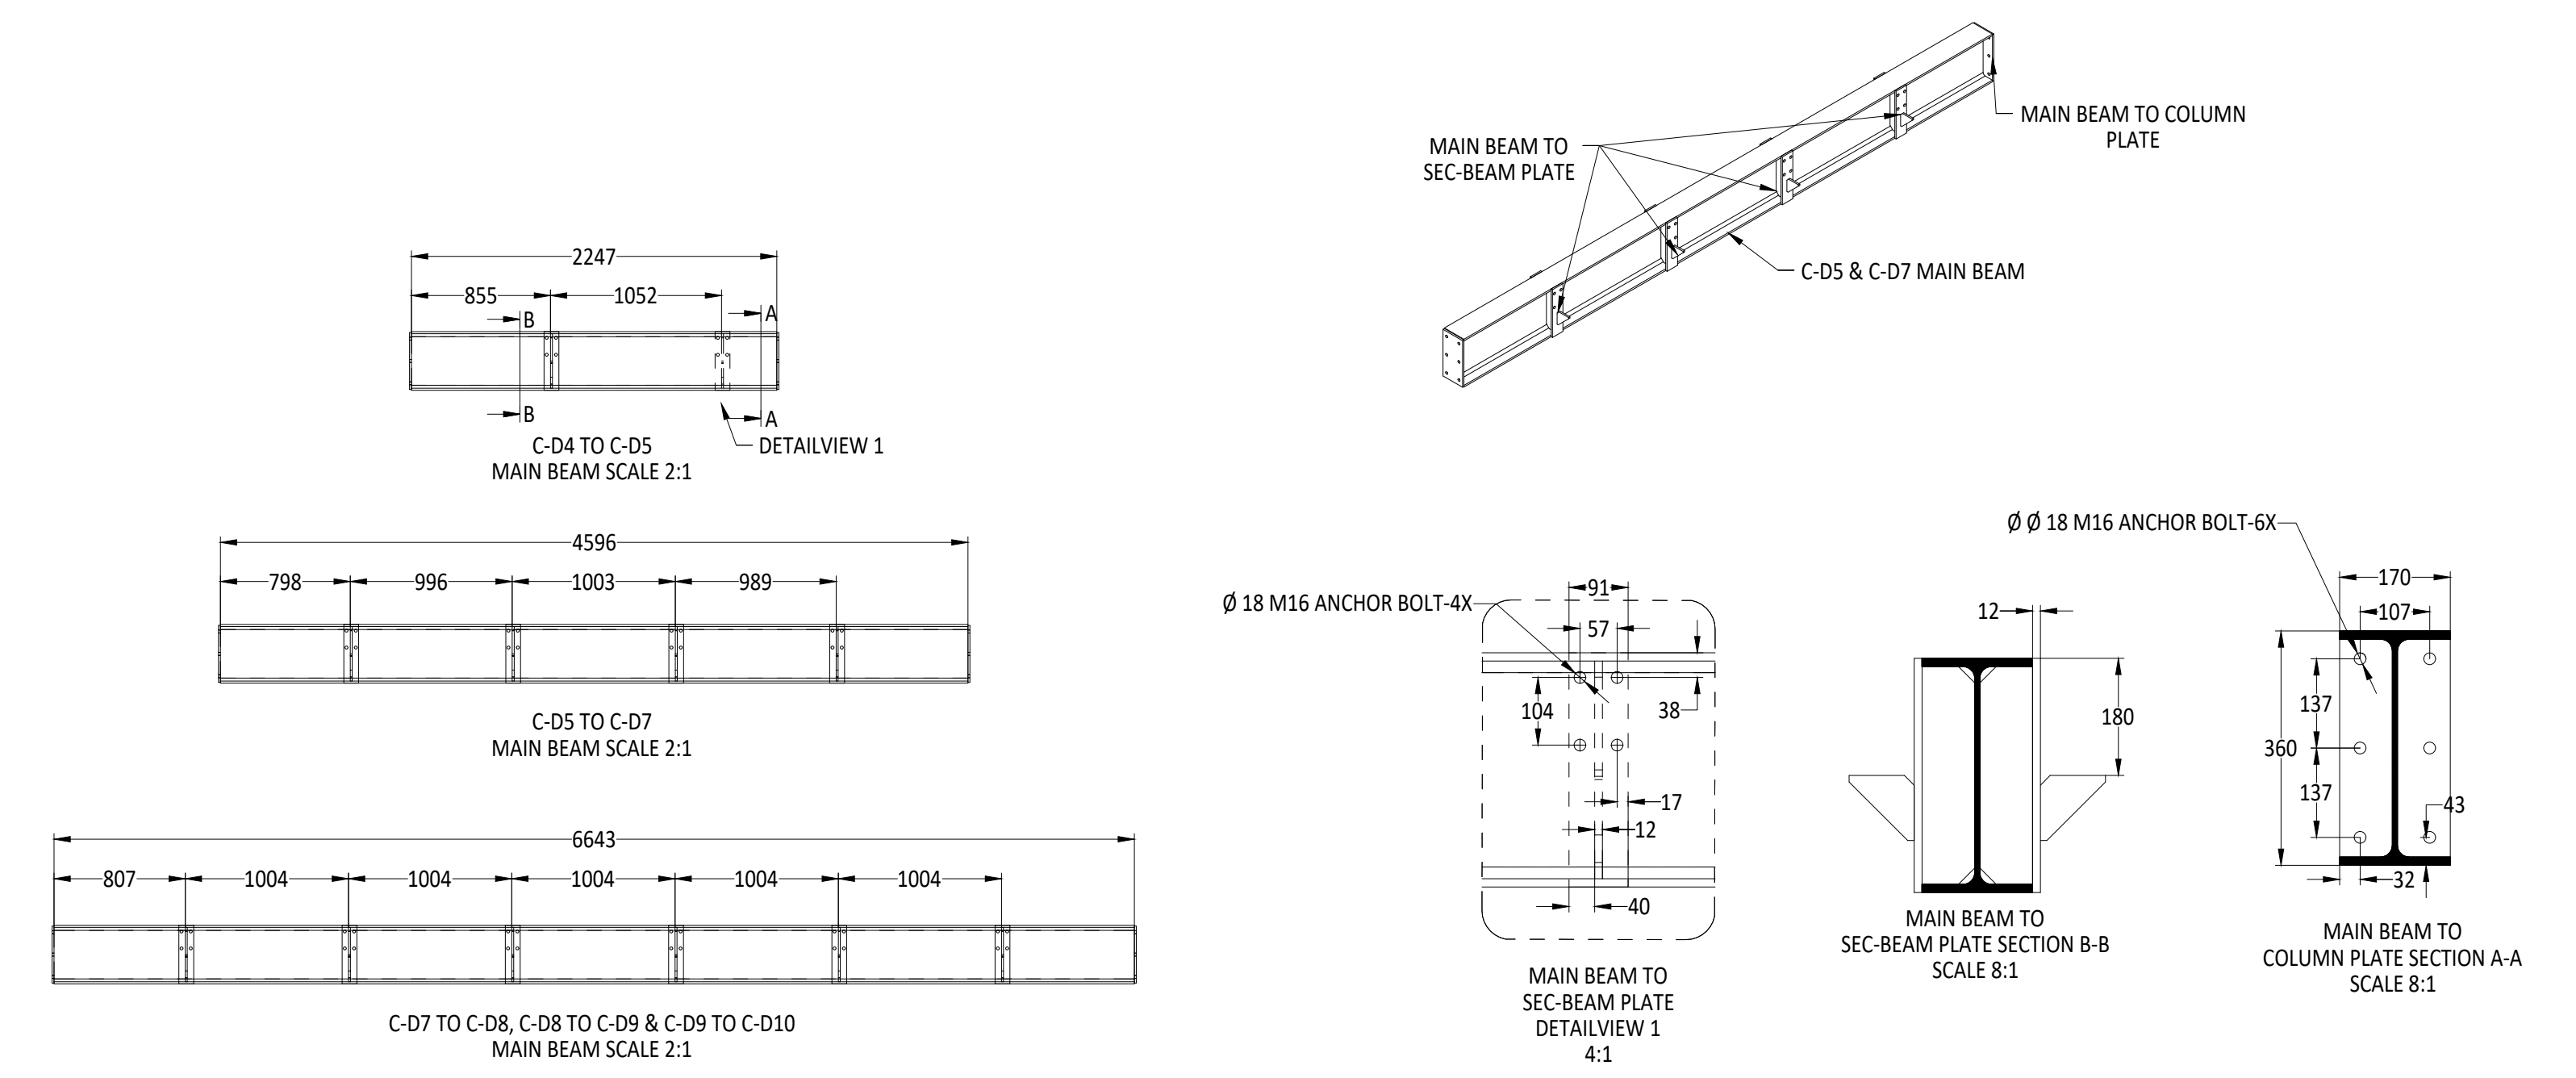

MAIN BEAMS FABRICATION DETAILS


ASSEMBLY NO.		TITLE			
PART NO.		HANGER FRAME-D FABRICATION DETAILS			
DESIGNER		SIZE	DWG NO	REV	
APPROVED		SCALE AS SHOWN	RELEASE DATE	WEIGHT Kg.	QTY.
			21/08/2025		

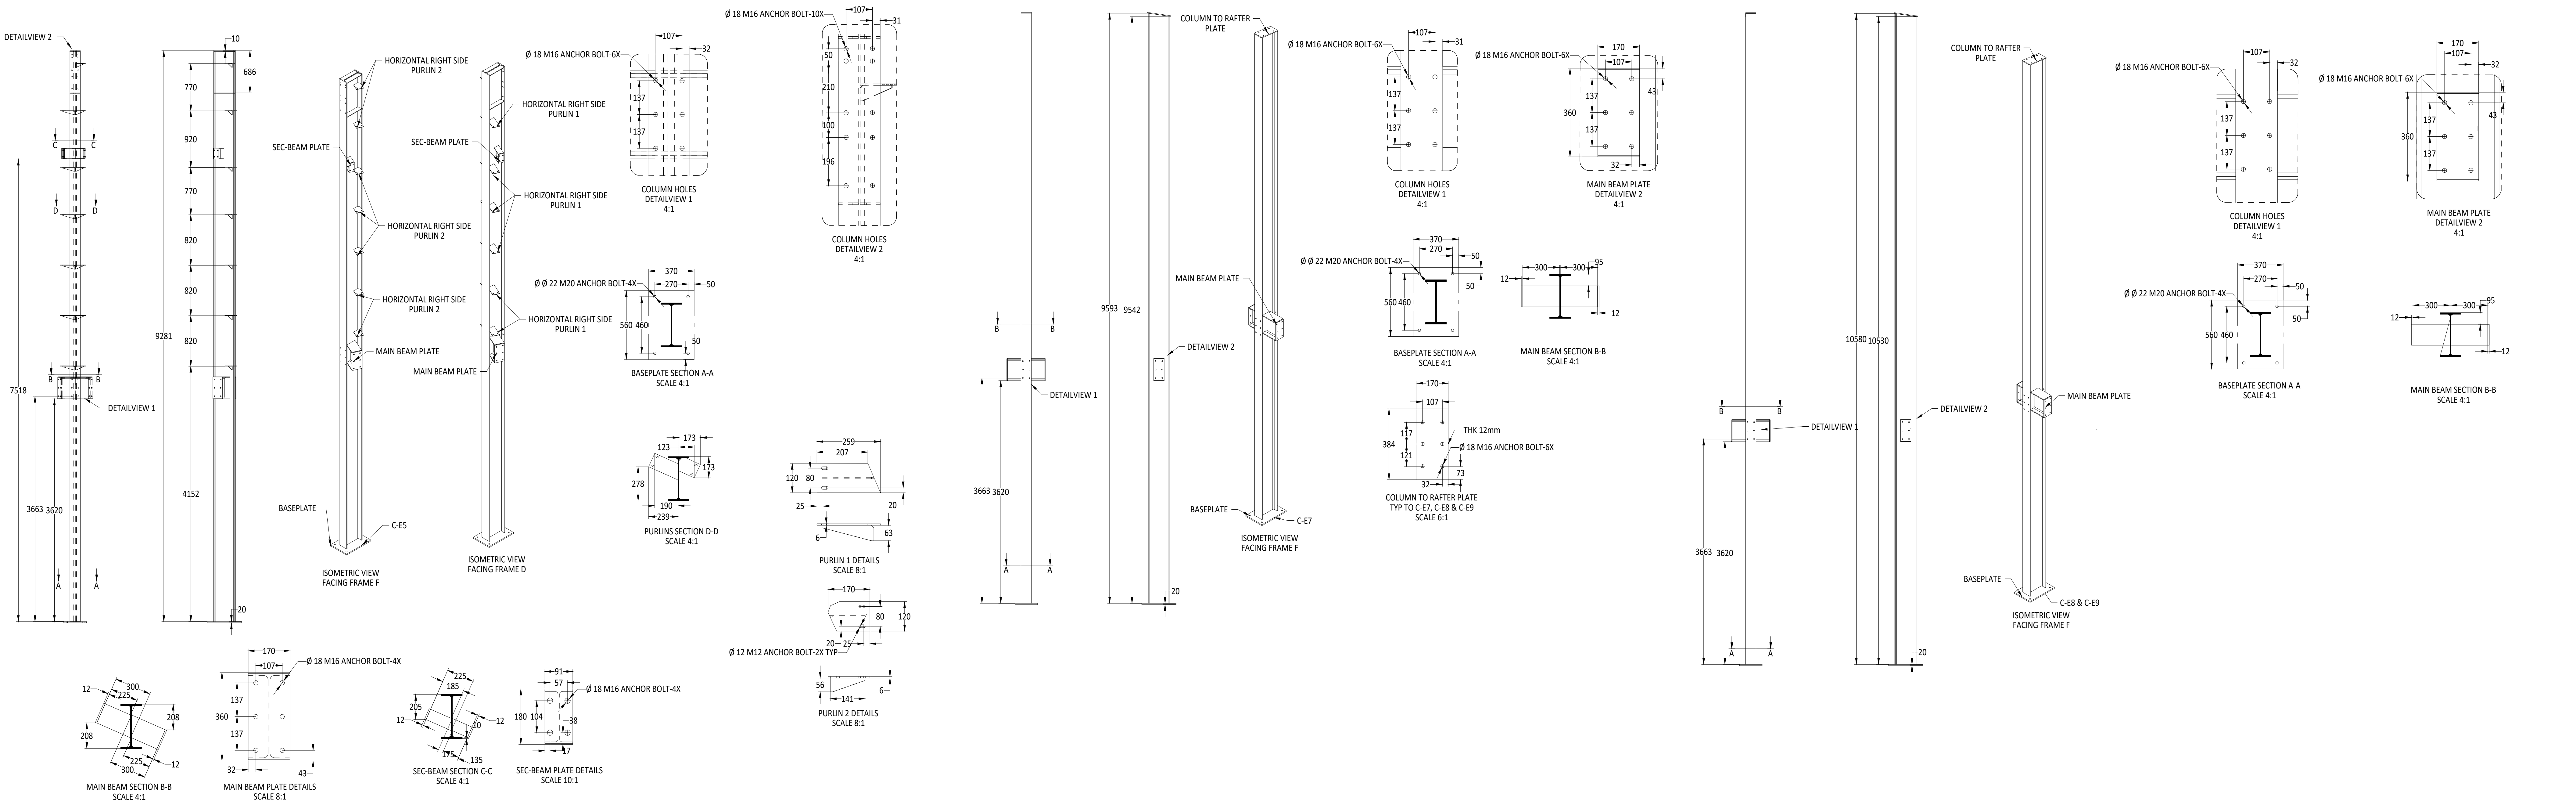


COLUMN C-E5 FABRICATION DETAILS

COLUMN C-E7 FABRICATION DETAILS

COLUMN C-E8 & C-E9 FABRICATION DETAILS

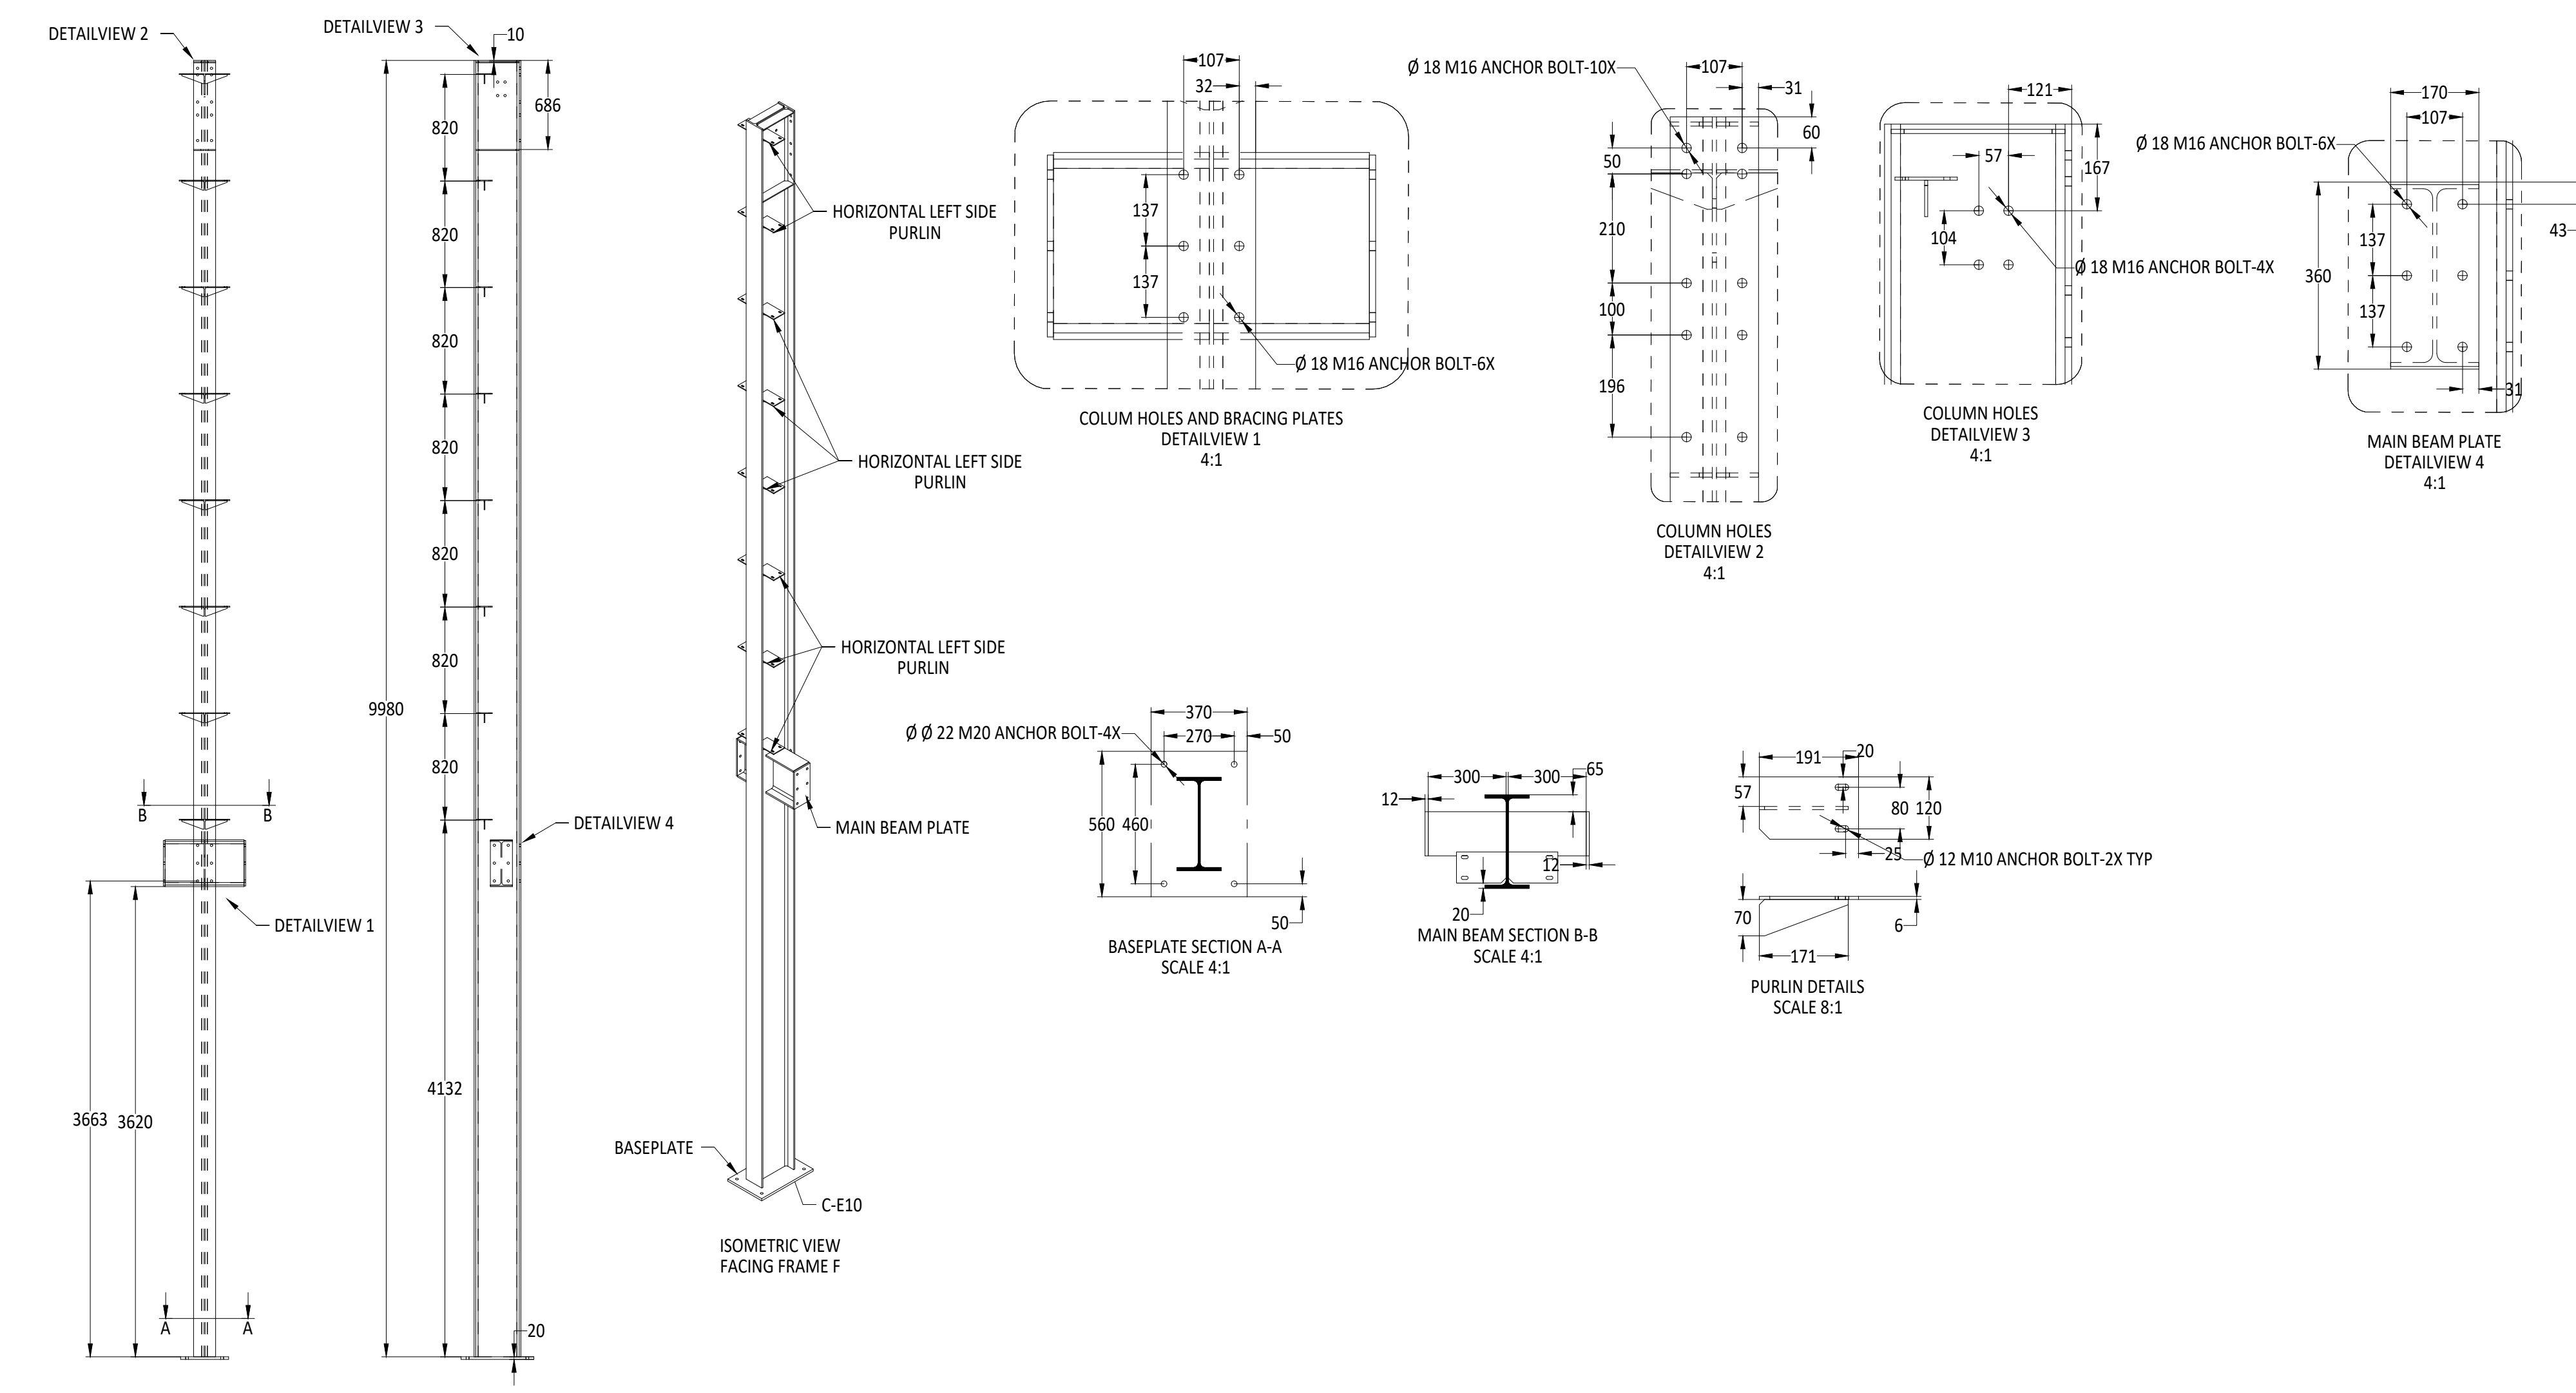


COLUMN C-E10 FABRICATION DETAILS
FRAME-E FABRICATION DETAILS

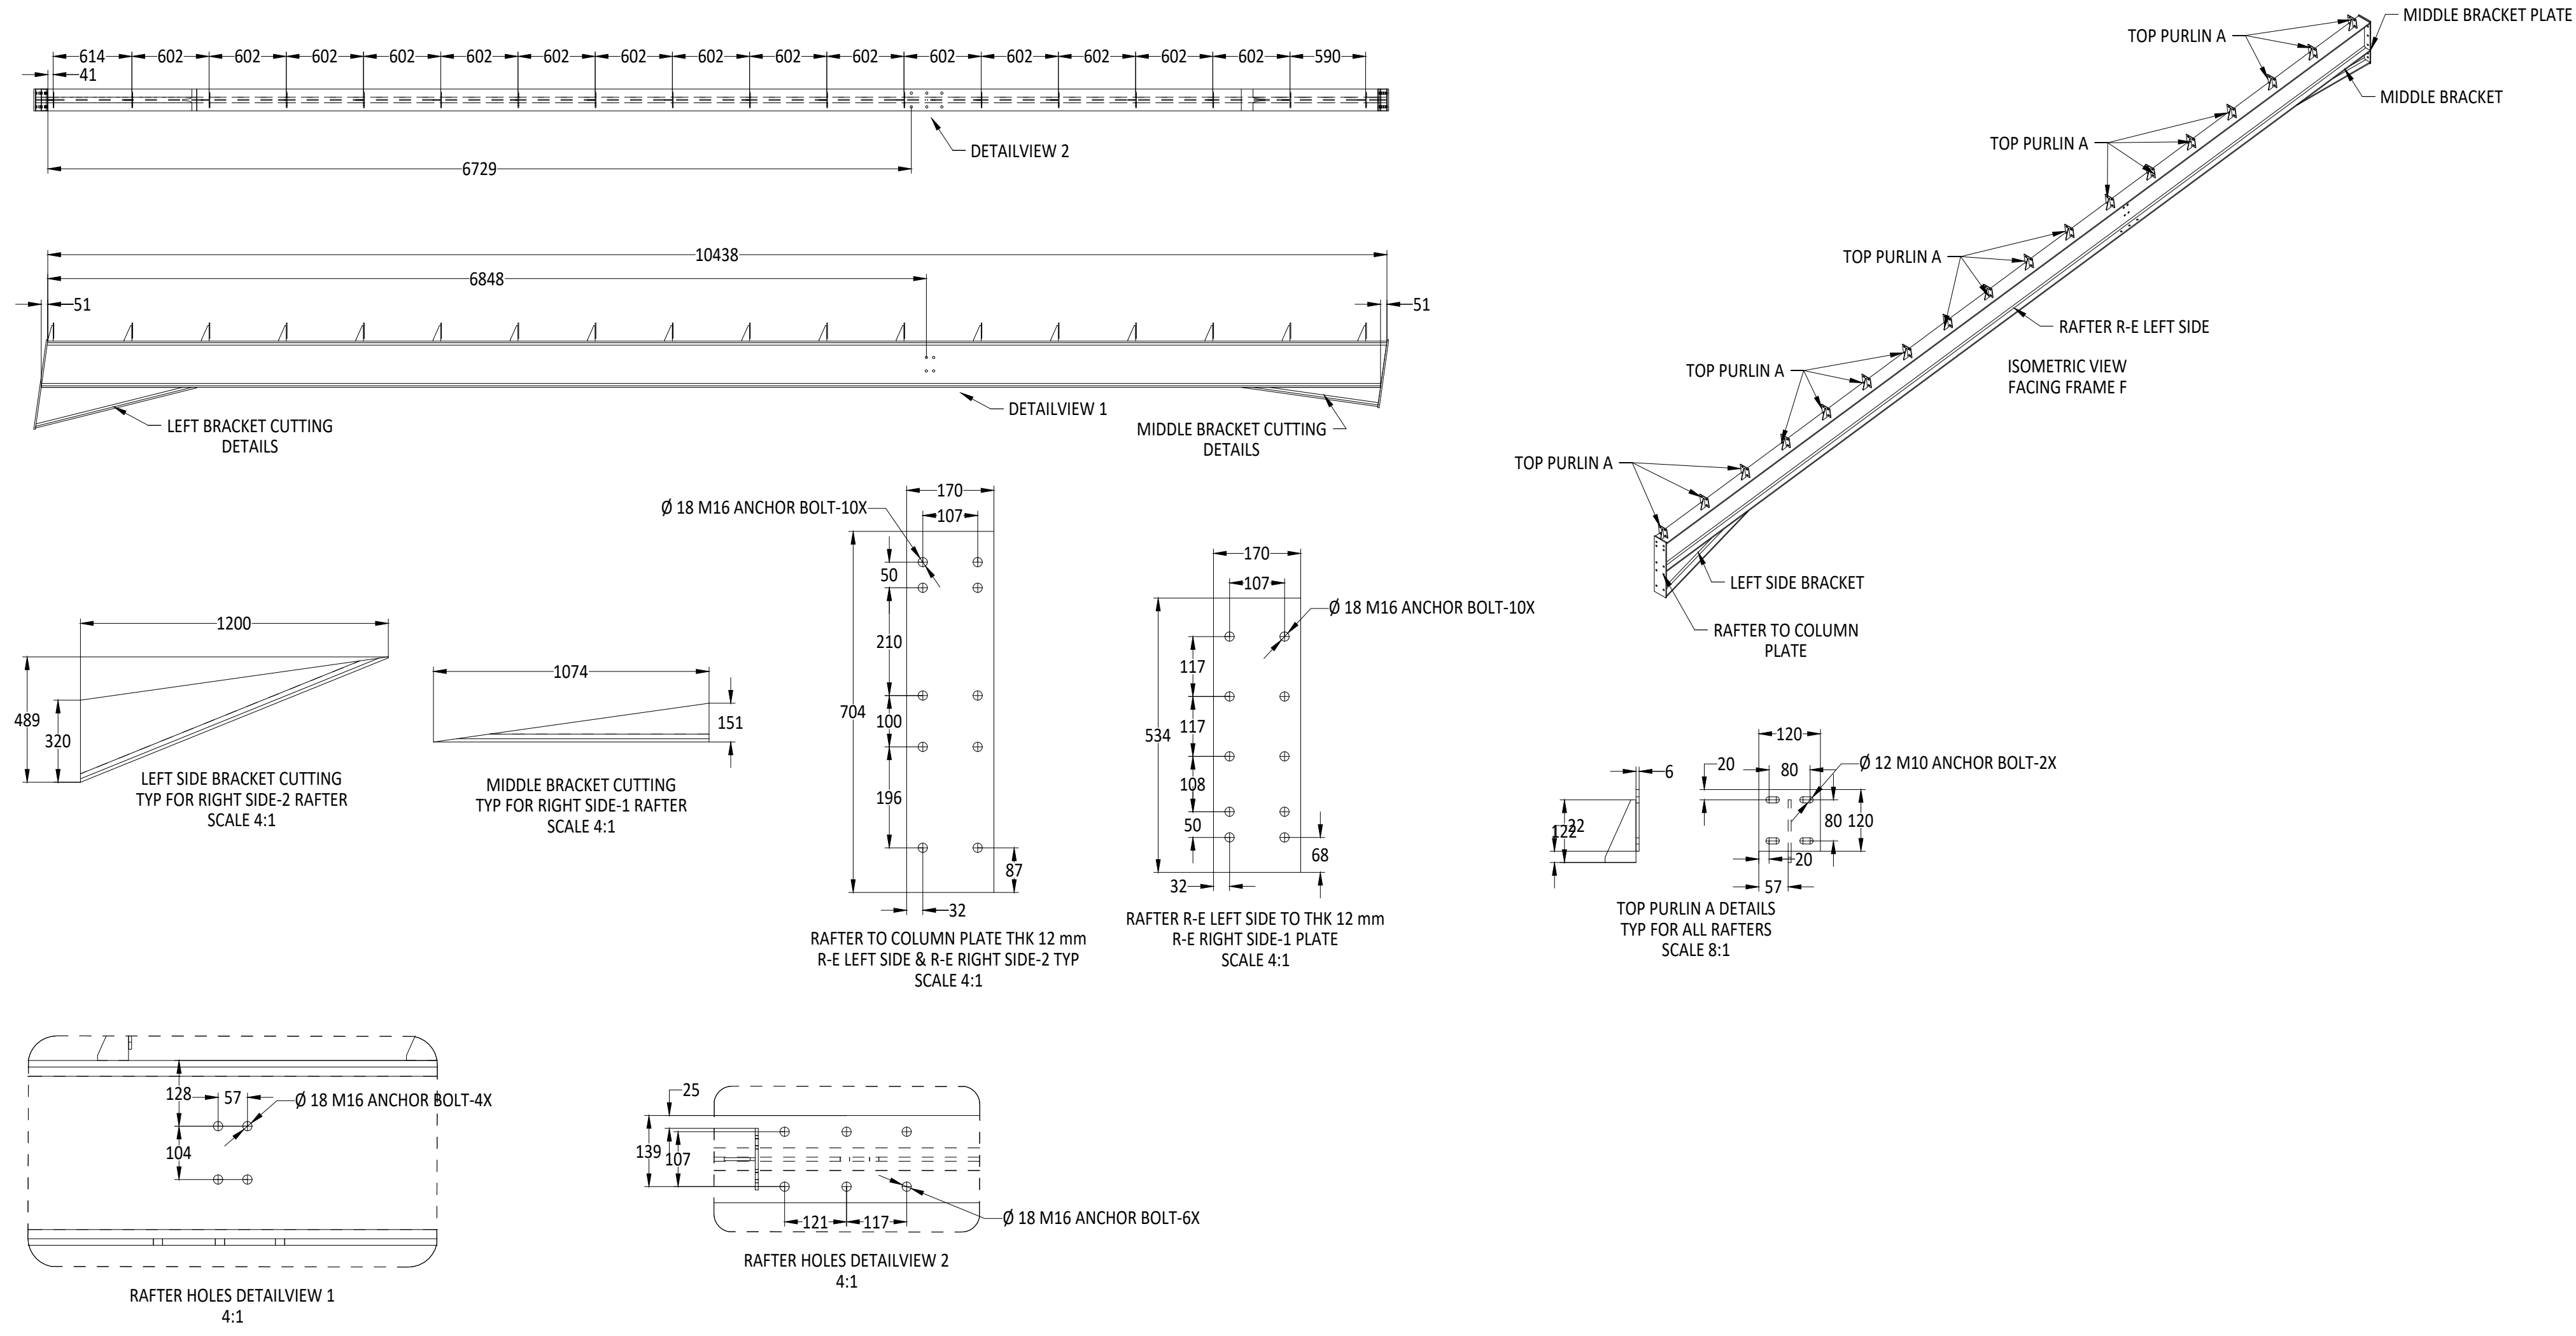


RAFTER R-E LEFT SIDE
FABRICATION DETAILS

ASSEMBLY NO.		TITLE			
PART NO.		HANGER FRAME-E FABRICATION DETAILS			
DESIGNER		SIZE	DWG NO	REV	
APPROVED		A0		00	
		RELEASE DATE	WEIGHT Kg.	QTY.	
		21/08/2025			
		SCALE AS SHOWN			

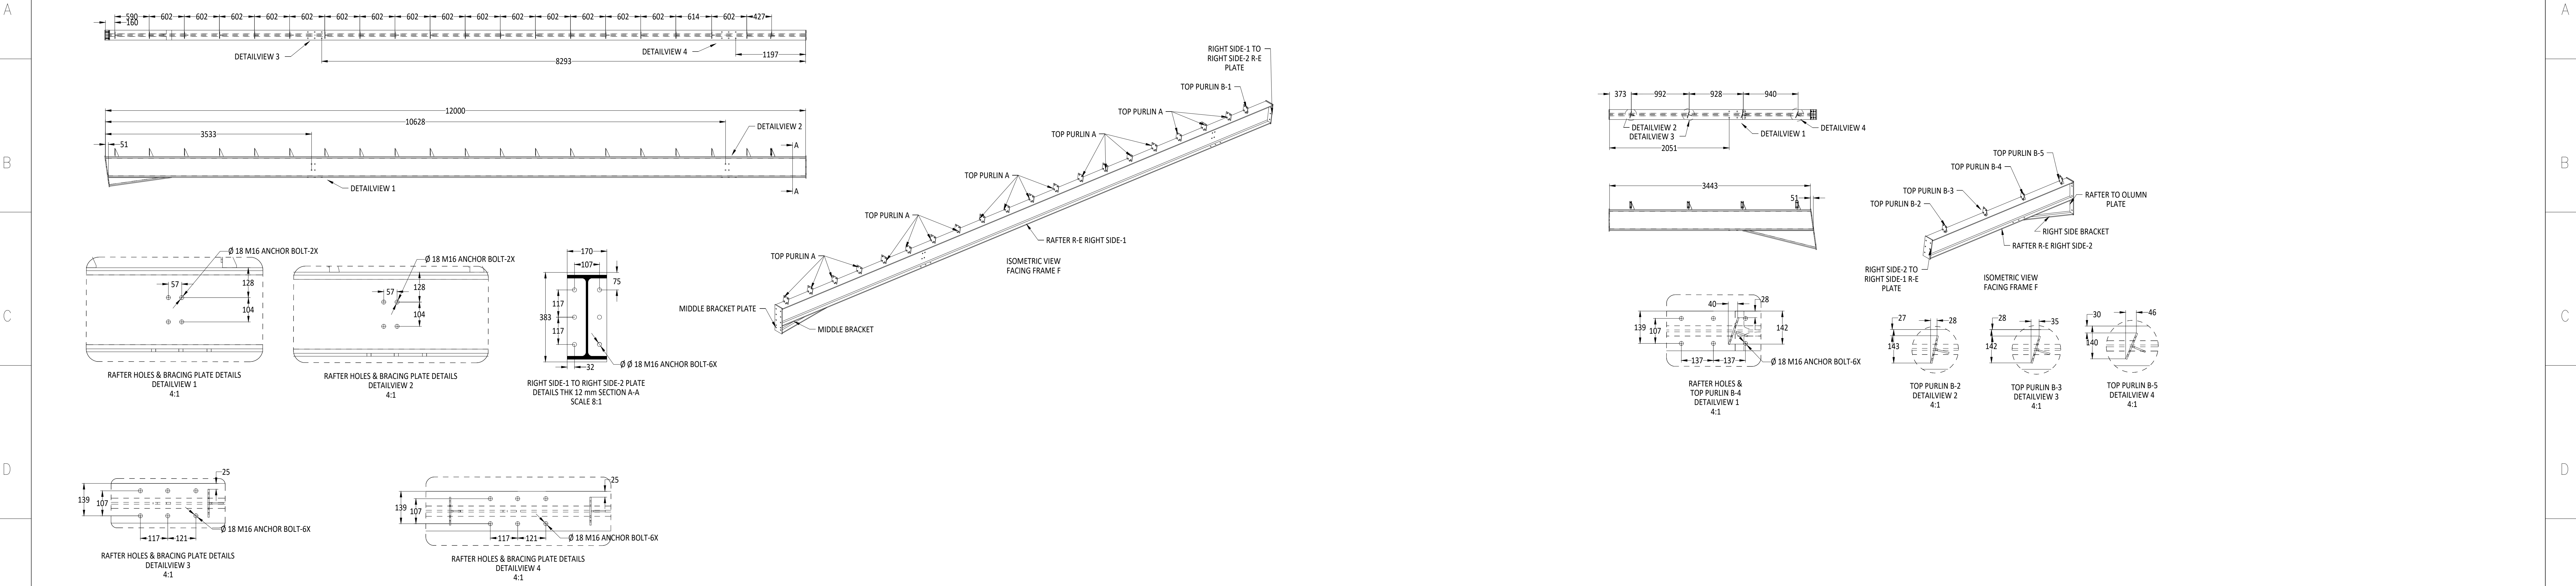


RAFTER R-E RIGHT SIDE-1 FABRICATION DETAILS

RAFTER R-E RIGHT SIDE-2 FABRICATION DETAILS

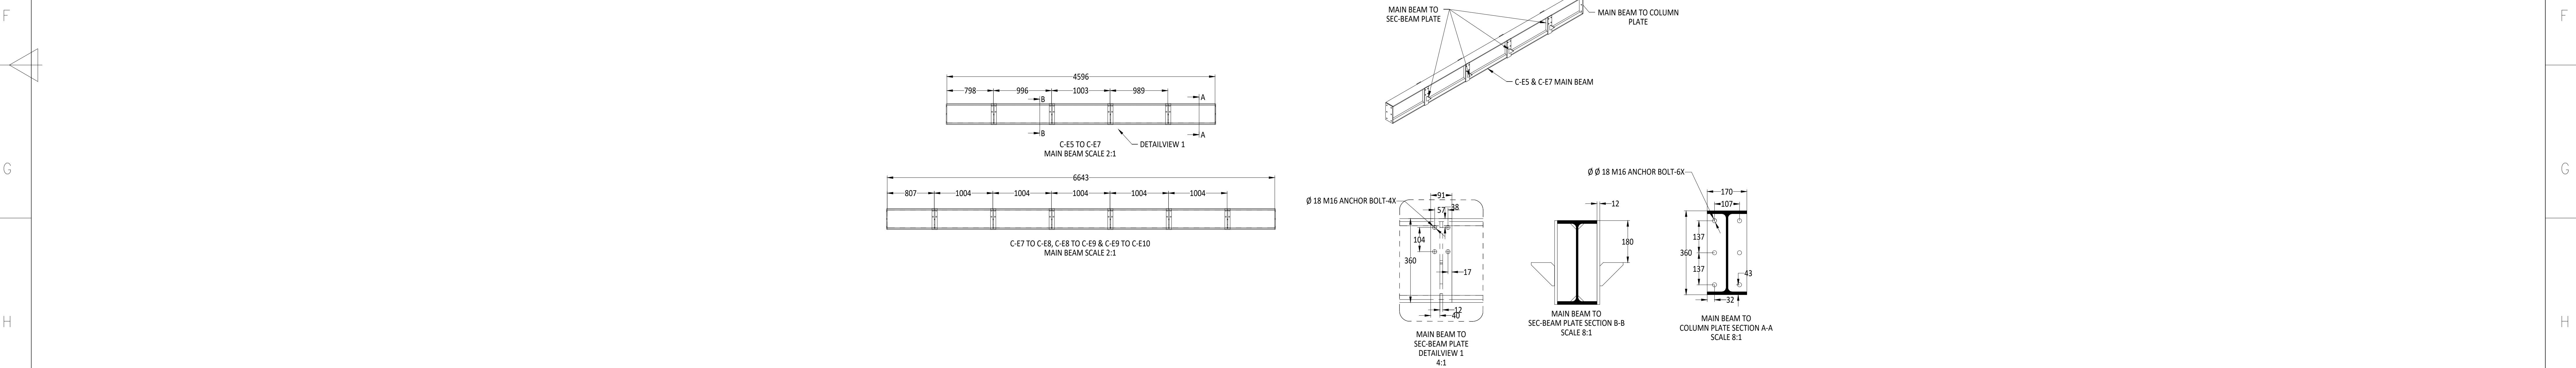

MAIN BEAMS FABRICATION DETAILS


DATE	
DWG NO	
SH	
REV	
ASSEMBLY NO.	TITLE
PART NO.	HANGER FRAME-E FABRICATION DETAILS
DESIGNER	SIZE A0
APPROVED	SCALE AS SHOWN
	RELEASE DATE 21/08/2025
	WEIGHT Kg.
	QTY.
	REV 00

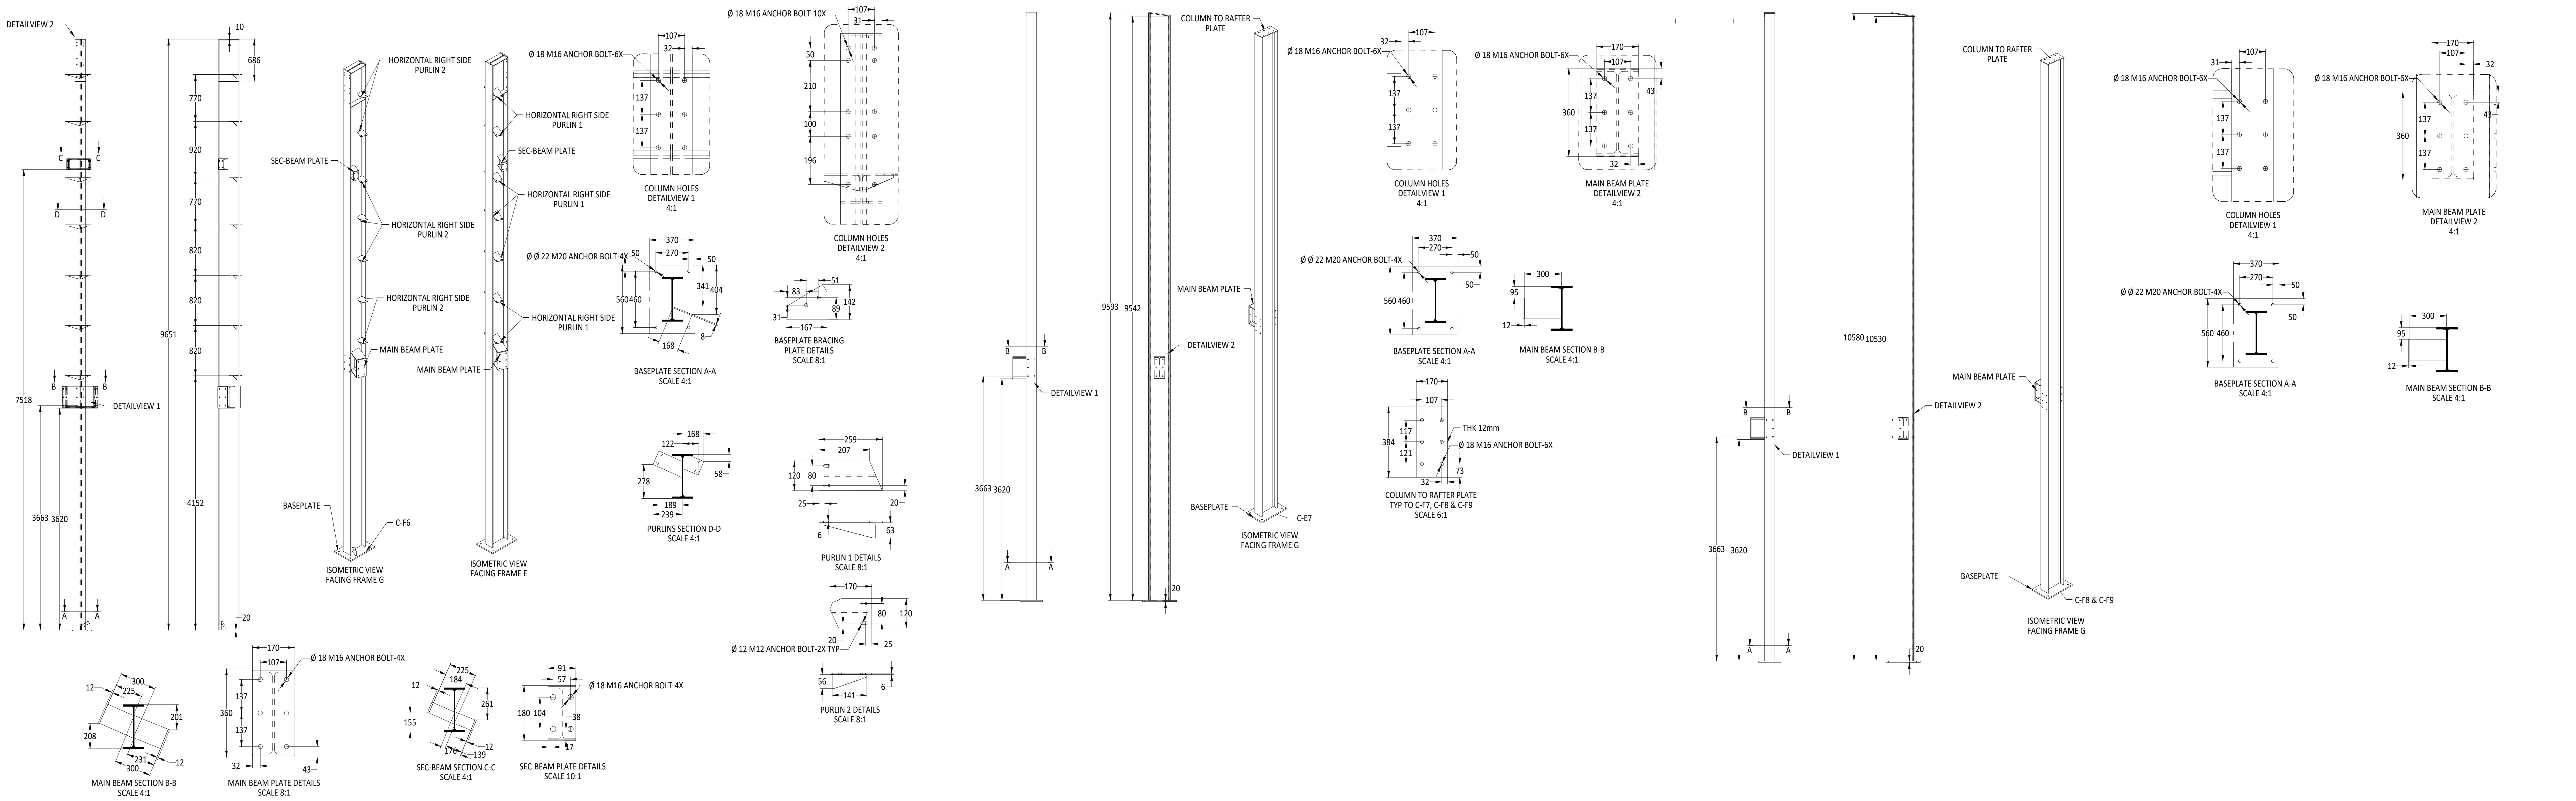


COLUMN C-F6 FABRICATION DETAILS

COLUMN C-F7 FABRICATION DETAILS

COLUMN C-F8 & C-F9 FABRICATION DETAILS

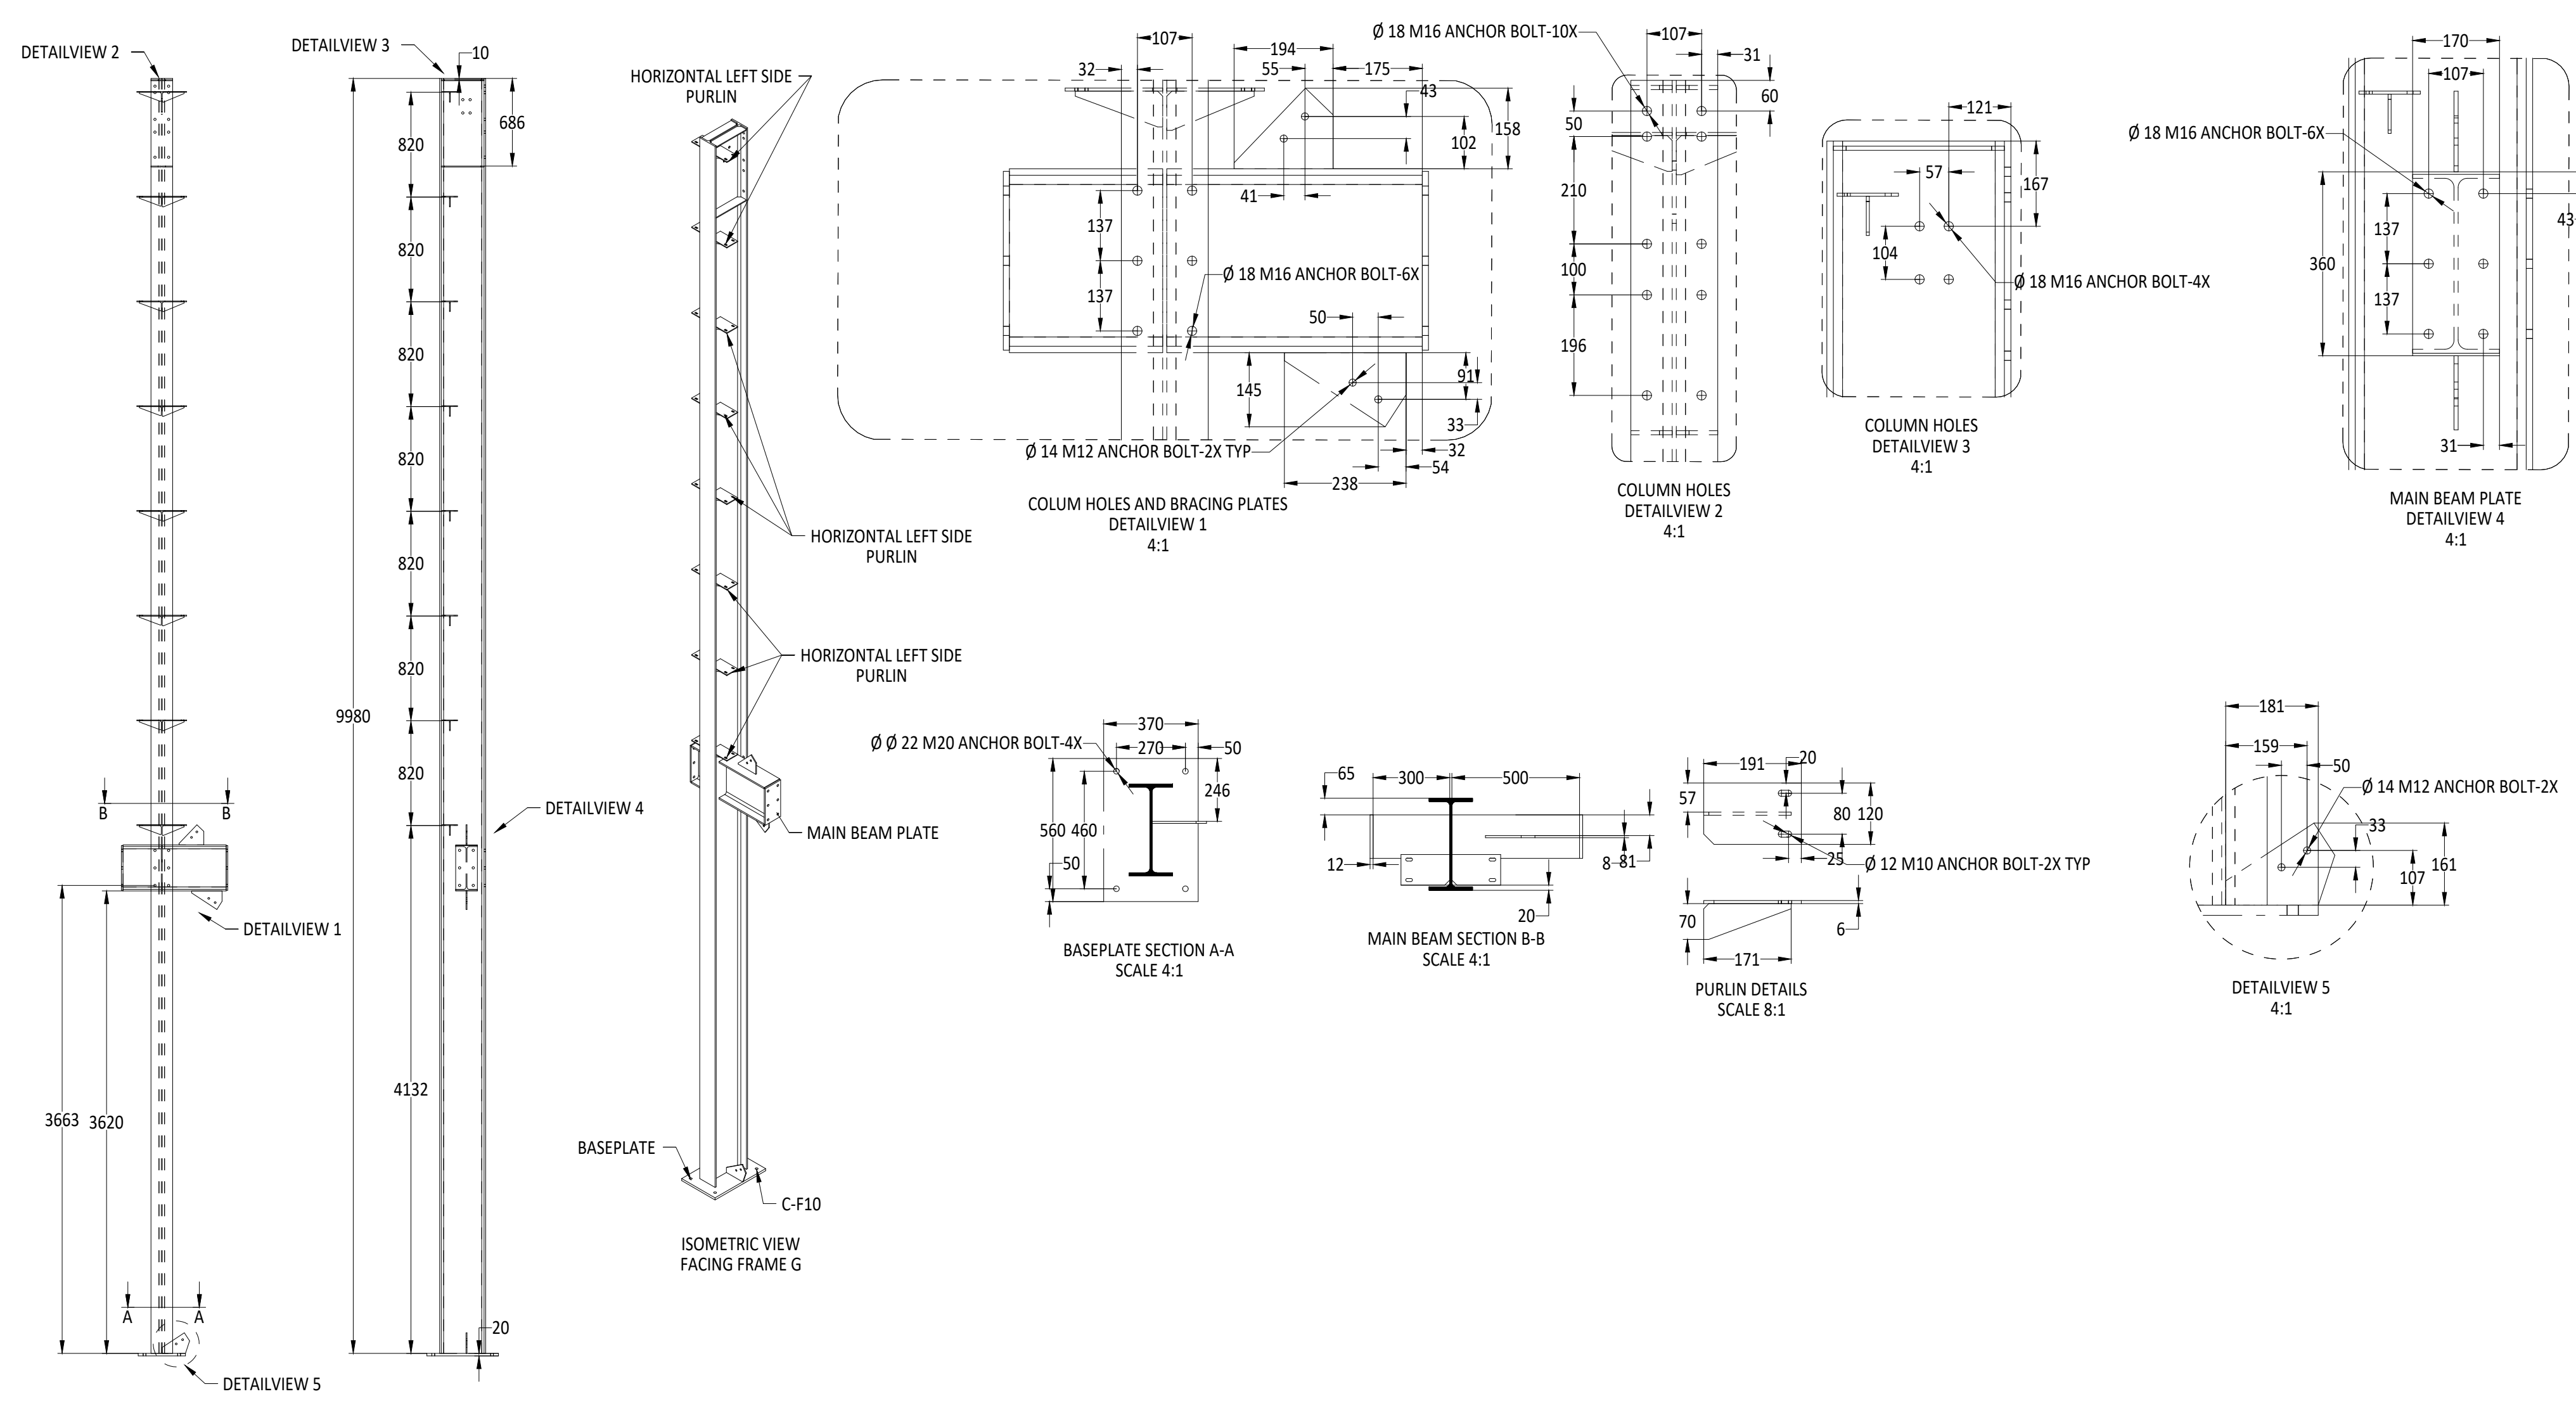


COLUMN C-F10 FABRICATION DETAILS
FRAME-F FABRICATION DETAILS

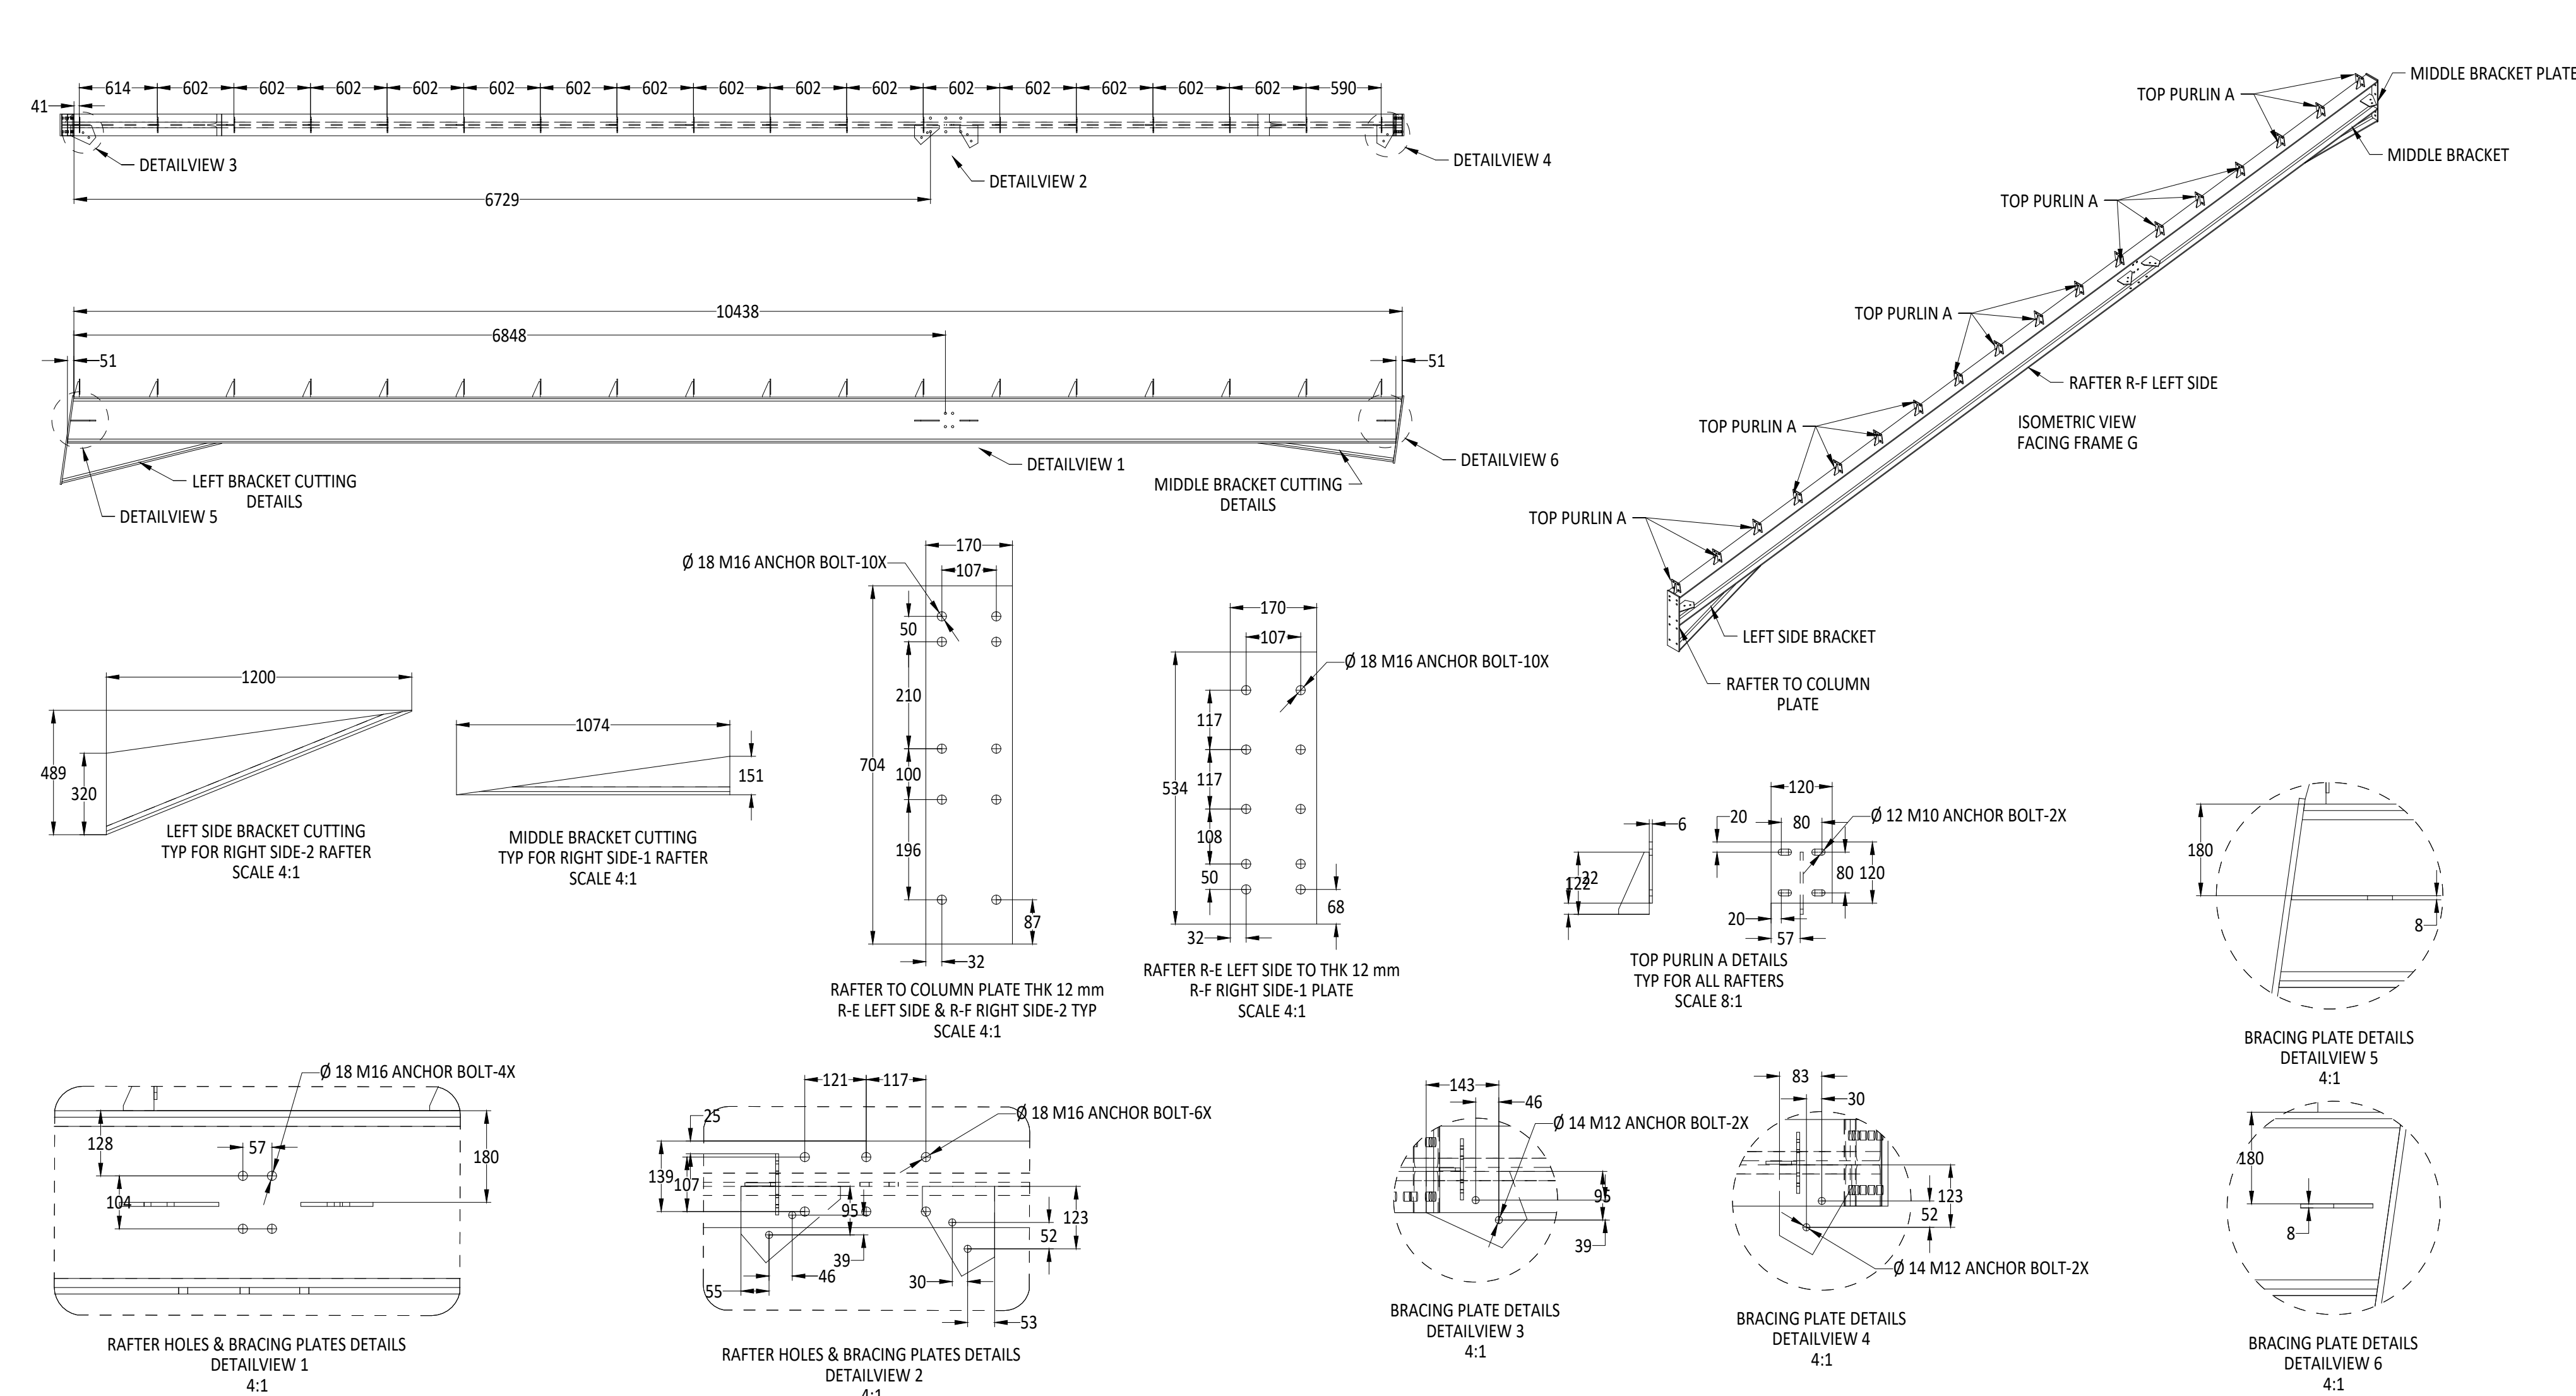

RAFTER R-F LEFT SIDE
FABRICATION DETAILS


ASSEMBLY NO.		TITLE			
PART NO.		HANGER FRAME-F FABRICATION DETAILS			
DESIGNER		SIZE	DWG NO	REV	
APPROVED		A0		00	
SCALE AS SHOWN		21/08/2025	WEIGHT Kg.	QTY.	

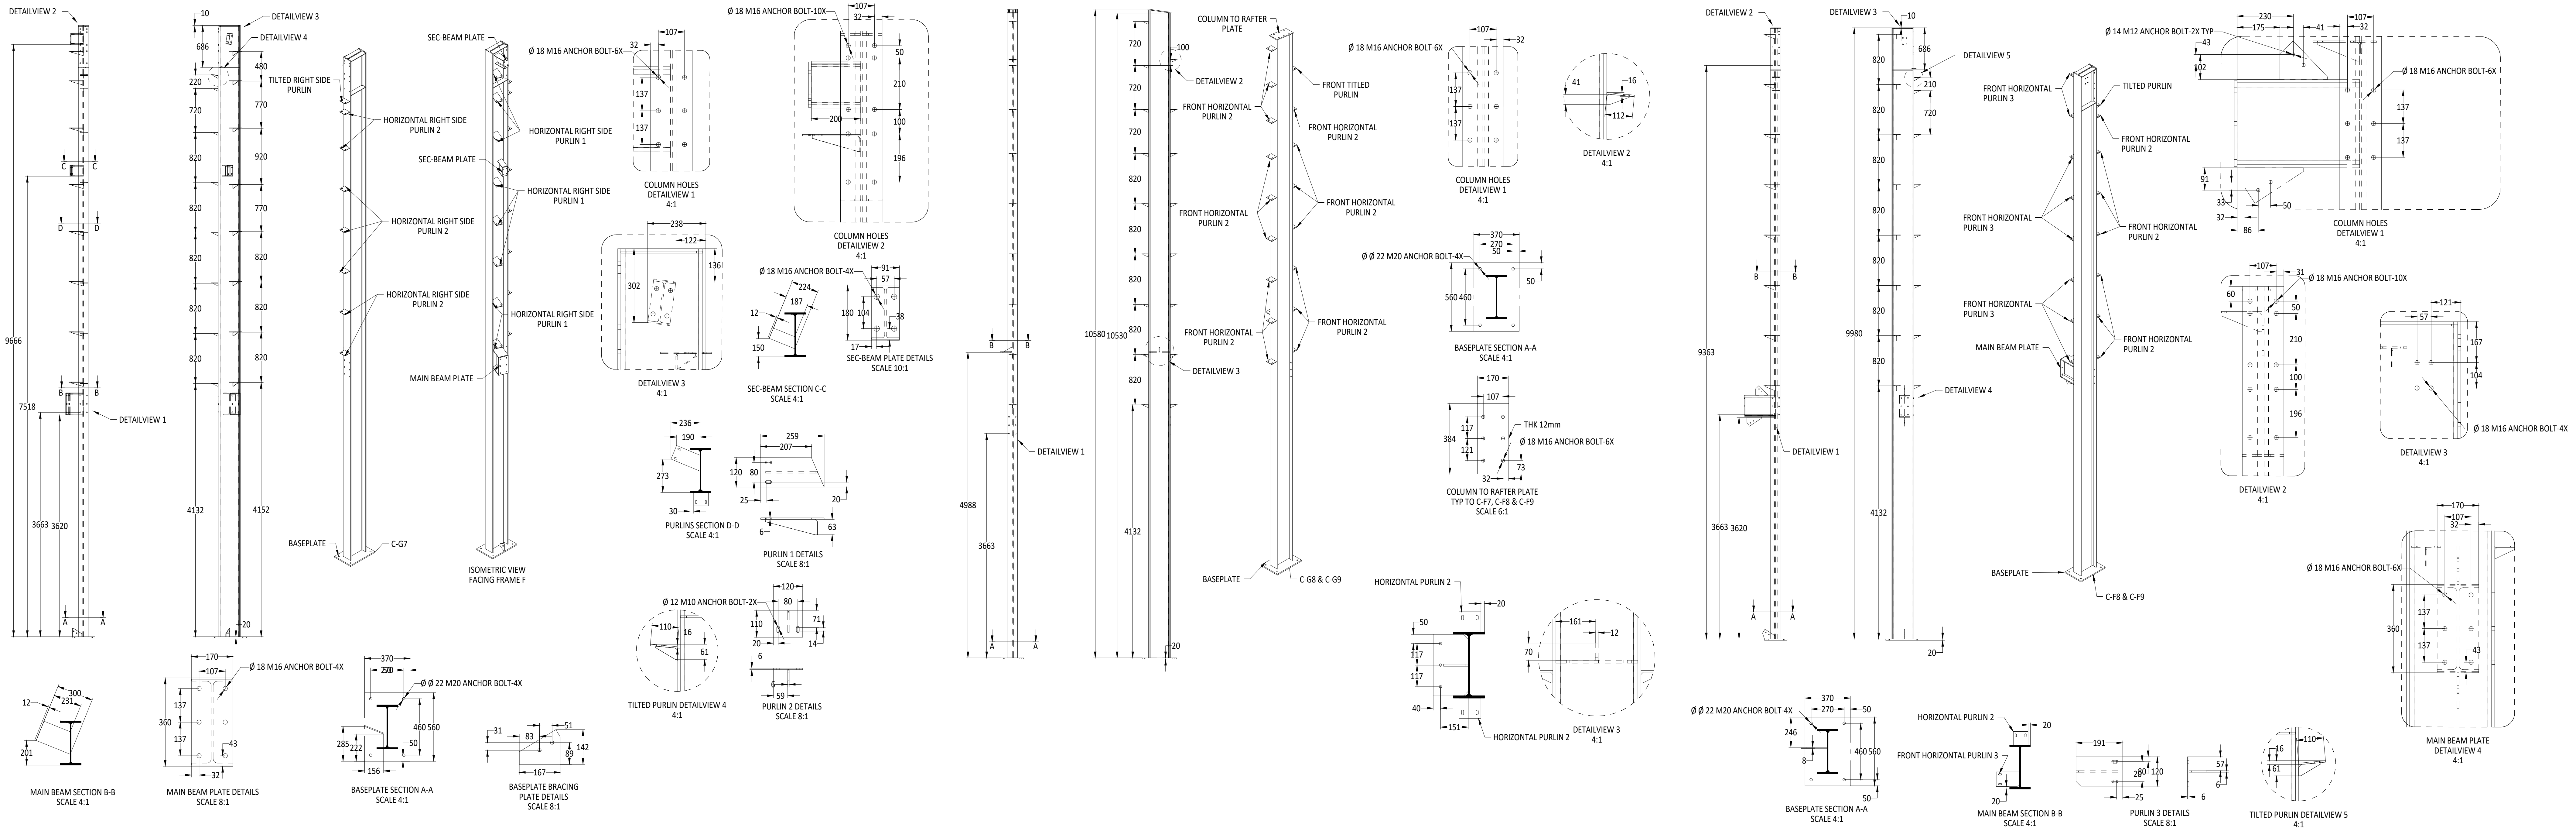


COLUMN C-G7 FABRICATION DETAILS

COLUMN C-G8 & C-G9 FABRICATION DETAILS


COLUMN C-G10 FABRICATION DETAILS

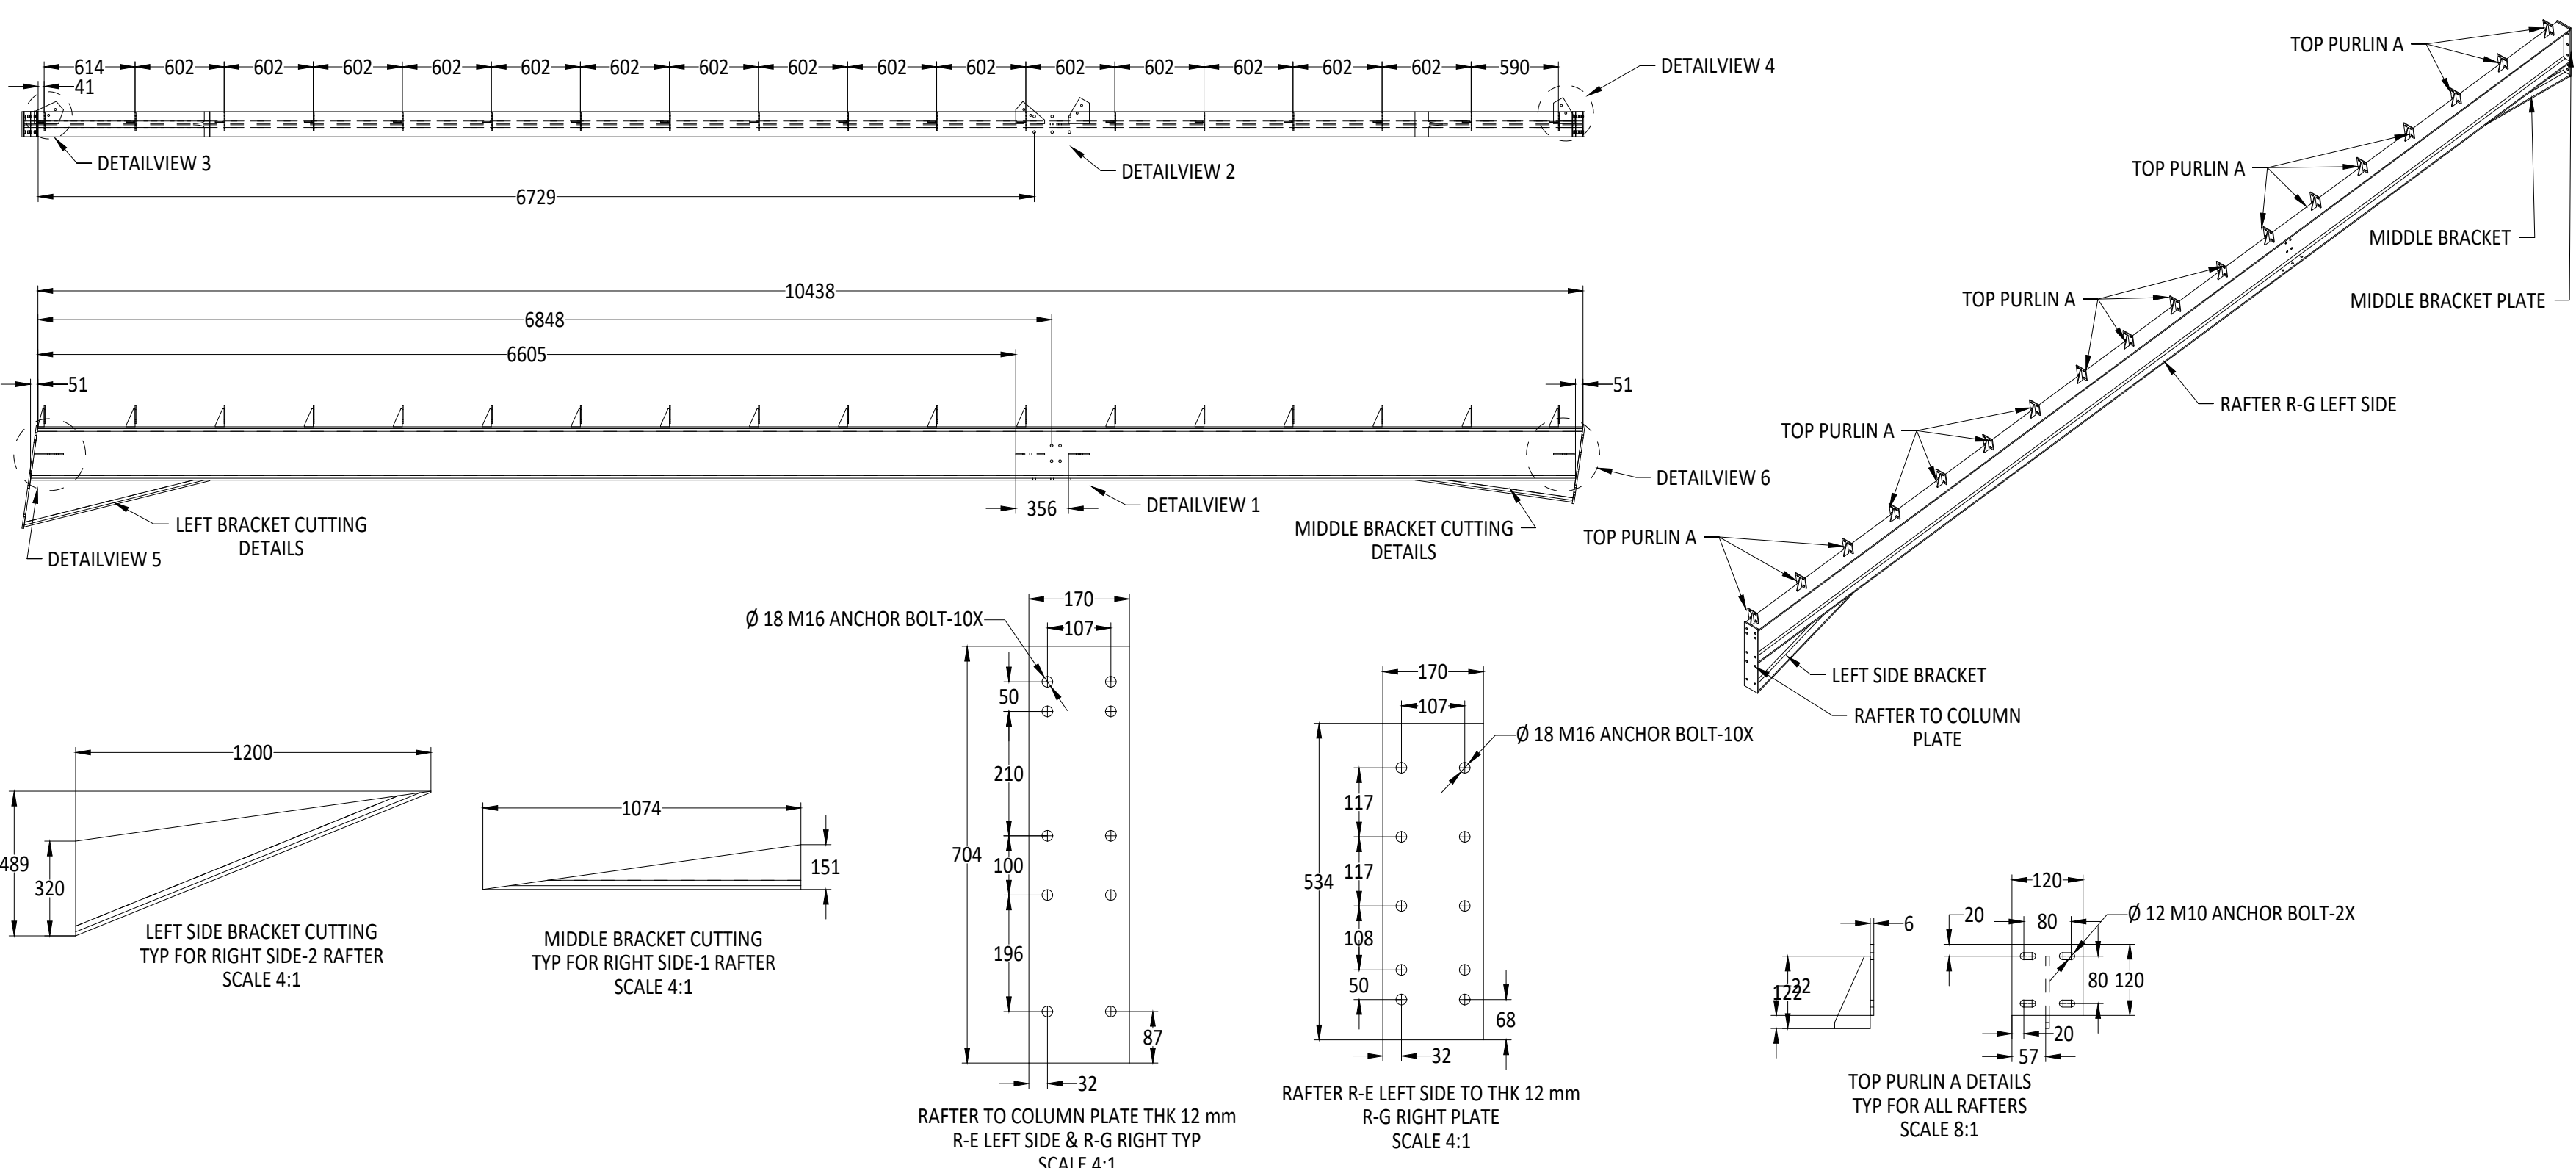

RAFTER R-G LEFT SIDE FABRICATION DETAILS

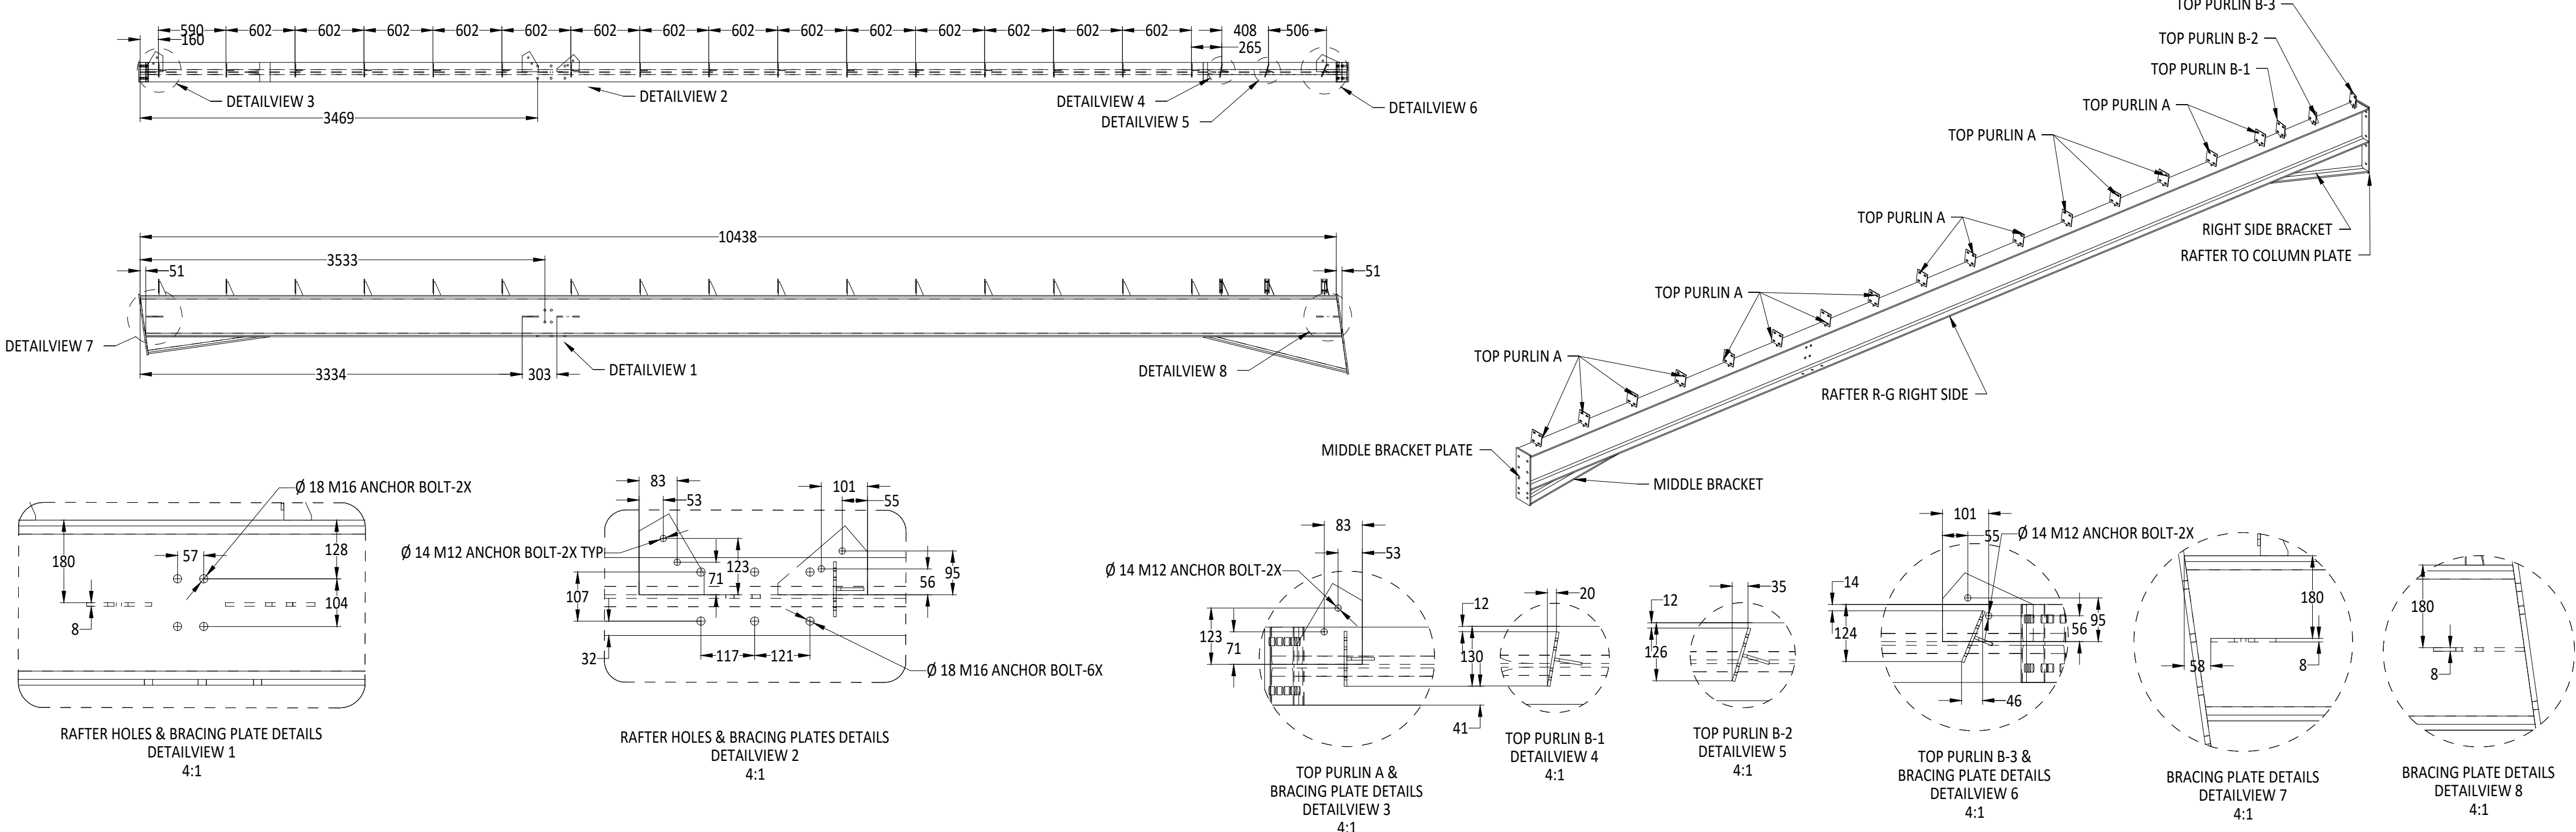

RAFTER R-G RIGHT FABRICATION DETAILS

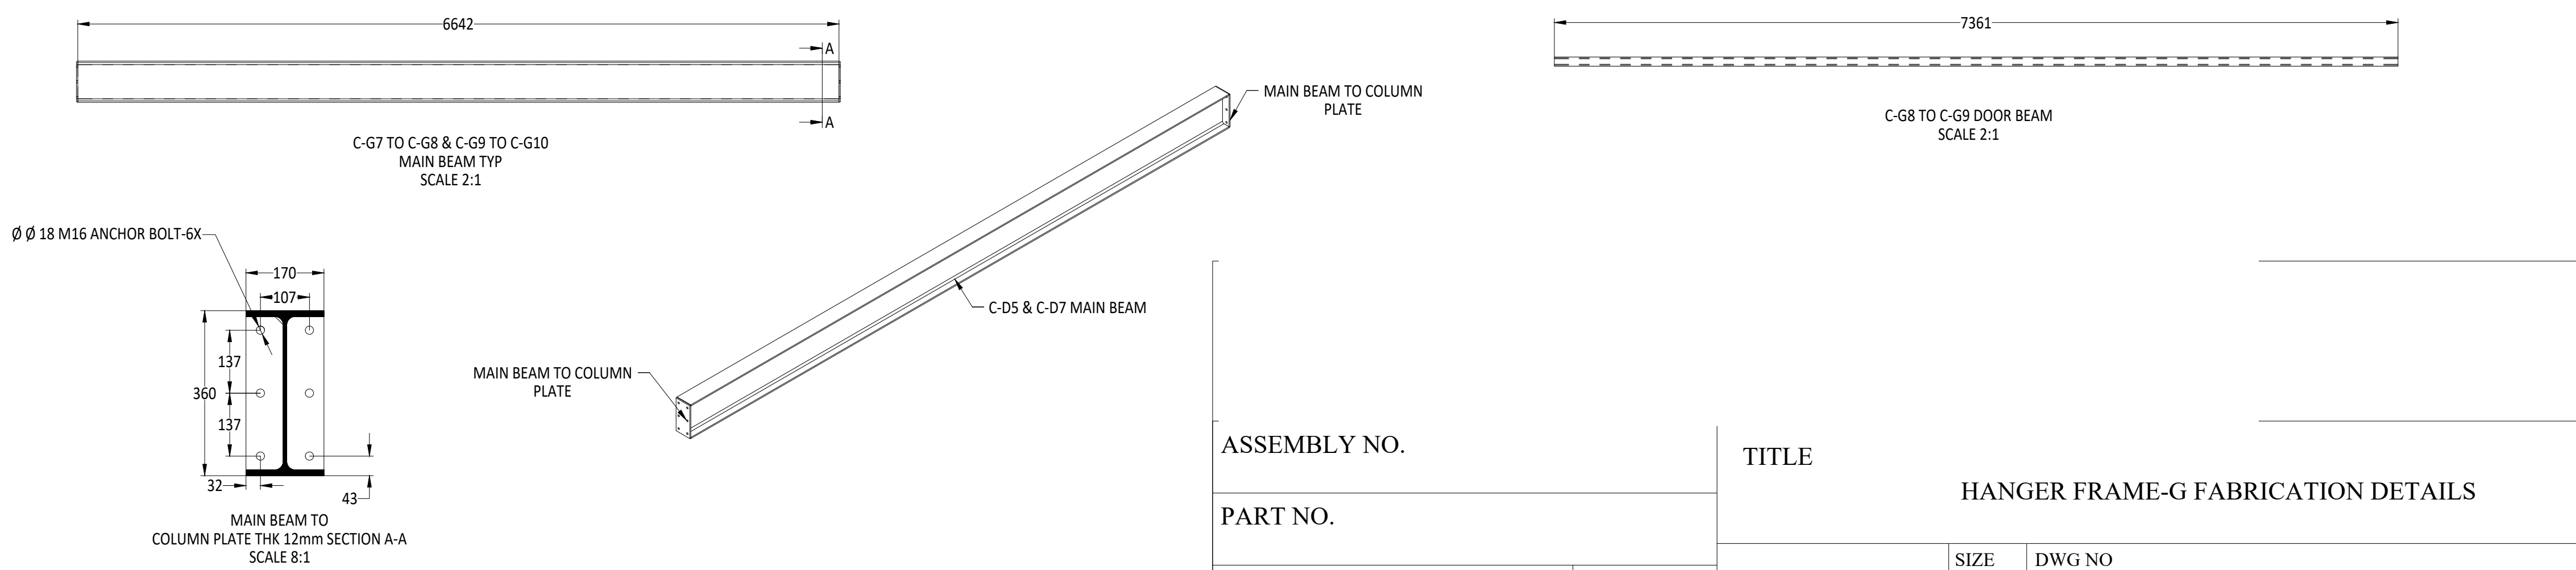

MAIN BEAMS FABRICATION DETAILS

ASSEMBLY NO.		TITLE	
PART NO.		HANGER FRAME-G FABRICATION DETAILS	
DESIGNER		SIZE	DWG NO
APPROVED		A0	00
SCALE AS SHOWN		RELEASE DATE	21/08/2025
		WEIGHT Kg.	QTY.